

*Дизайн-проект  
Частный дом. ЖК МонакоВо!*



*Заказчик Мельников Д.А.*



*Дизайнер Т. Астафьева 8 915 360 0663*



## Содержание дизайн-проекта

Лист	Наименование	Лист	Наименование
1	Обмерный план цокольный этаж	25	Схема расположения светильников цокольный этаж
2	Обмерный план 1-й этаж	26	Схема расположения светильников 1-й этаж
3	Обмерный план 2-й этаж	27	Схема расположения светильников 2-й этаж
4	Экспликация помещений цокольный этаж	28	Схема расположения теплых полов цокольный этаж
5	Экспликация помещений 1-й этаж	29	Схема расположения теплых полов 1 этаж
6	Экспликация помещений 2-й этаж	30	Схема расположения теплых полов 2-й этаж
7	План расстановки мебели цокольный этаж	31	Дизайн-проект камина
8	План расстановки мебели 1-й этаж	32	Разрез всего дома с лестницей
9	План расстановки мебели 2-й этаж	33	Конструктивный узел
10	Монтажно-демонтажный план цокольный этаж		
11	Монтажно-демонтажный план 1-й этаж		
12	Монтажно-демонтажный план 2-й этаж		
13	План полов цокольный этаж		
14	План полов 1-й этаж		
15	План полов 2-й этаж		
16	Схема сантехники цокольный этаж		
17	Схема сантехники 1-й этаж		
18	Схема сантехники 2-й этаж		
19	Схема электрики цокольный этаж		
20	Схема электрики 1-й этаж		
21	Схема электрики 2-й этаж		
22	План потолков цокольный этаж		
23	План потолков 1-й этаж		
24	План потолков 2-й этаж		

## *Обмерный план цокольный этаж*

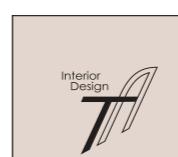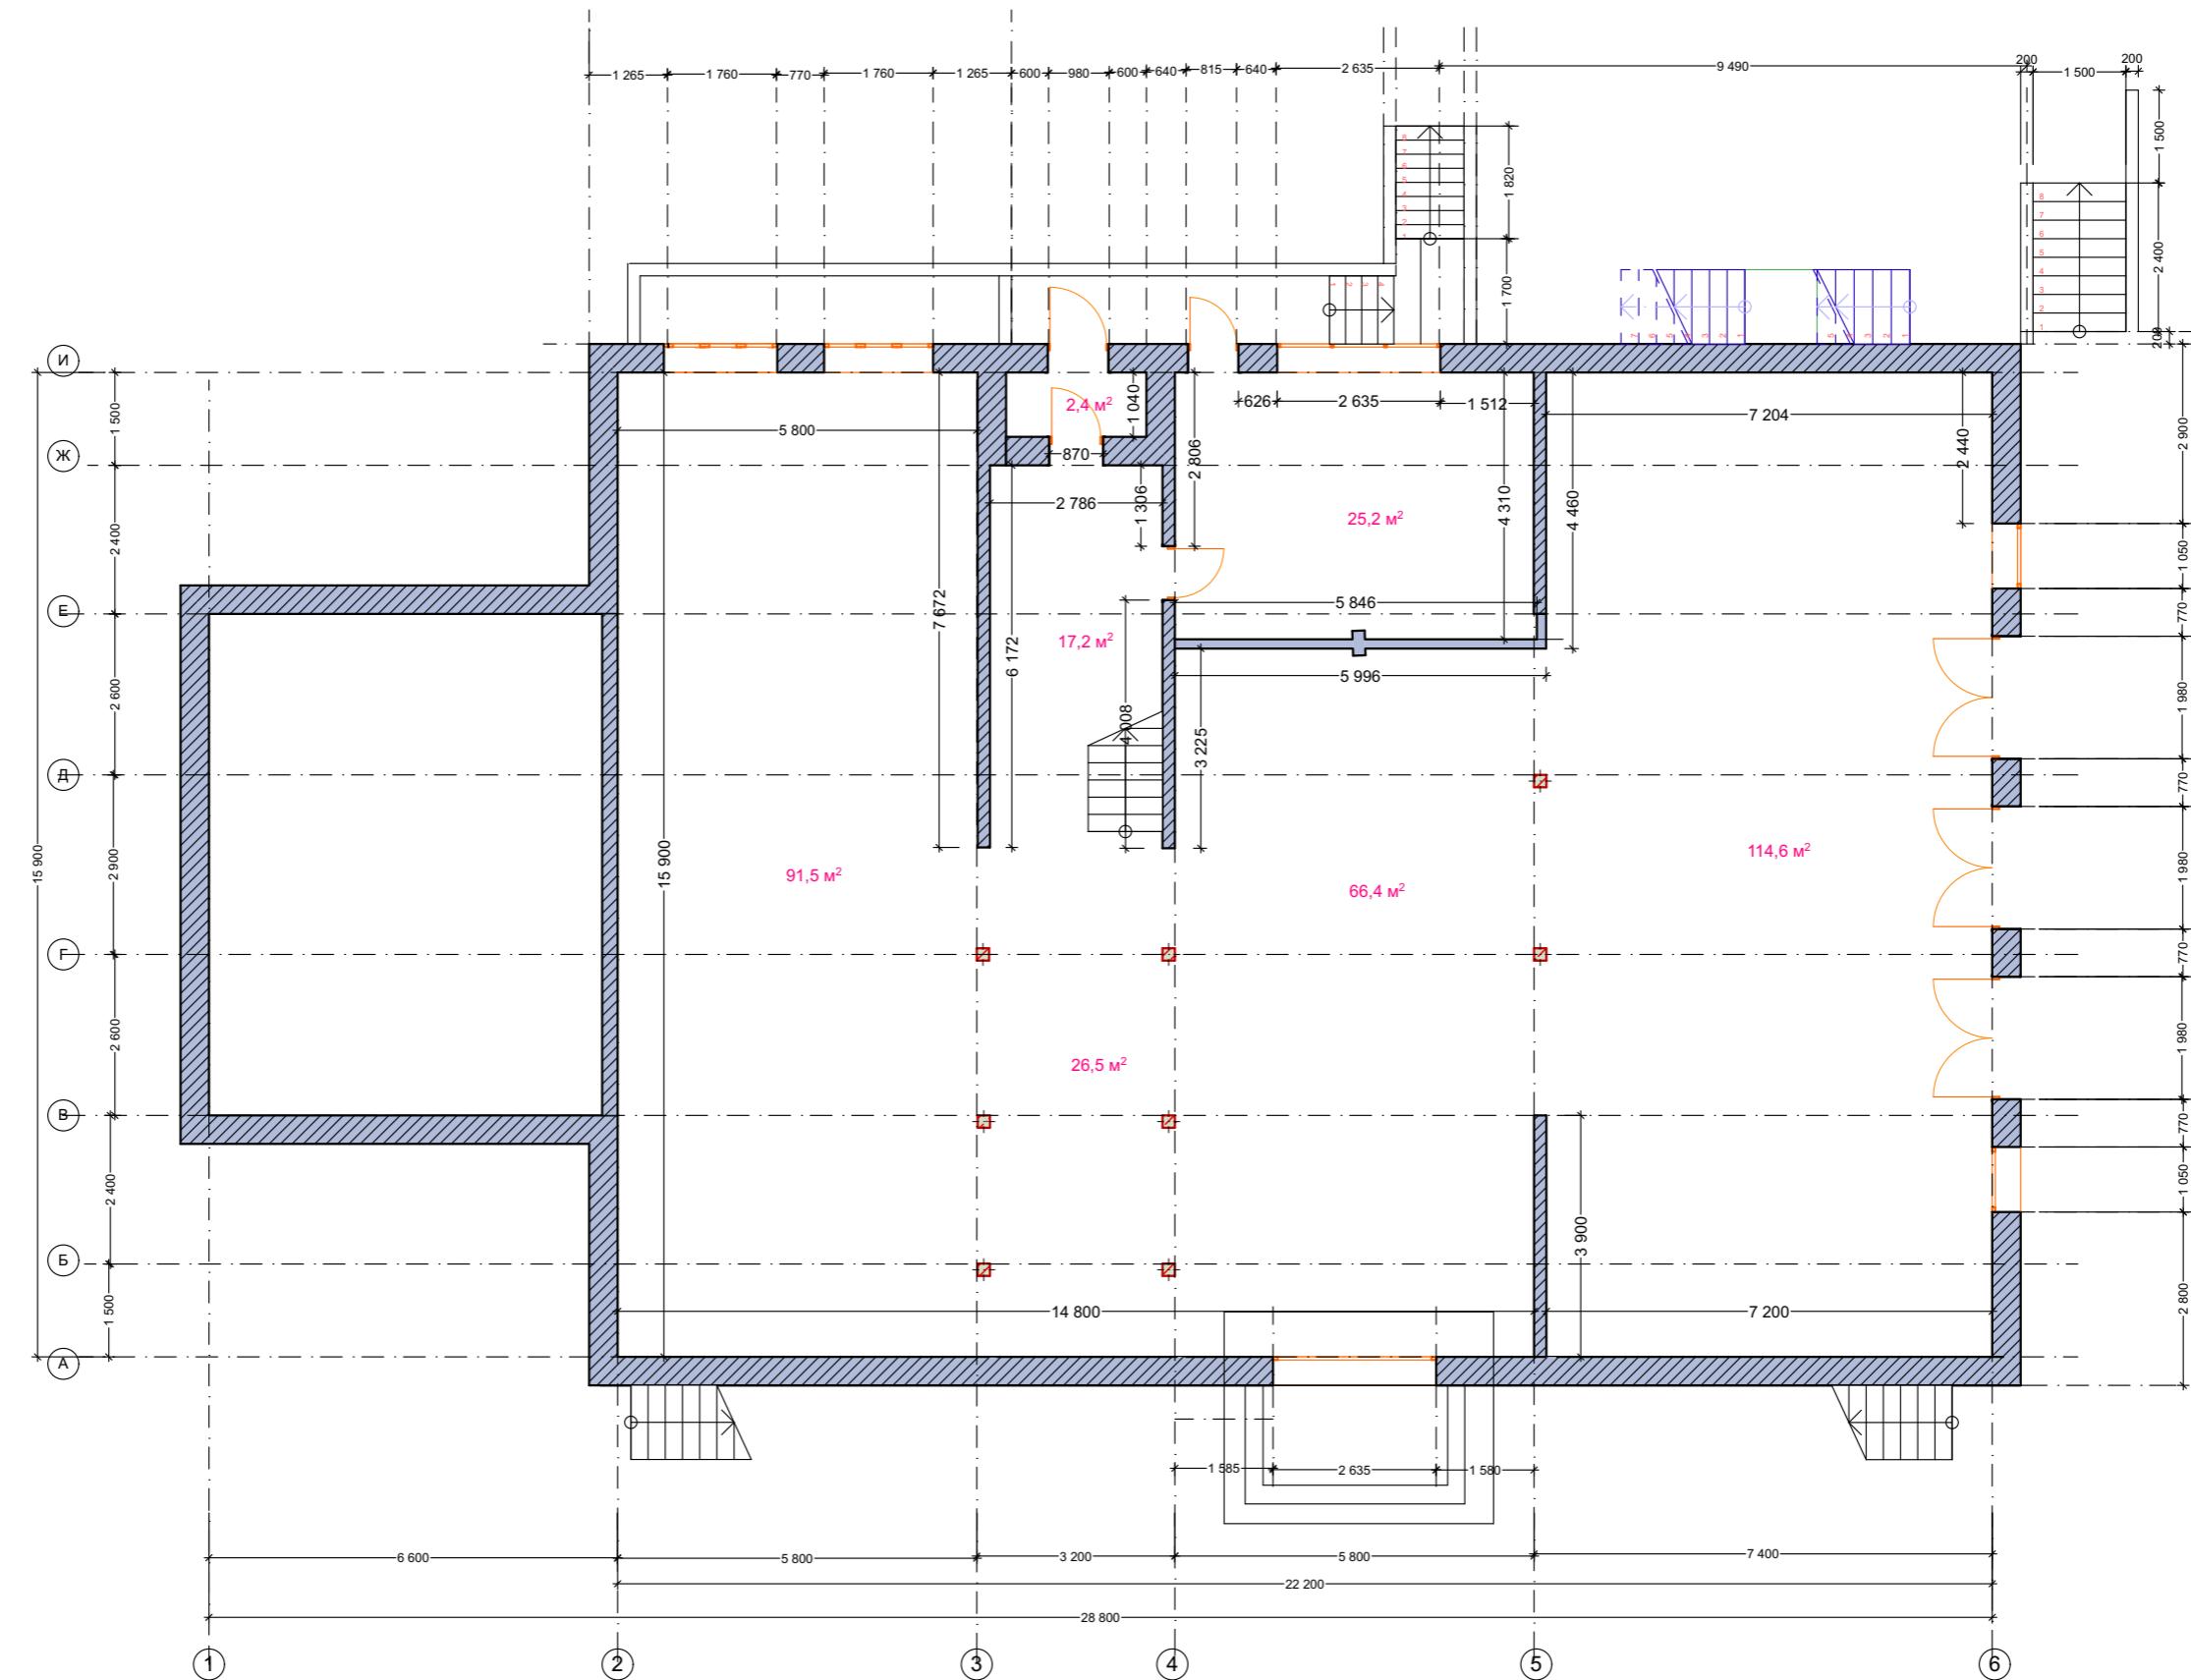

Частный дом. ЖК МонакоВо!


Дом у Озера

Масштаб 1:120

*Дизайнер Т. Астафьева 8 915 360 0663*

Лист 22 из 11

## Обмерный план 1-й этаж

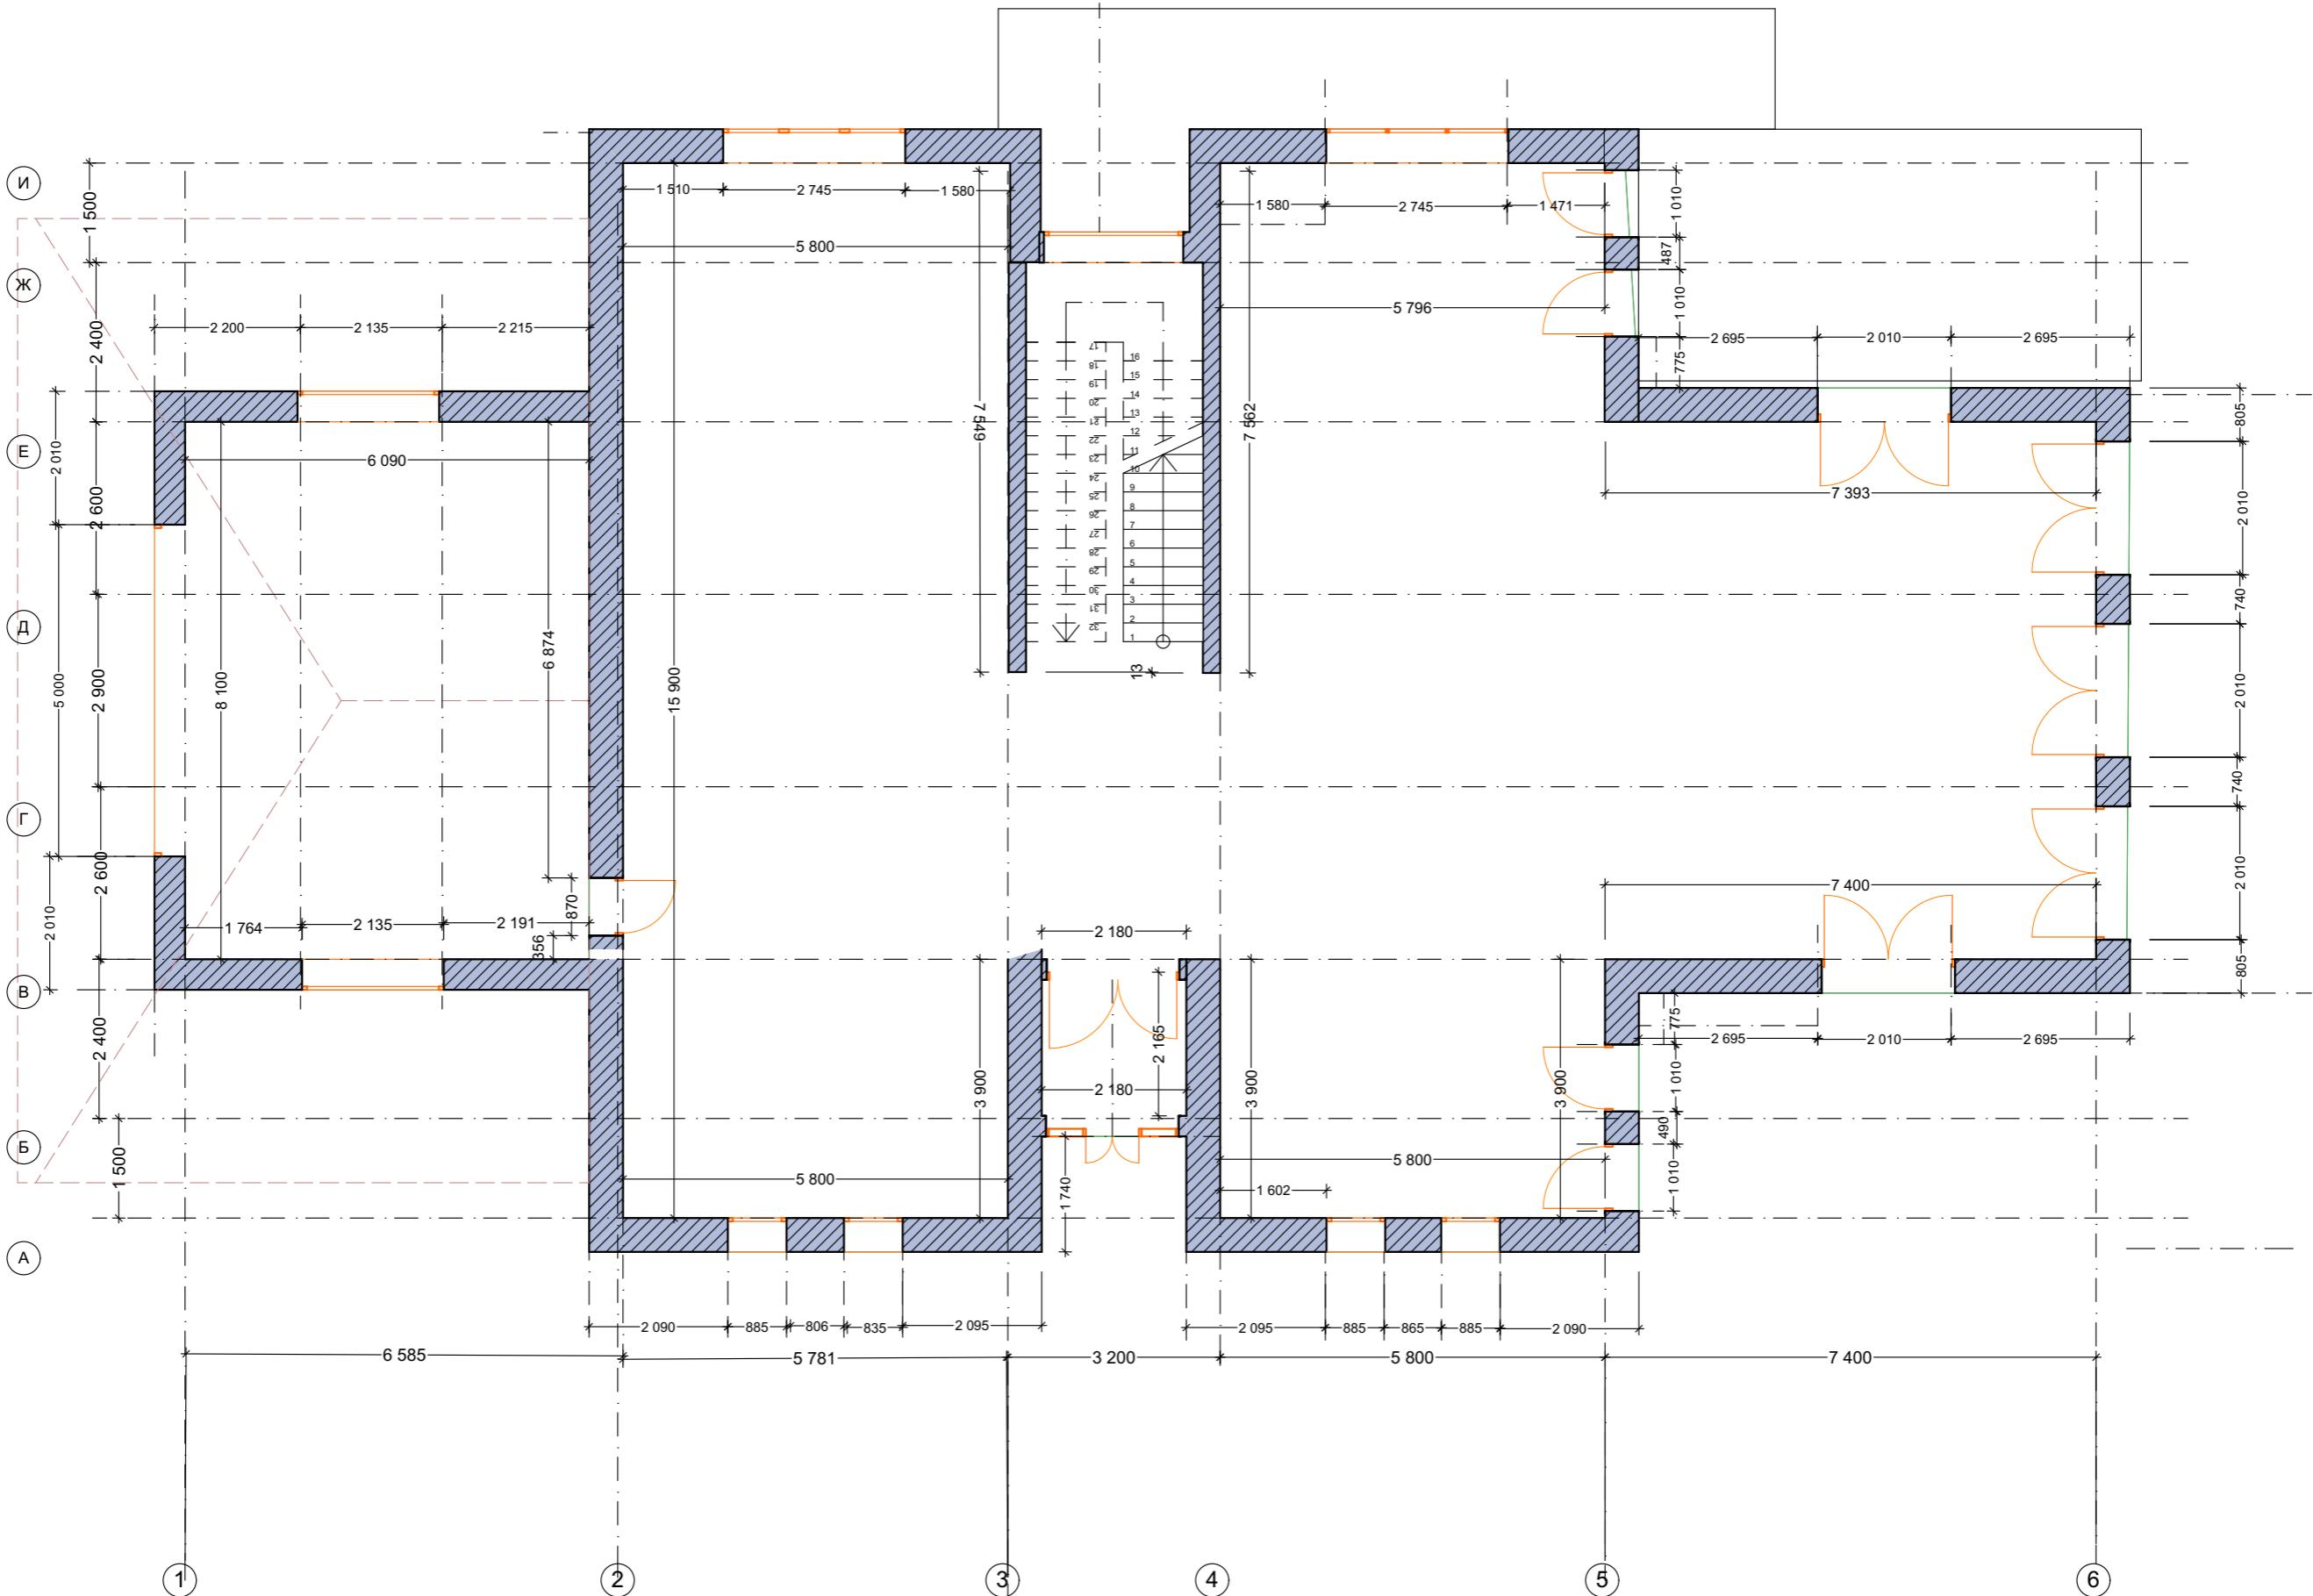

Частный дом. ЖК МонакоВо!




Дом у Озера

Масштаб 1:100

Дизайнер Т. Астафьева 8 915 360 0663

Лист 23 из 11

## Обмерный план 2-й этаж

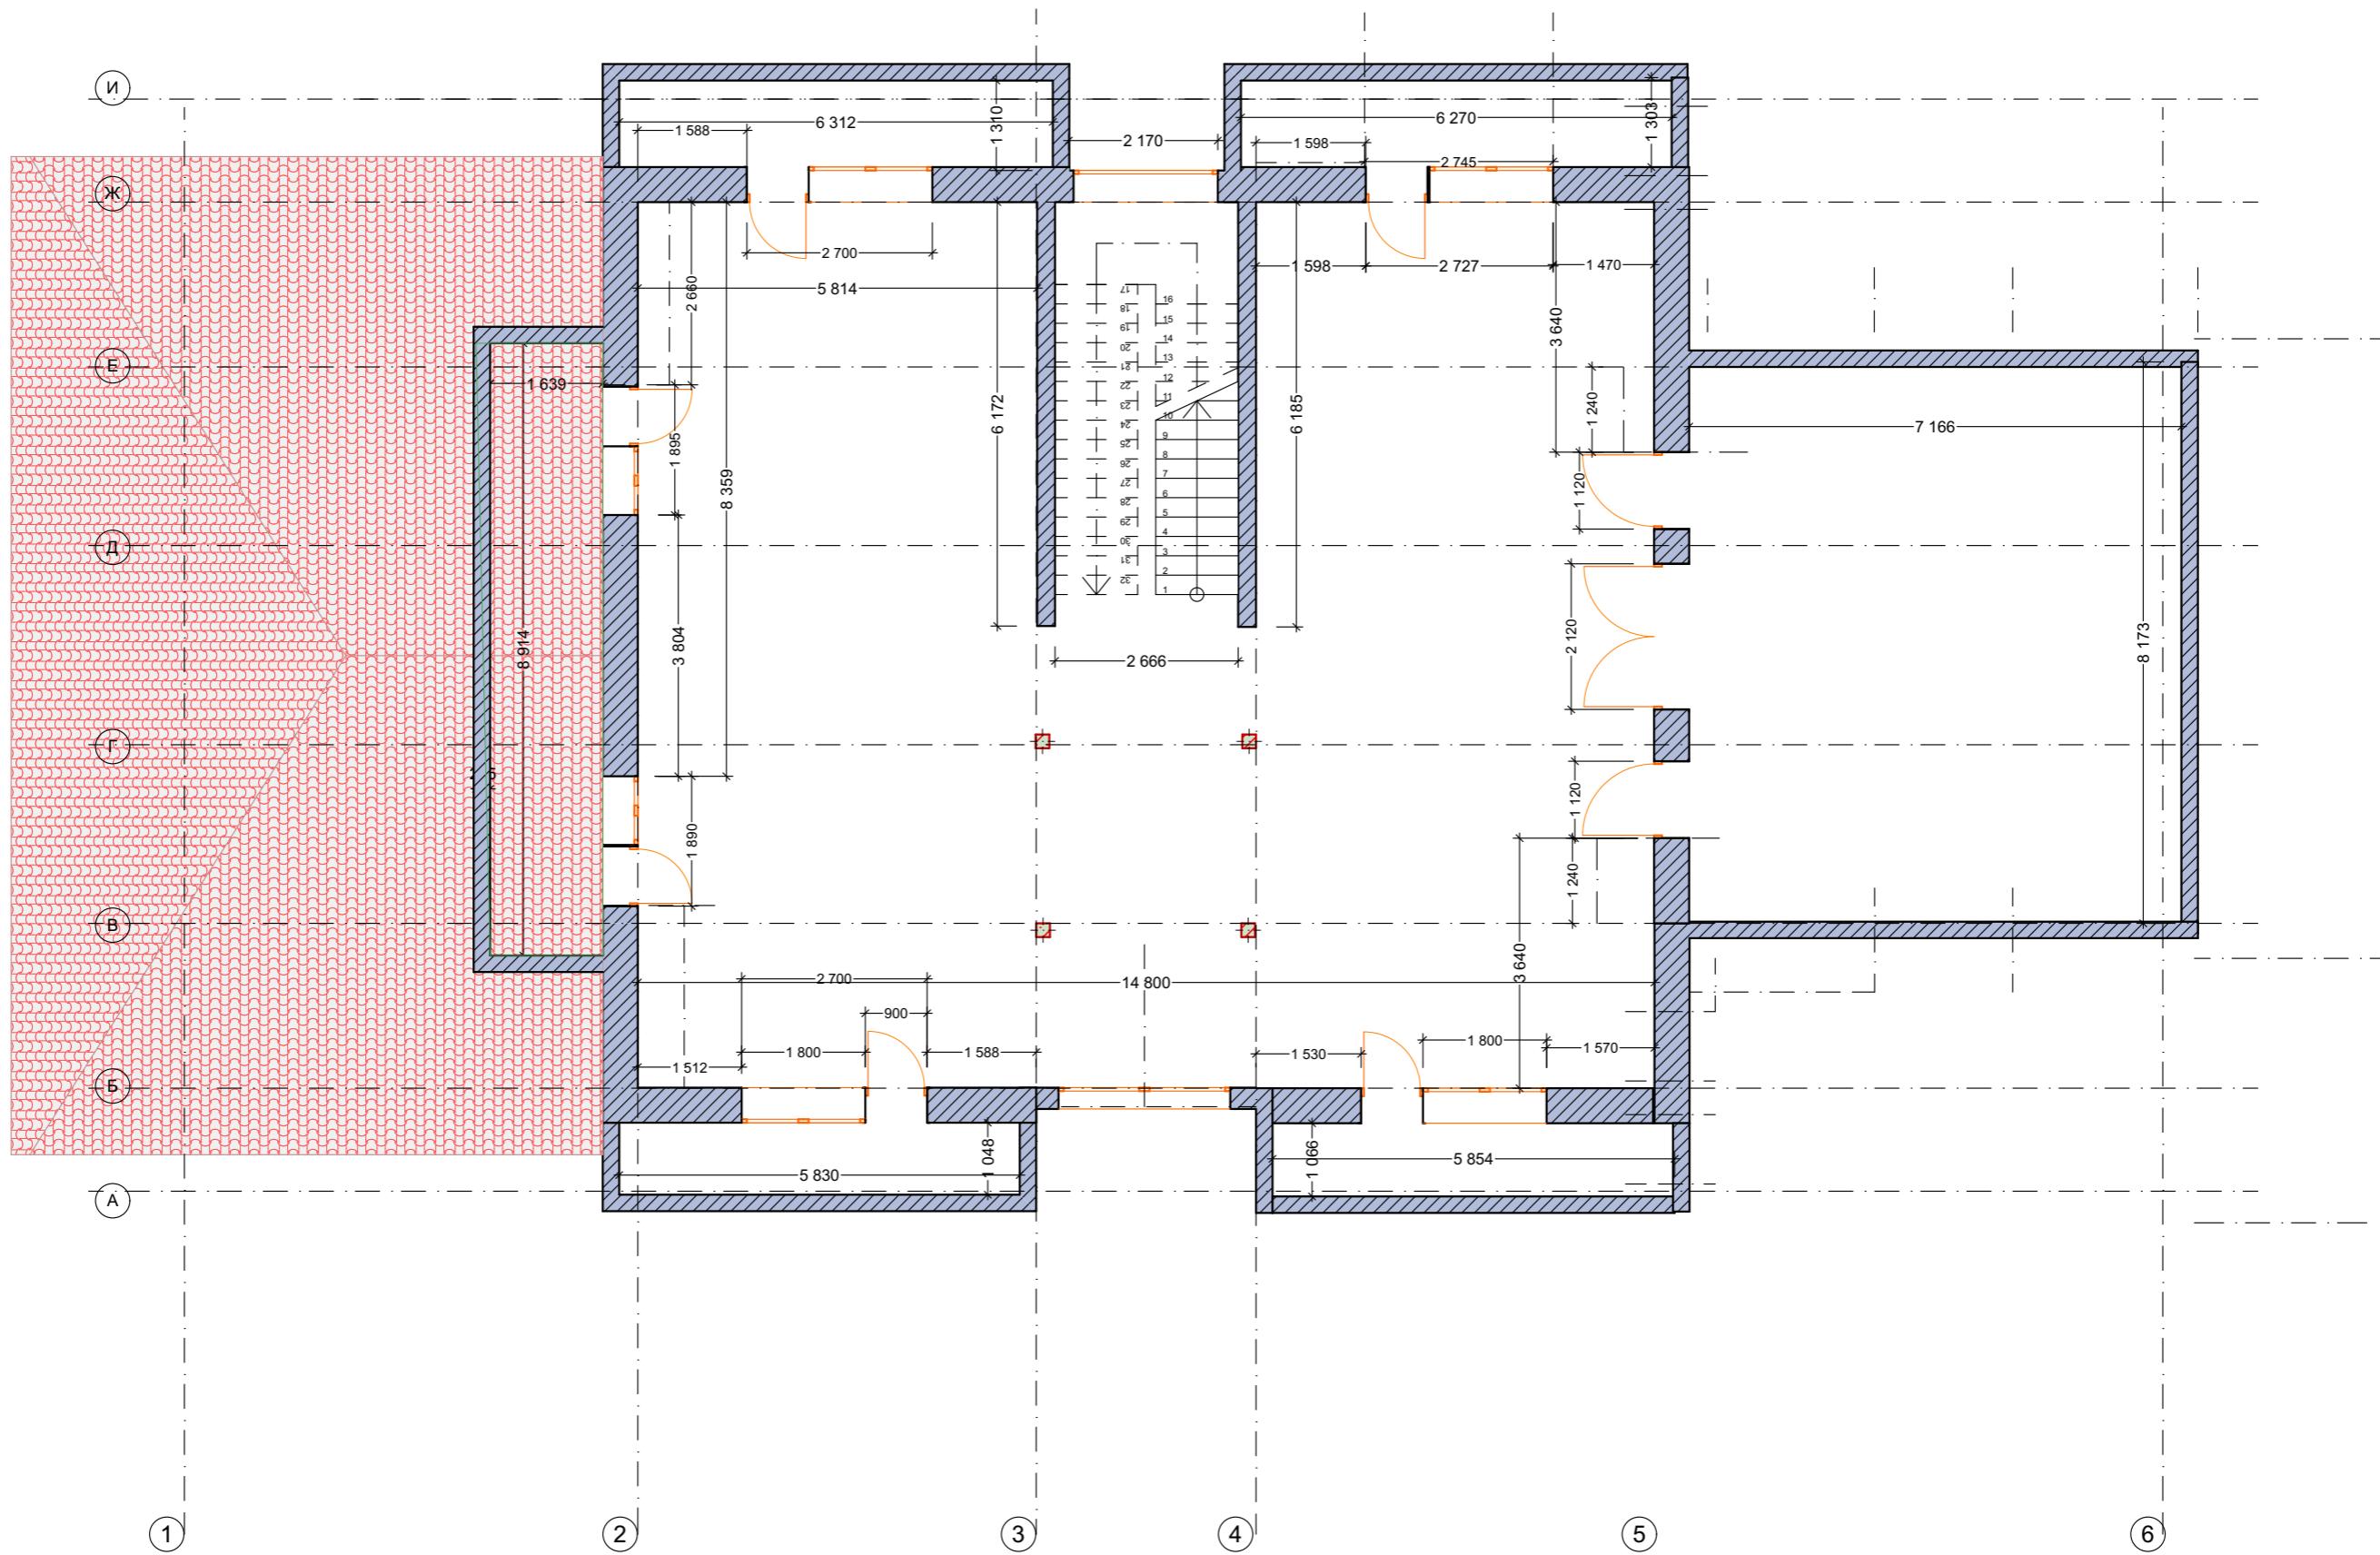


	Частный дом. ЖК МонакоВо!
	Дом у Озера
	Масштаб 1:100

Дизайнер Т. Астафьев 8 915 360 0663

Лист 24 из 11

# Экспликация помещений цокольный этаж

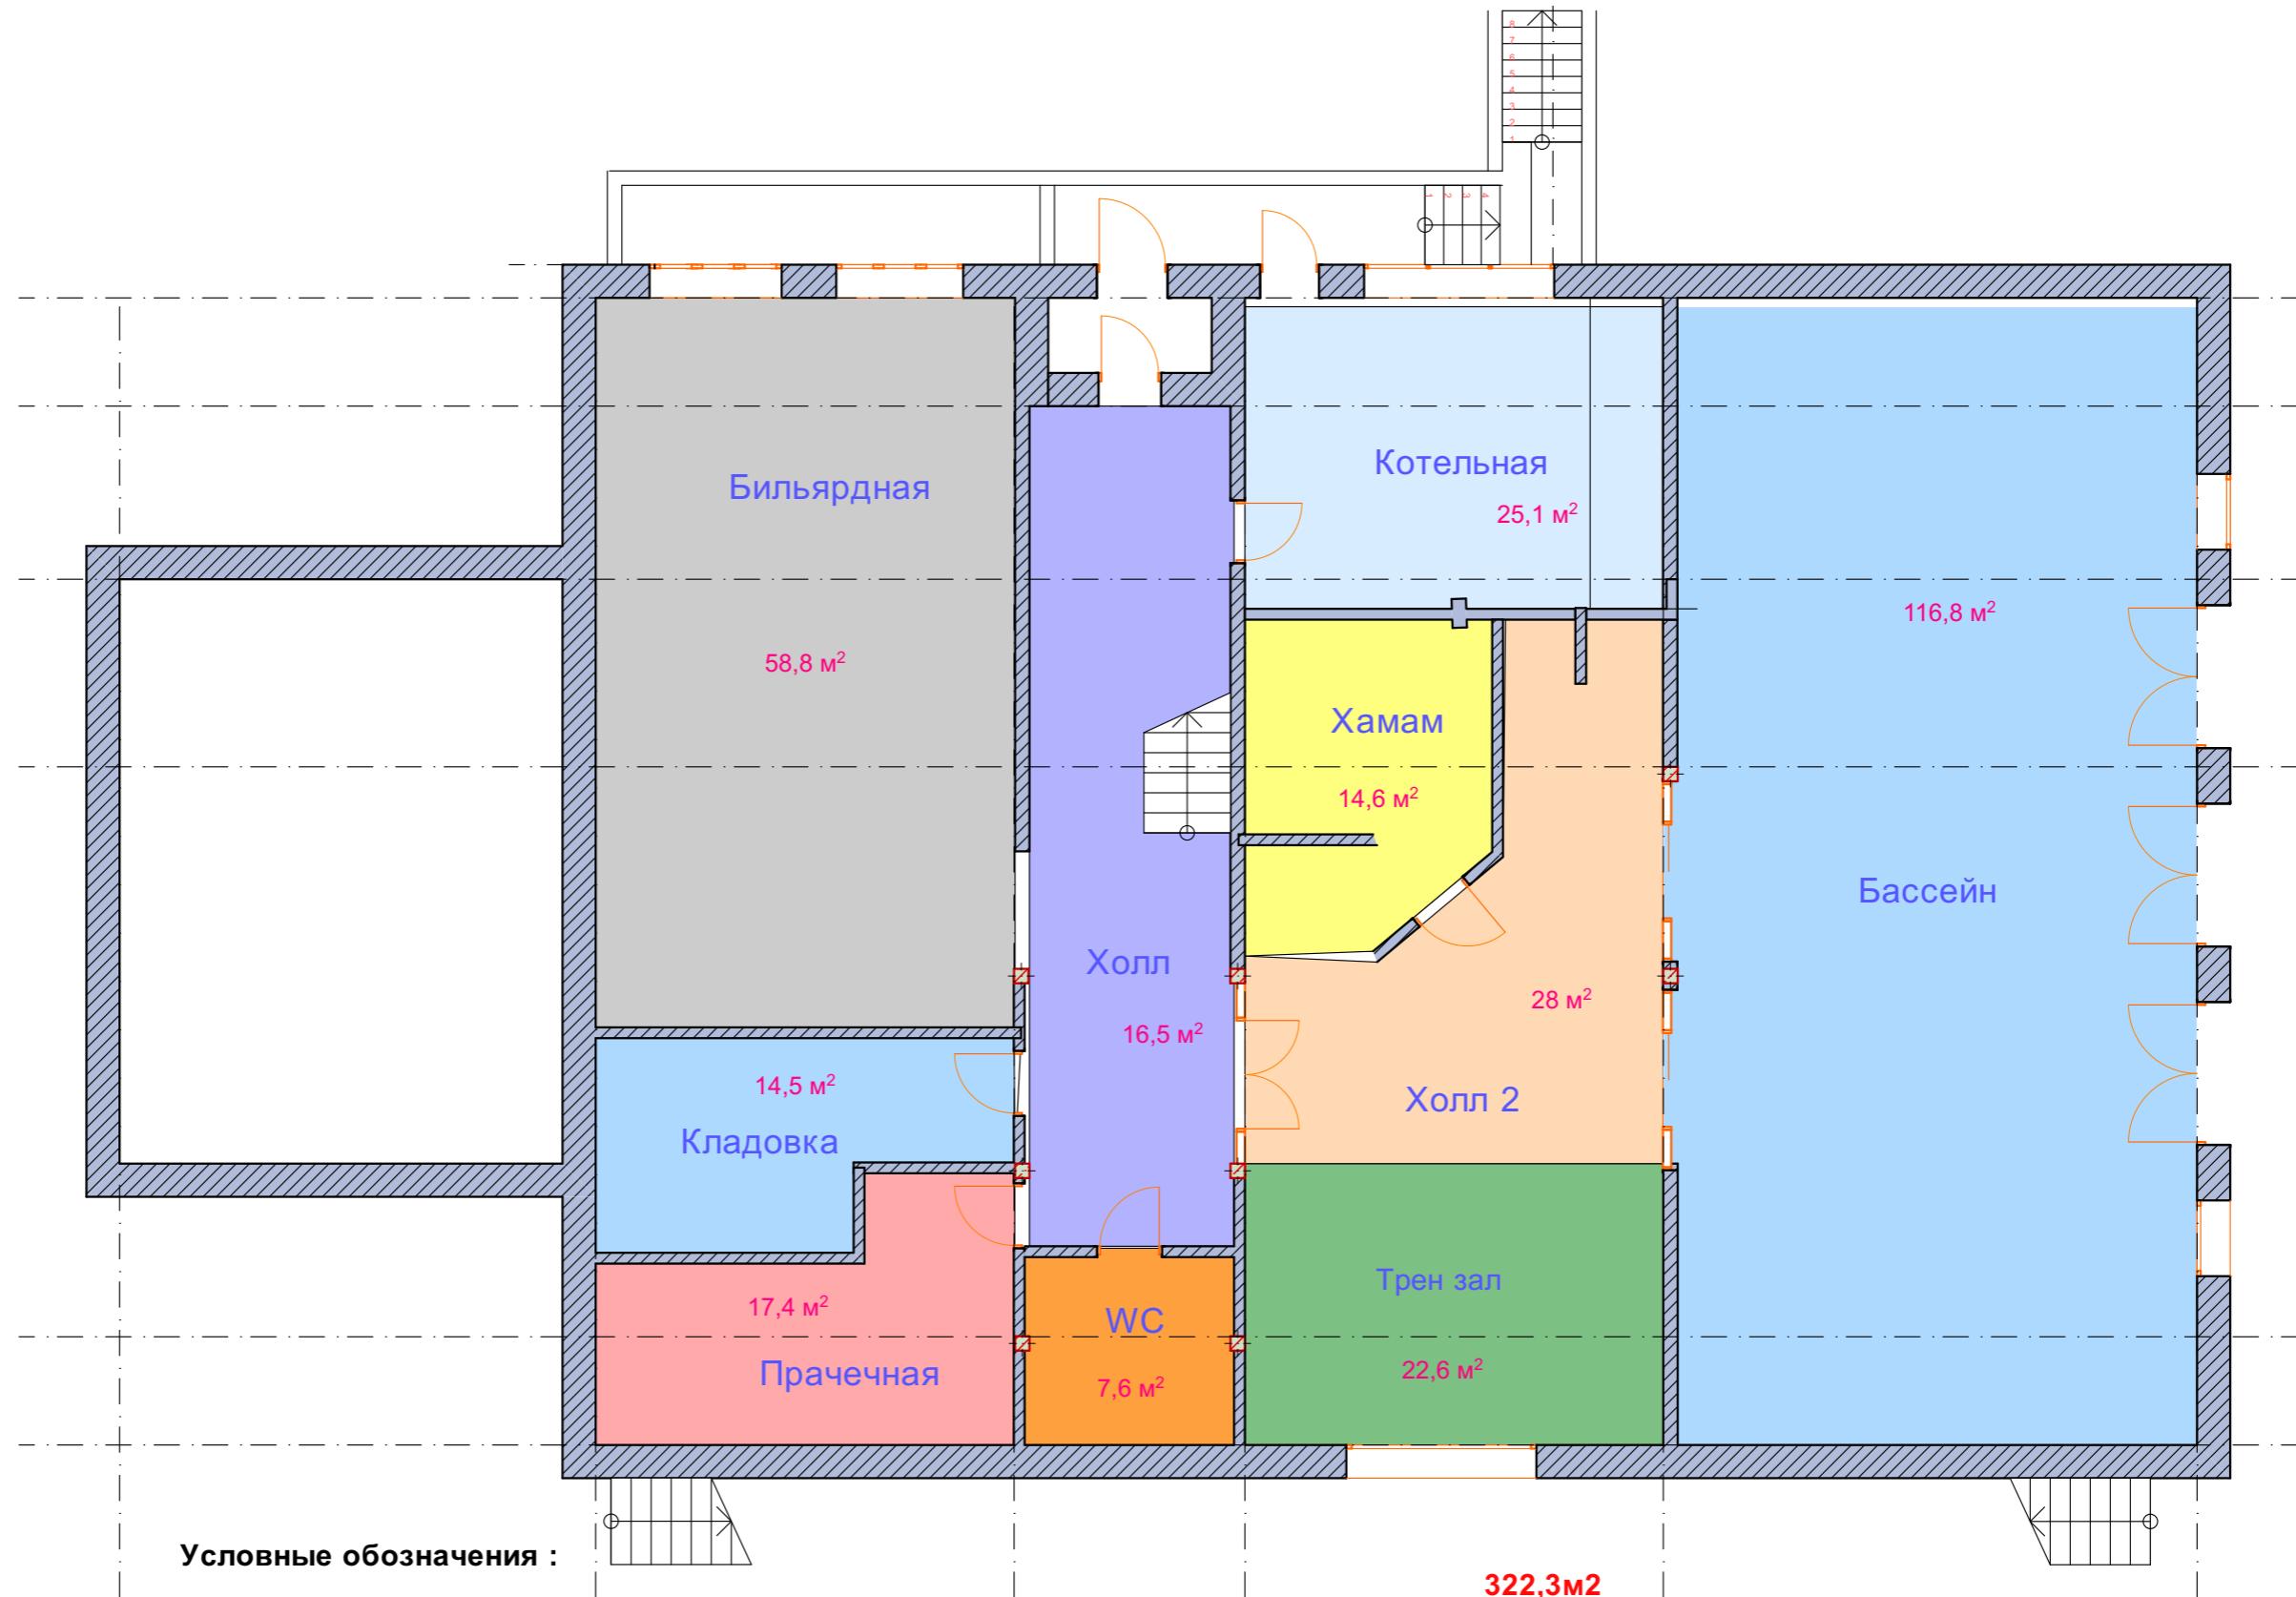


## Условные обозначения :

	-Холл		-Тренаж.зал
	-Бильярдная		-Холл 2
	- Кладовая		-Хамам
	- Прачечная		-Котельная
	-WC		-Бассейн

Общая площадь: 338,5м<sup>2</sup>

# Экспликация помещений 1-й этаж

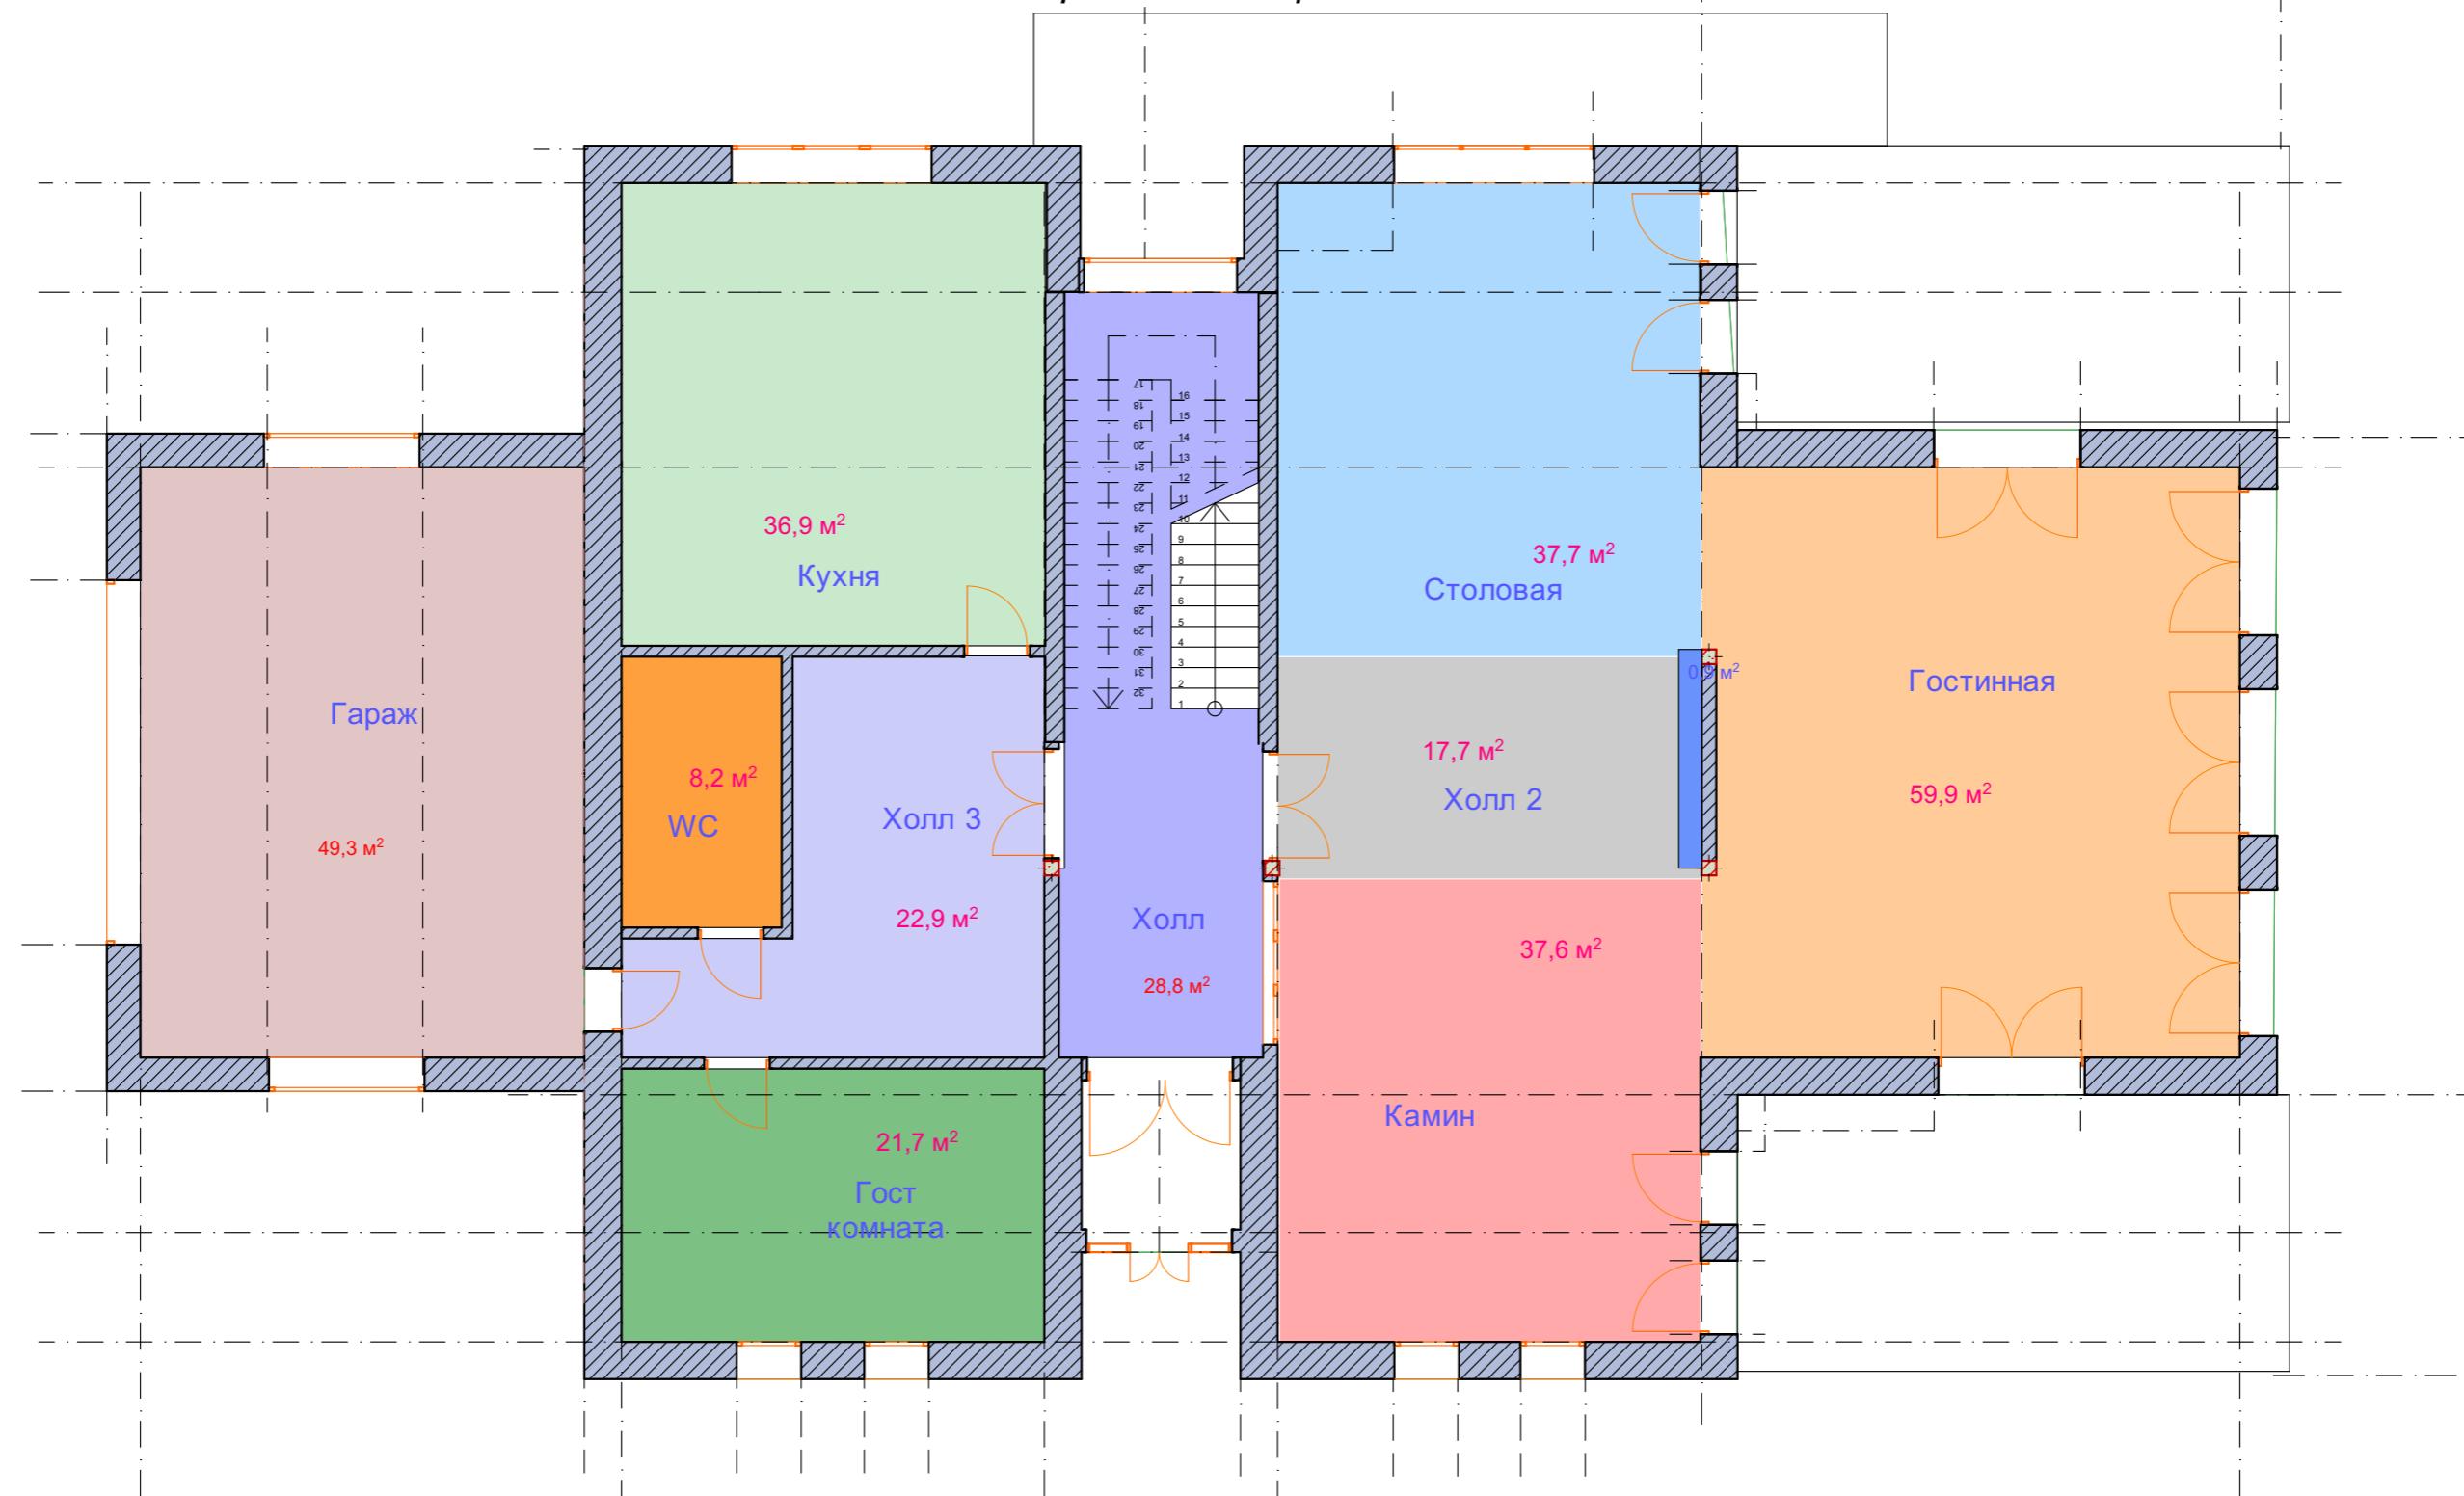

## Условные обозначения :

	-Холл		-Столовая
	-Холл 2		-Холл 3
	- Столовая		-Гостевая комната
	- Камин		-WC
	- Гараж		-Кухня


Общая площадь: 320,7м<sup>2</sup>

	Частный дом. ЖК МонакоВо!
	Дом у Озера
	Масштаб 1:100

Дизайнер Т. Астафьев 8 915 360 0663

Лист 26 из 11

## Экспликация помещений 2-й этаж

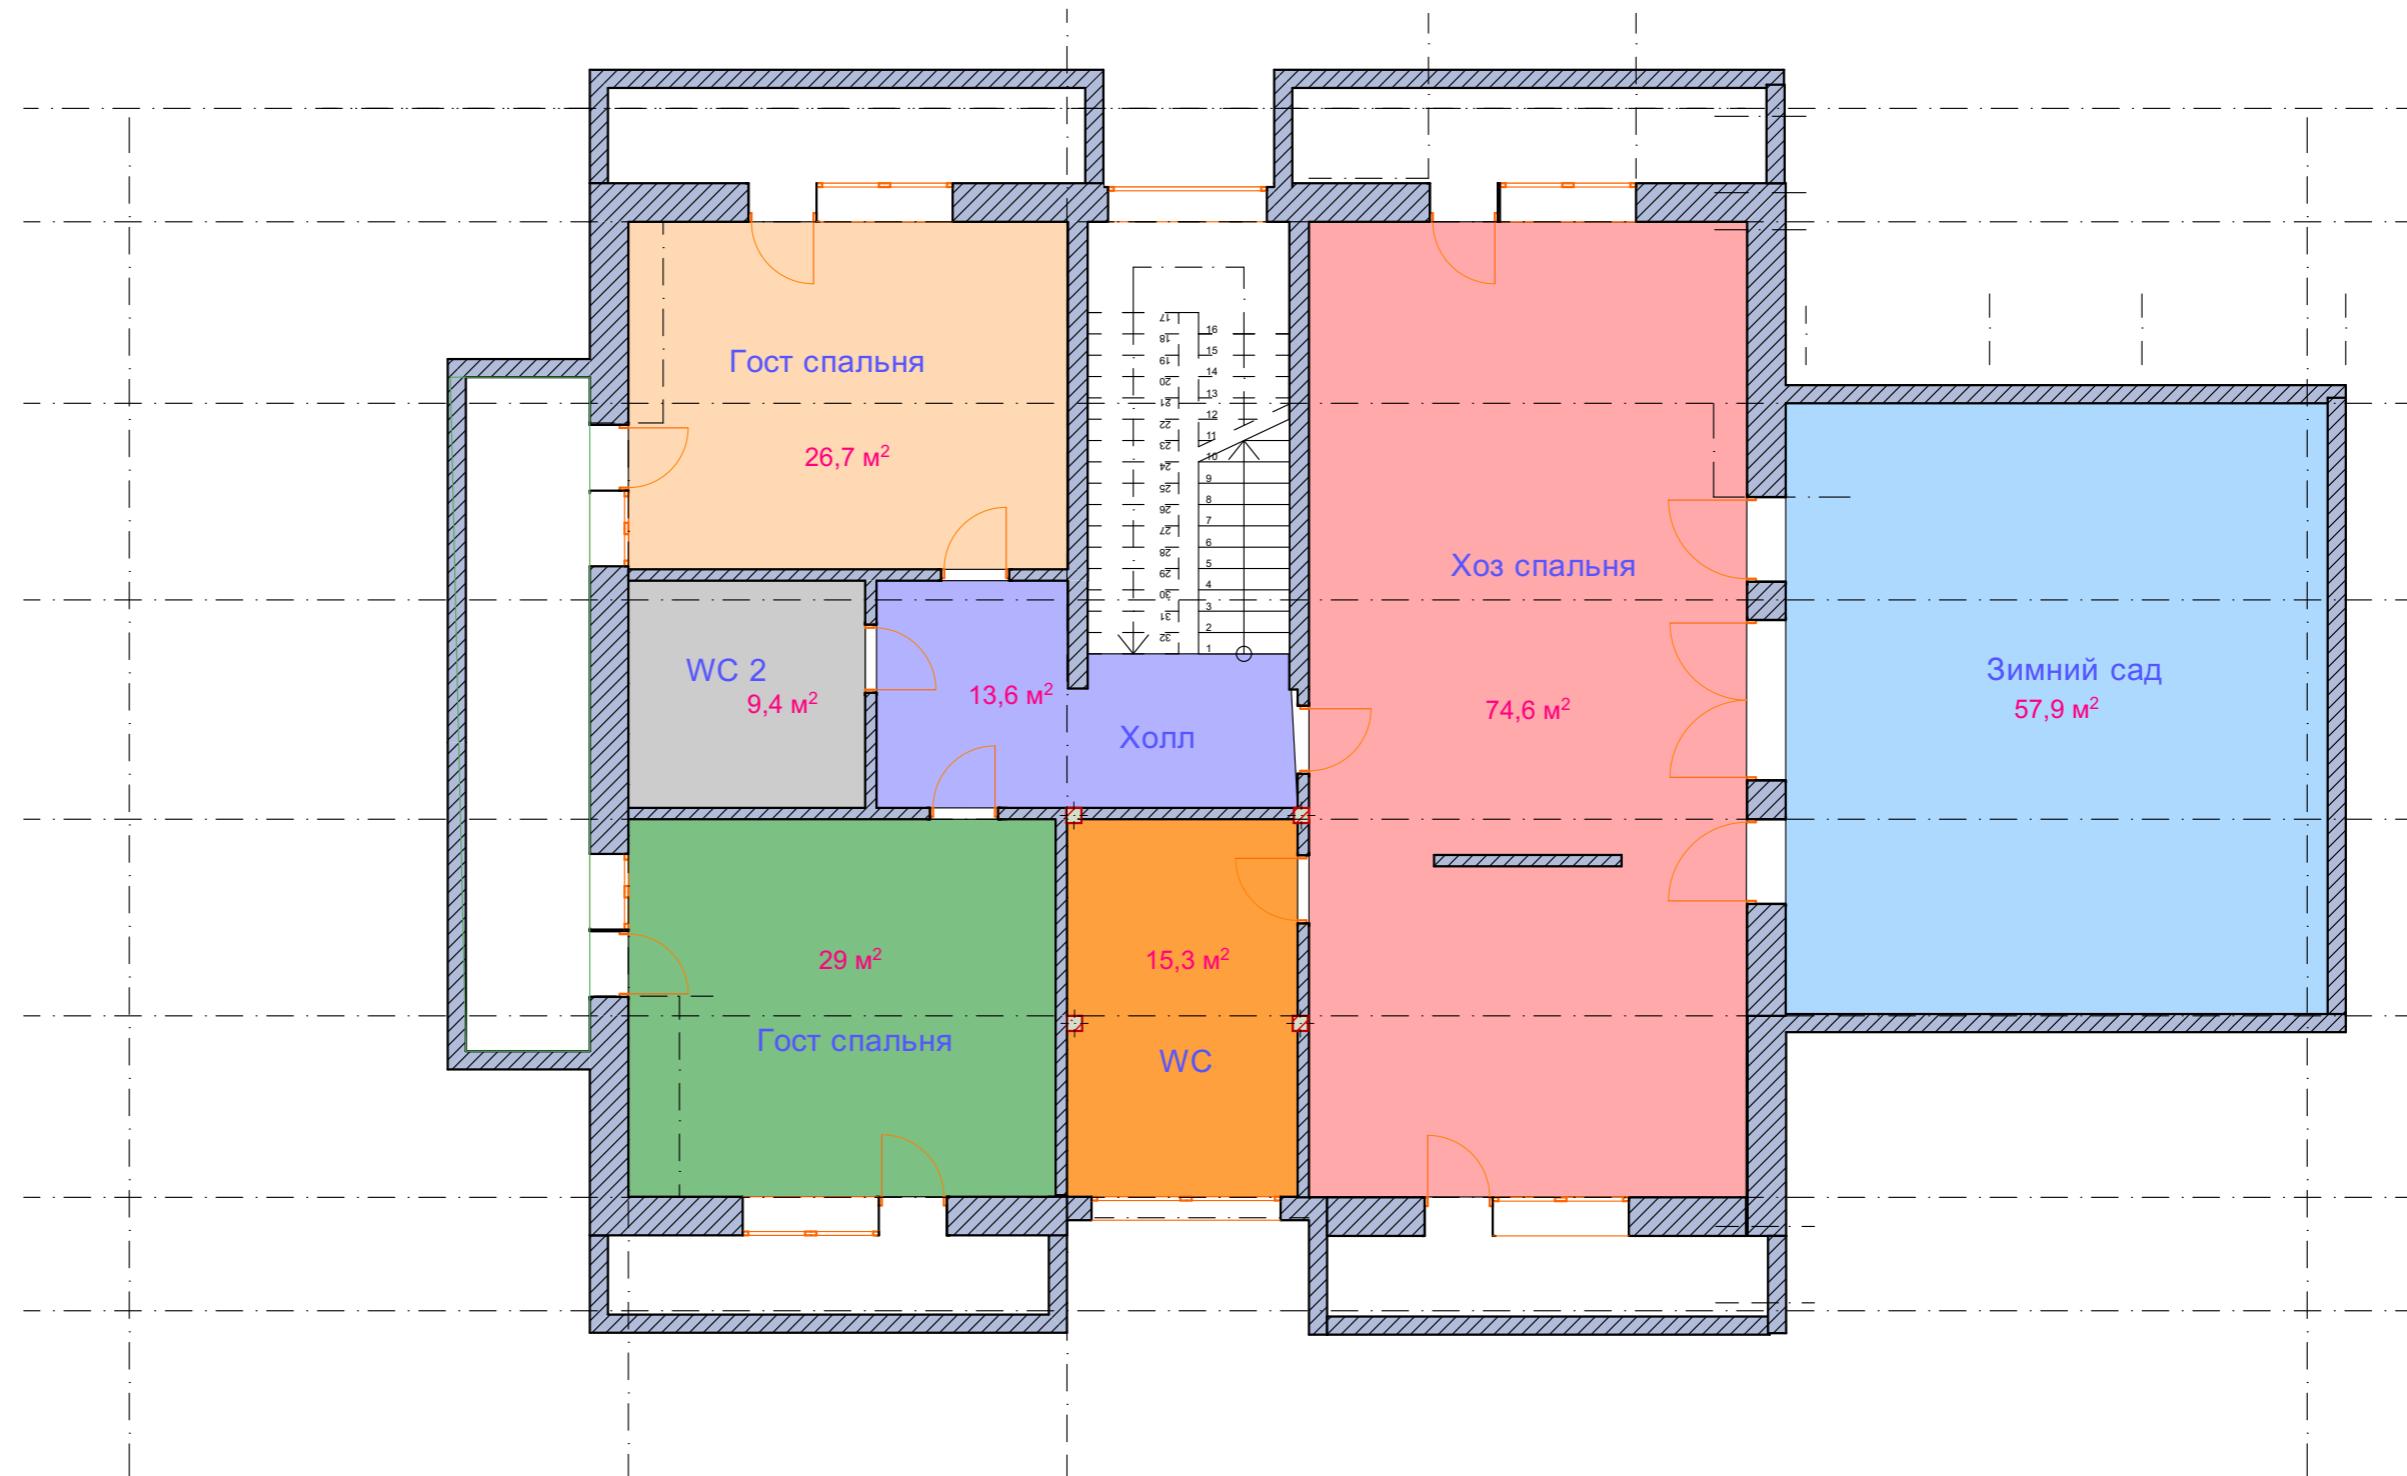

### Условные обозначения :

[Light Blue Box]	-Холл	[Green Box]	-Гостевая спальня
[Grey Box]	-WC 2	[Orange Box]	-Гостевая спальня 2
[Light Blue Box]	- Зимн.Сад		
[Pink Box]	- Хоз.спальня		
[Orange Box]	-WC		

Общая площадь: 226,4м<sup>2</sup>



Частный дом. ЖК МонакоВо!


Дом у Озера

Масштаб 1:100

Дизайнер Т. Астафьева 8 915 360 0663


Лист 27 из 11

План расстановки мебели цокольный этаж

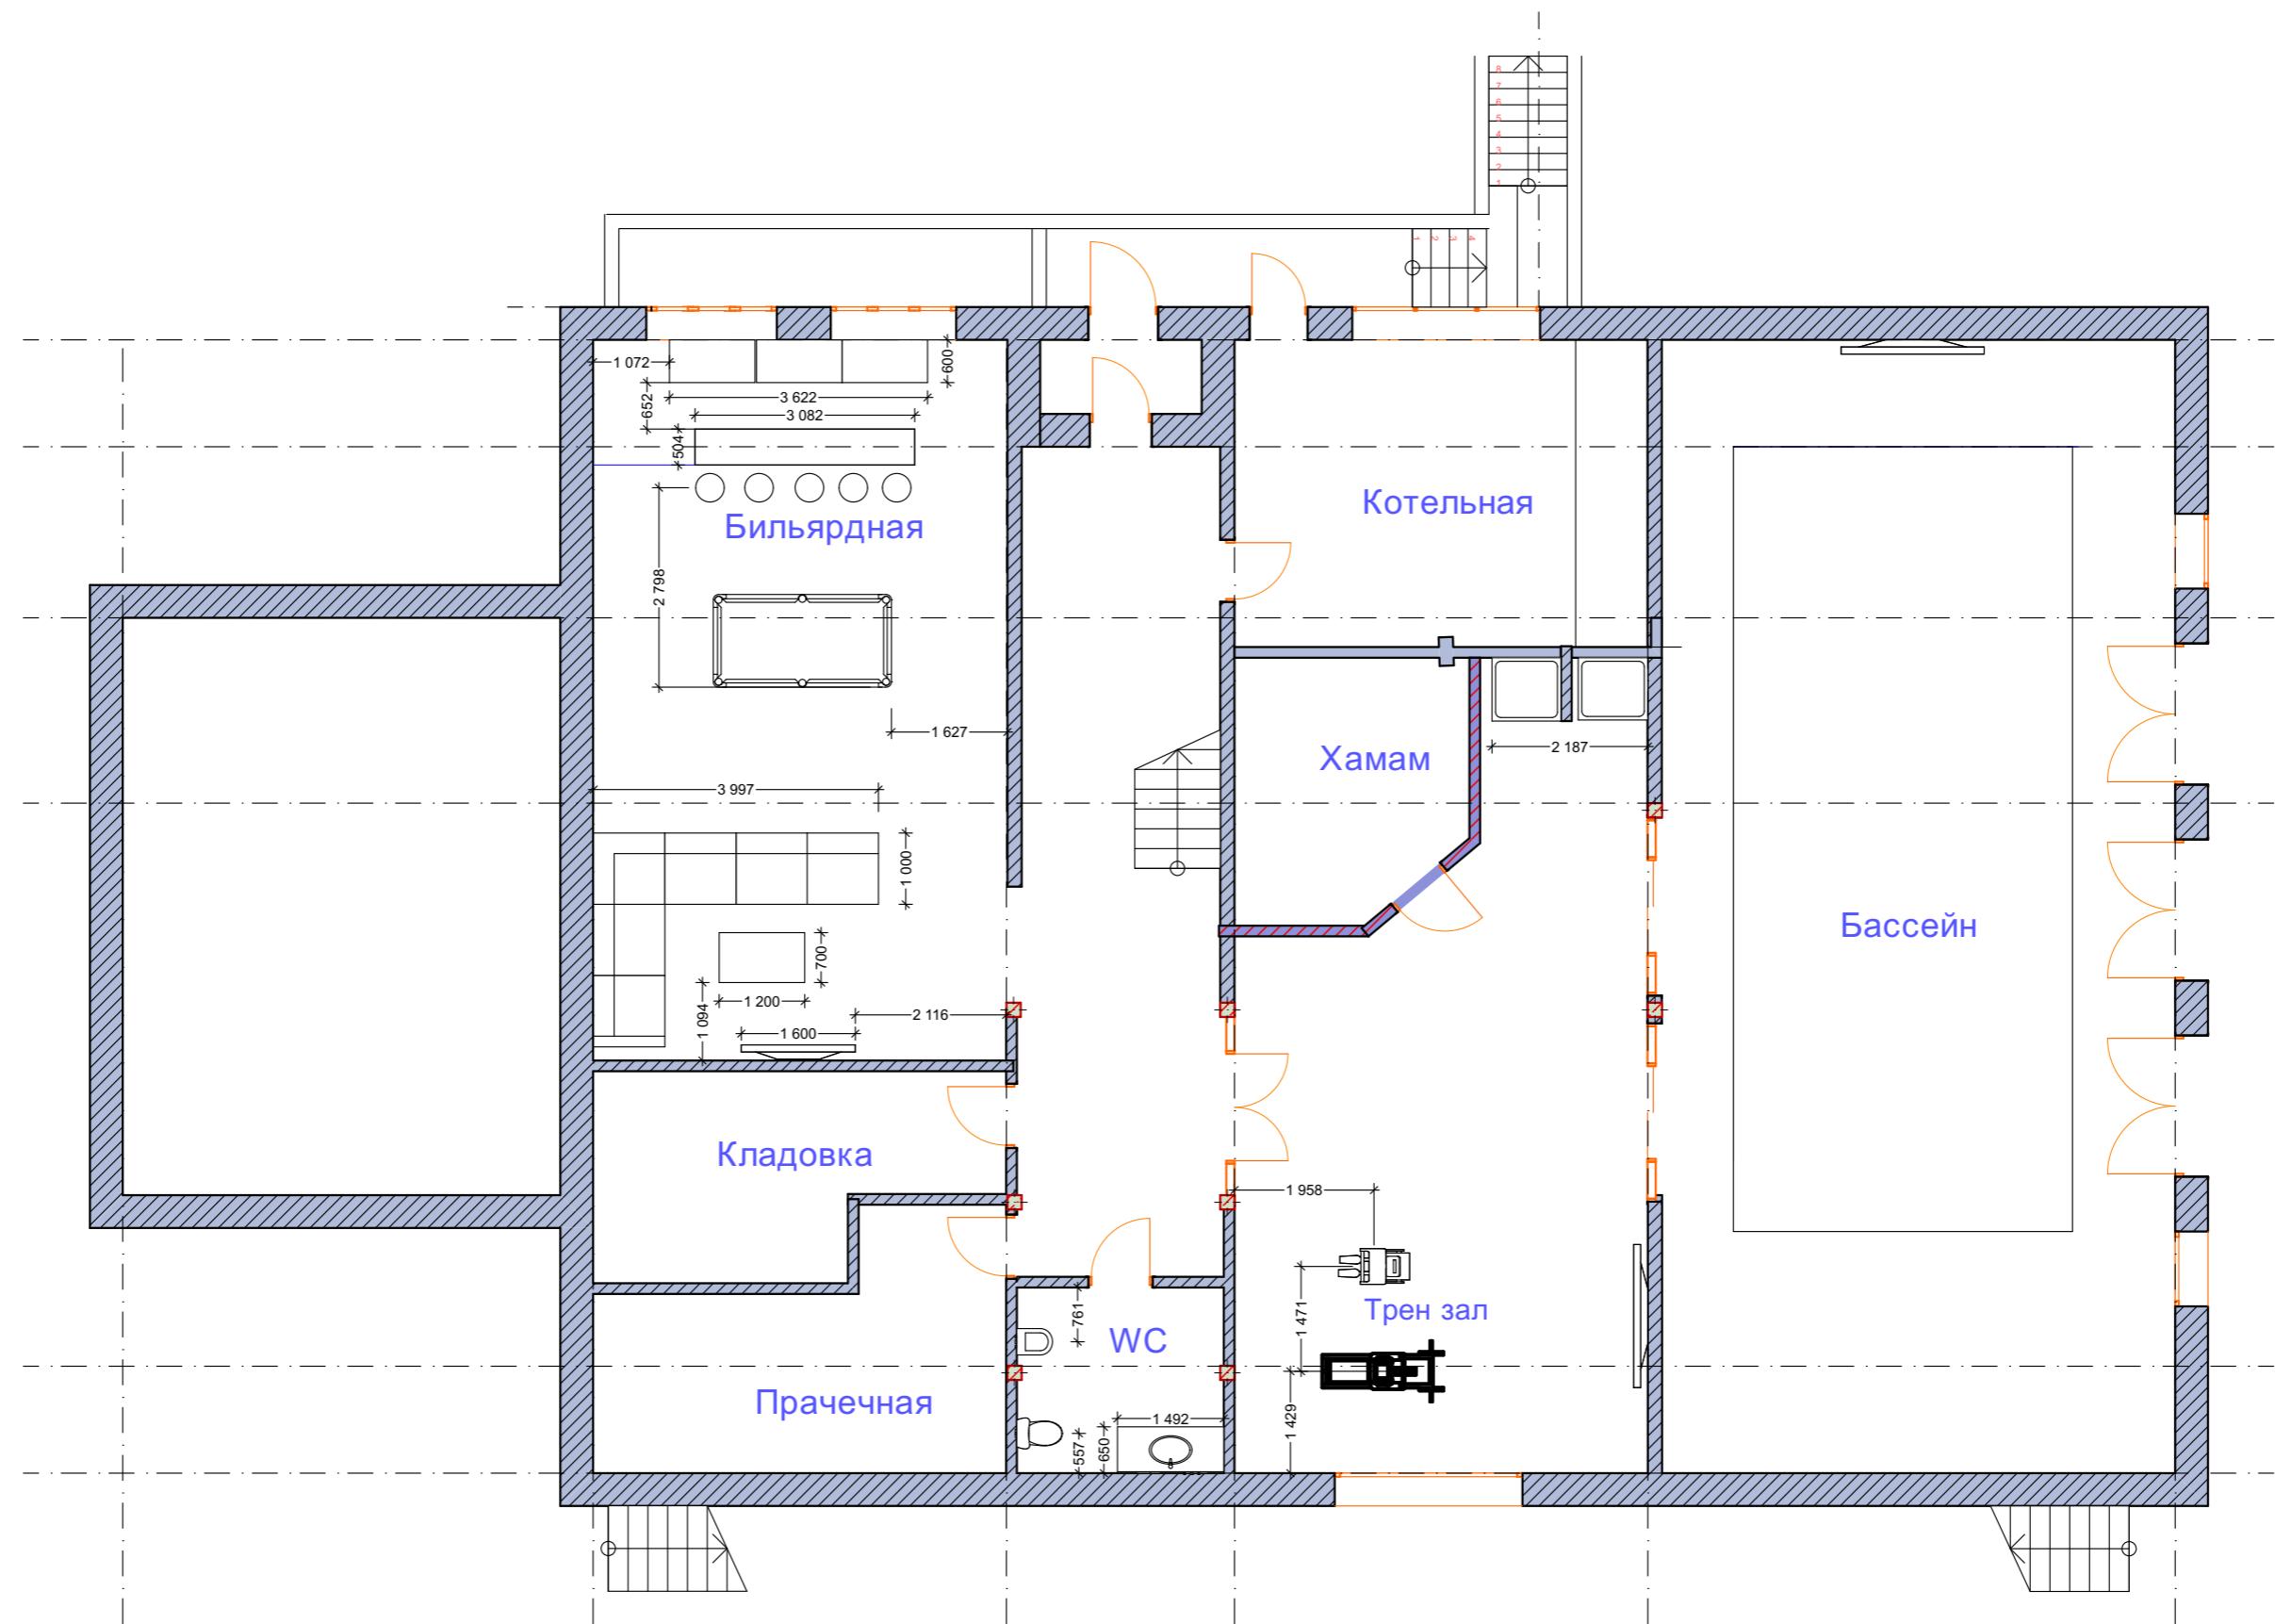

	Частный дом. ЖК МонакоВо!
	Дом у Озера
	Масштаб 1:100
	Дизайнер Т. Астафьев 8 915 360 0663
	Лист 28 из 11

# План расстановки мебели 1-й этаж

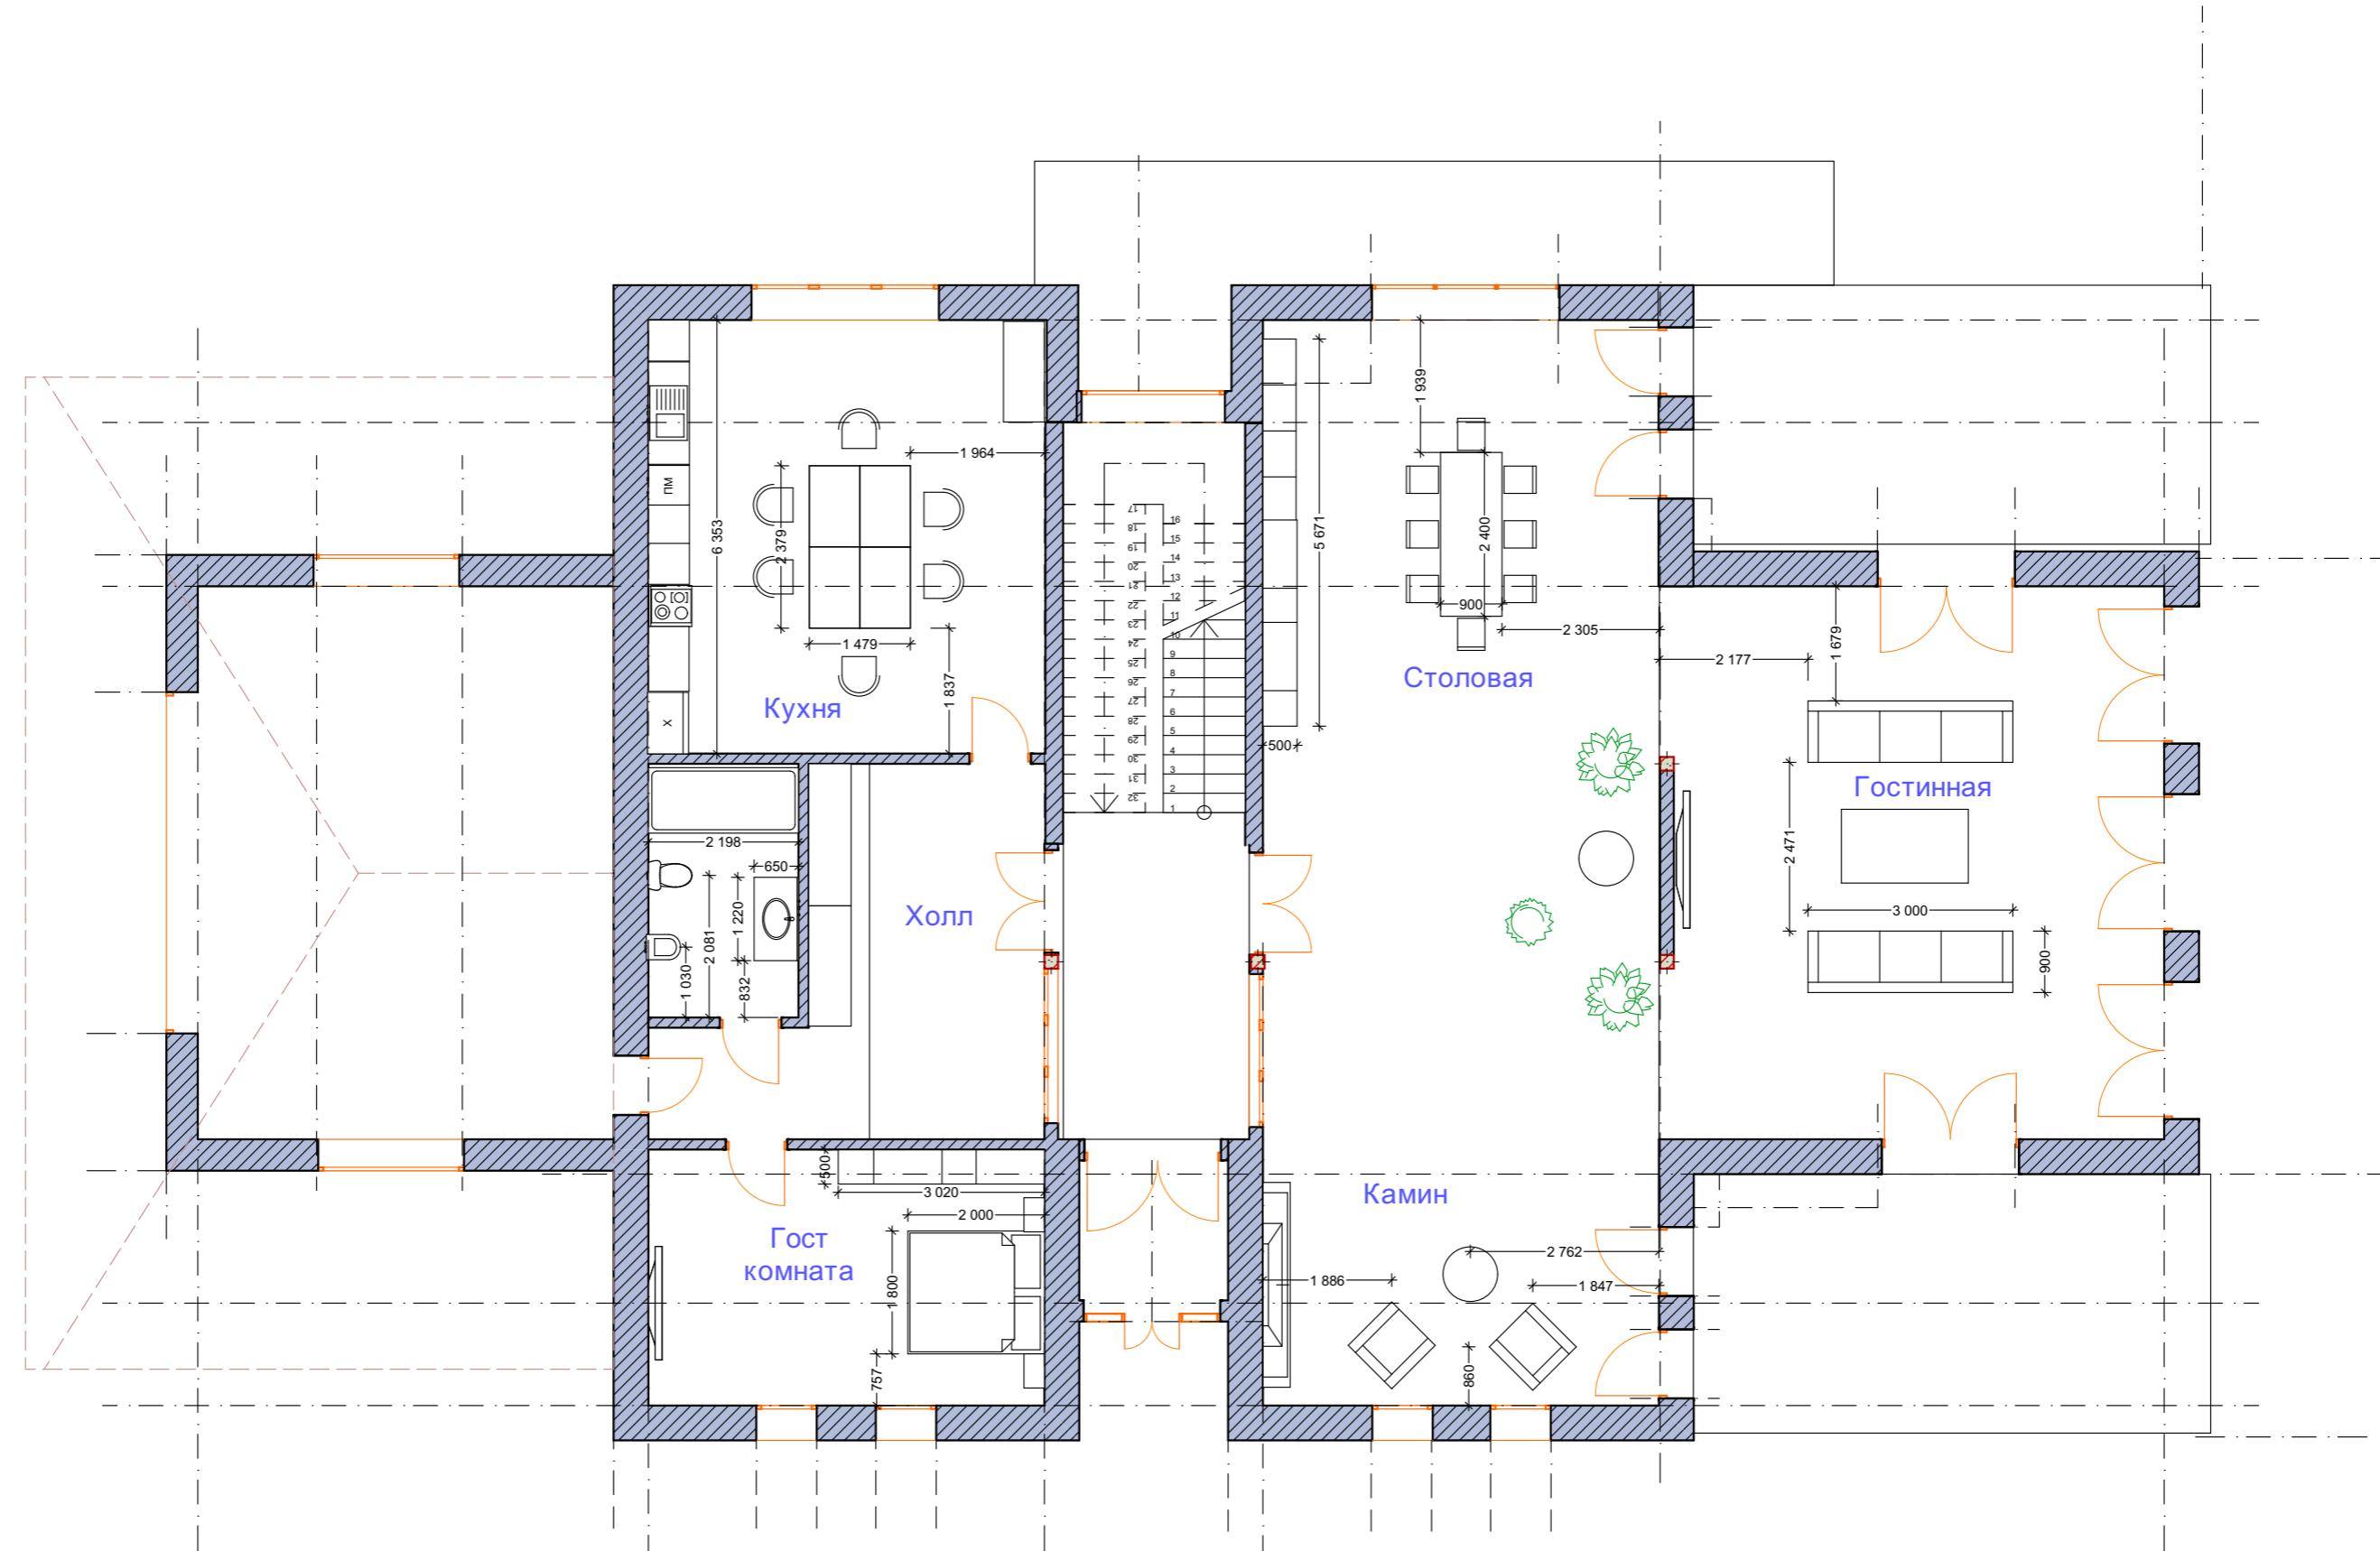

Частный дом. ЖК МонакоВо!


Дом у Озера

Масштаб 1:100

Дизайнер Т. Астафьев 8 915 360 0663


Лист 29 из 11

# План расстановки мебели 2-й этаж

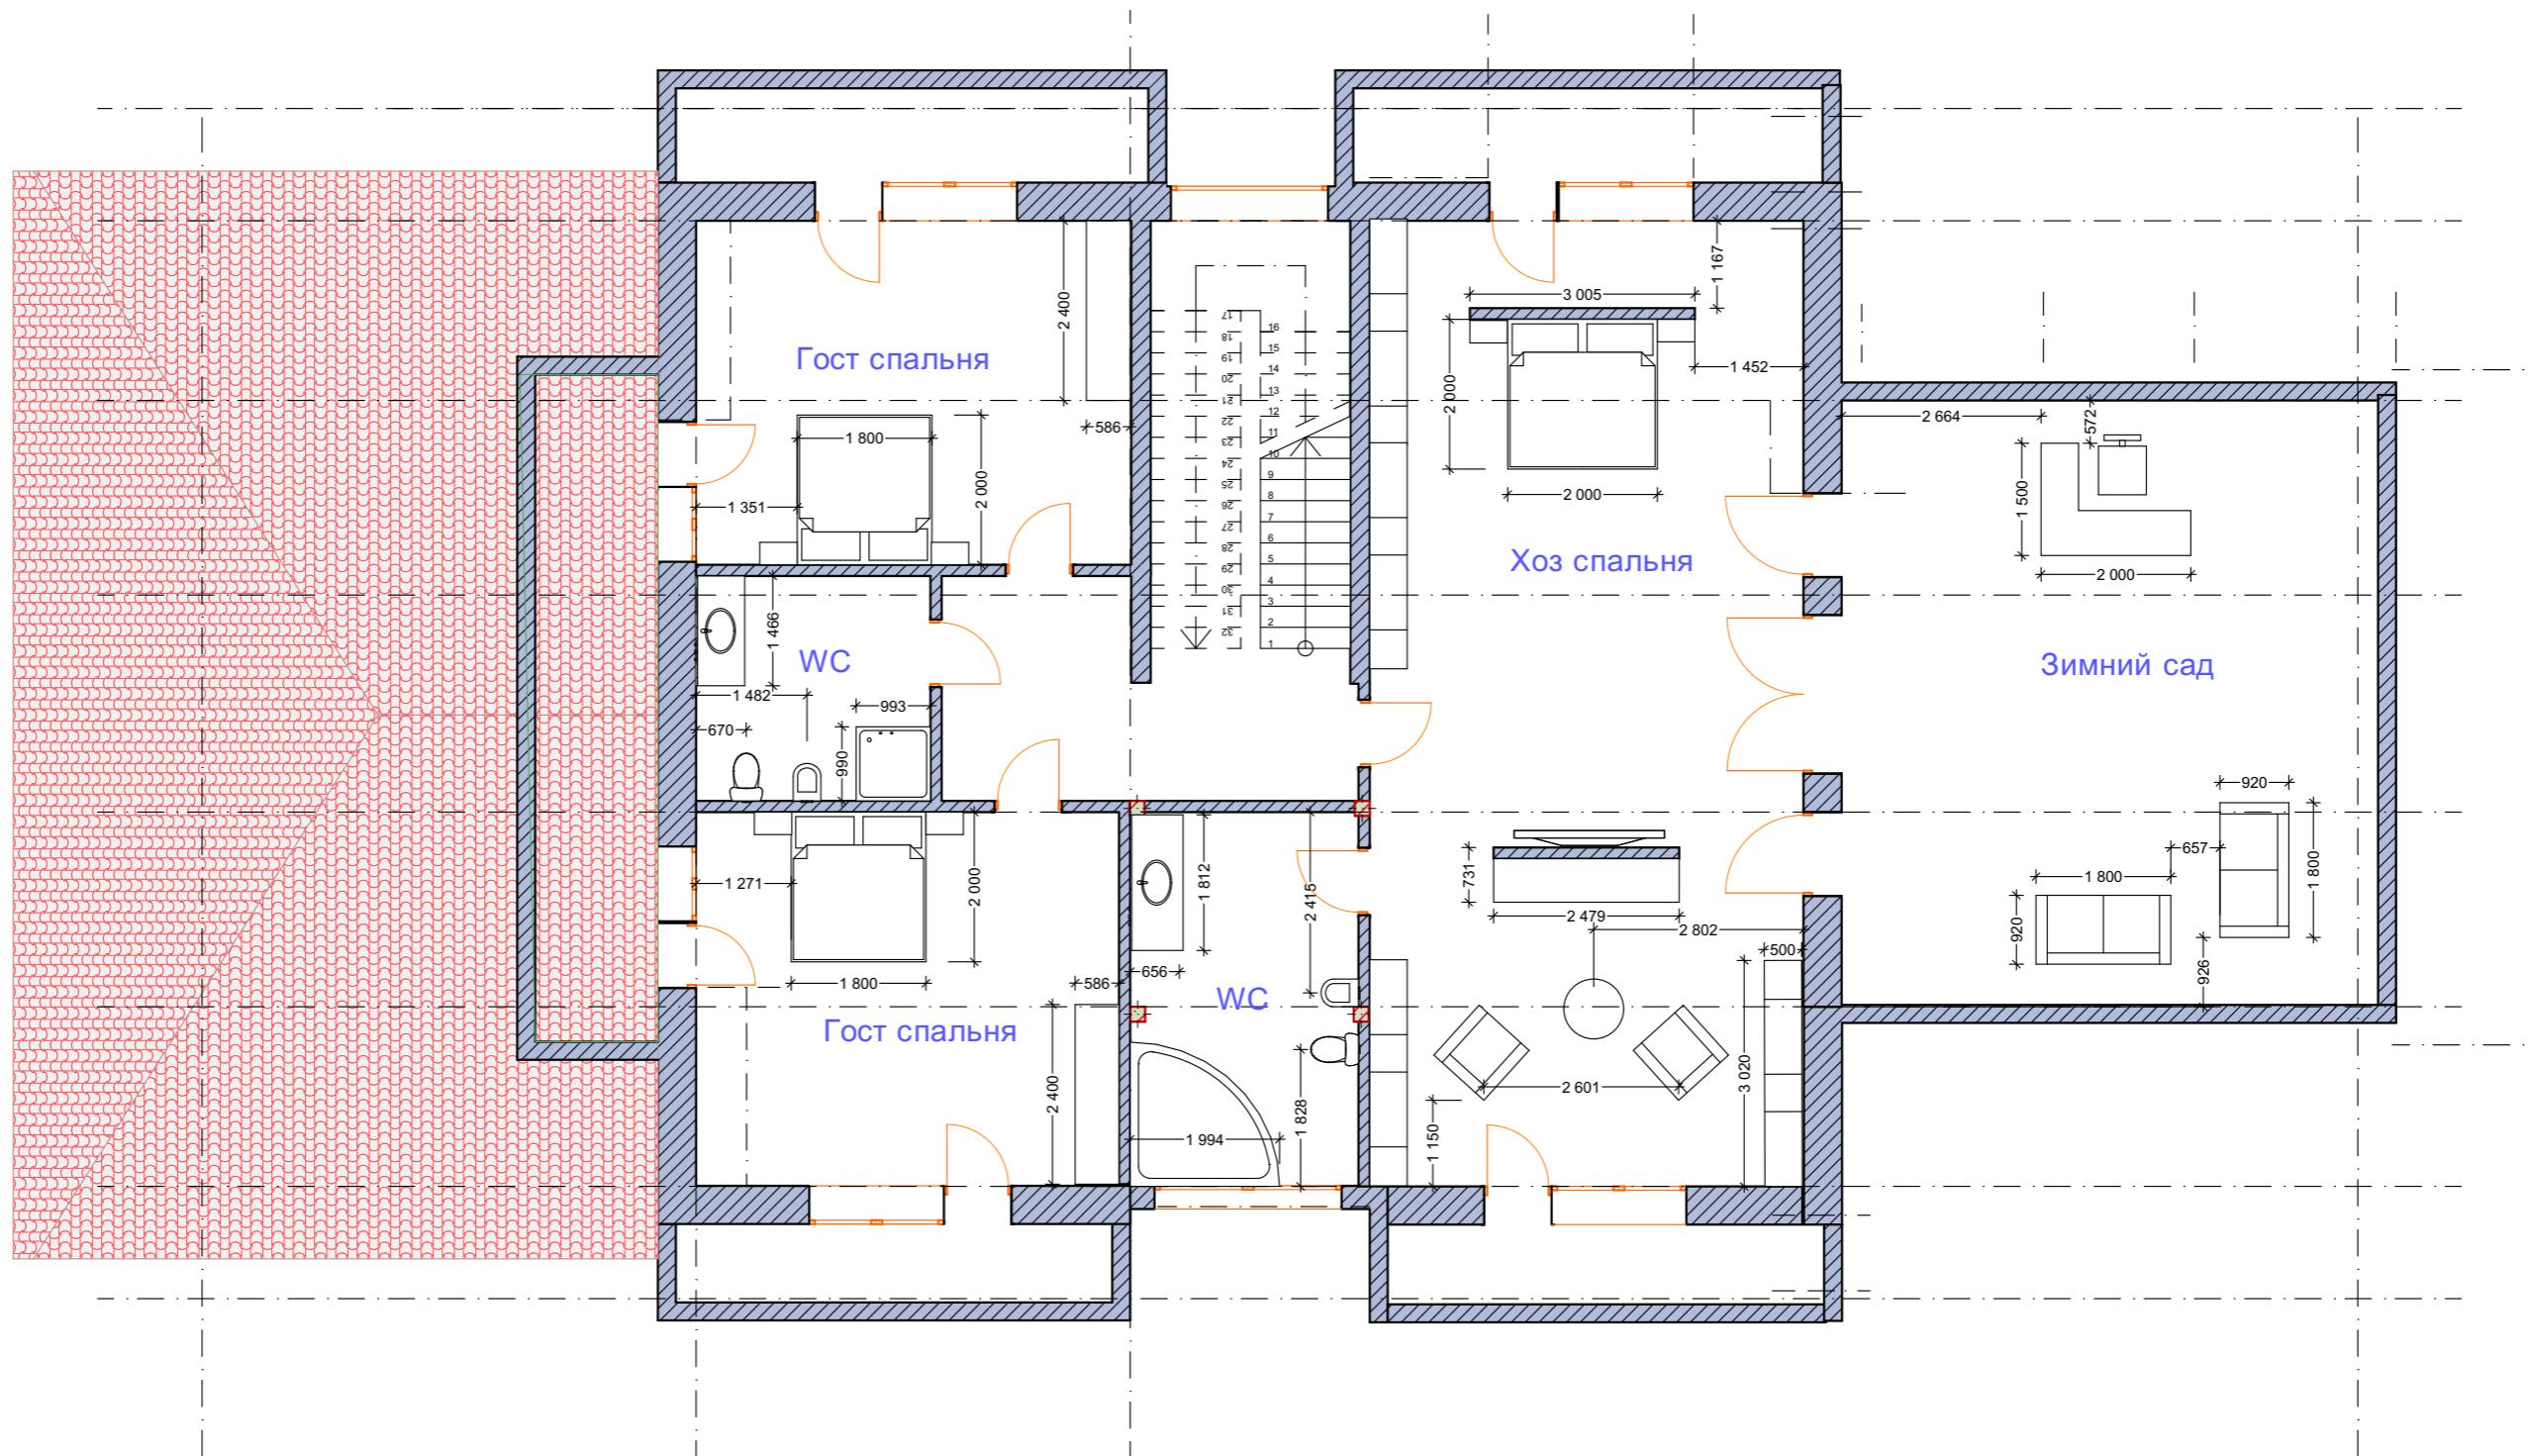


	Частный дом. ЖК МонакоВо!
	Дом у Озера
	Масштаб 1:100
	Дизайнер Т. Астафьев 8 915 360 0663
	Лист 30 из 11

## *Монтажно-демонтажный план цокольный этаж*

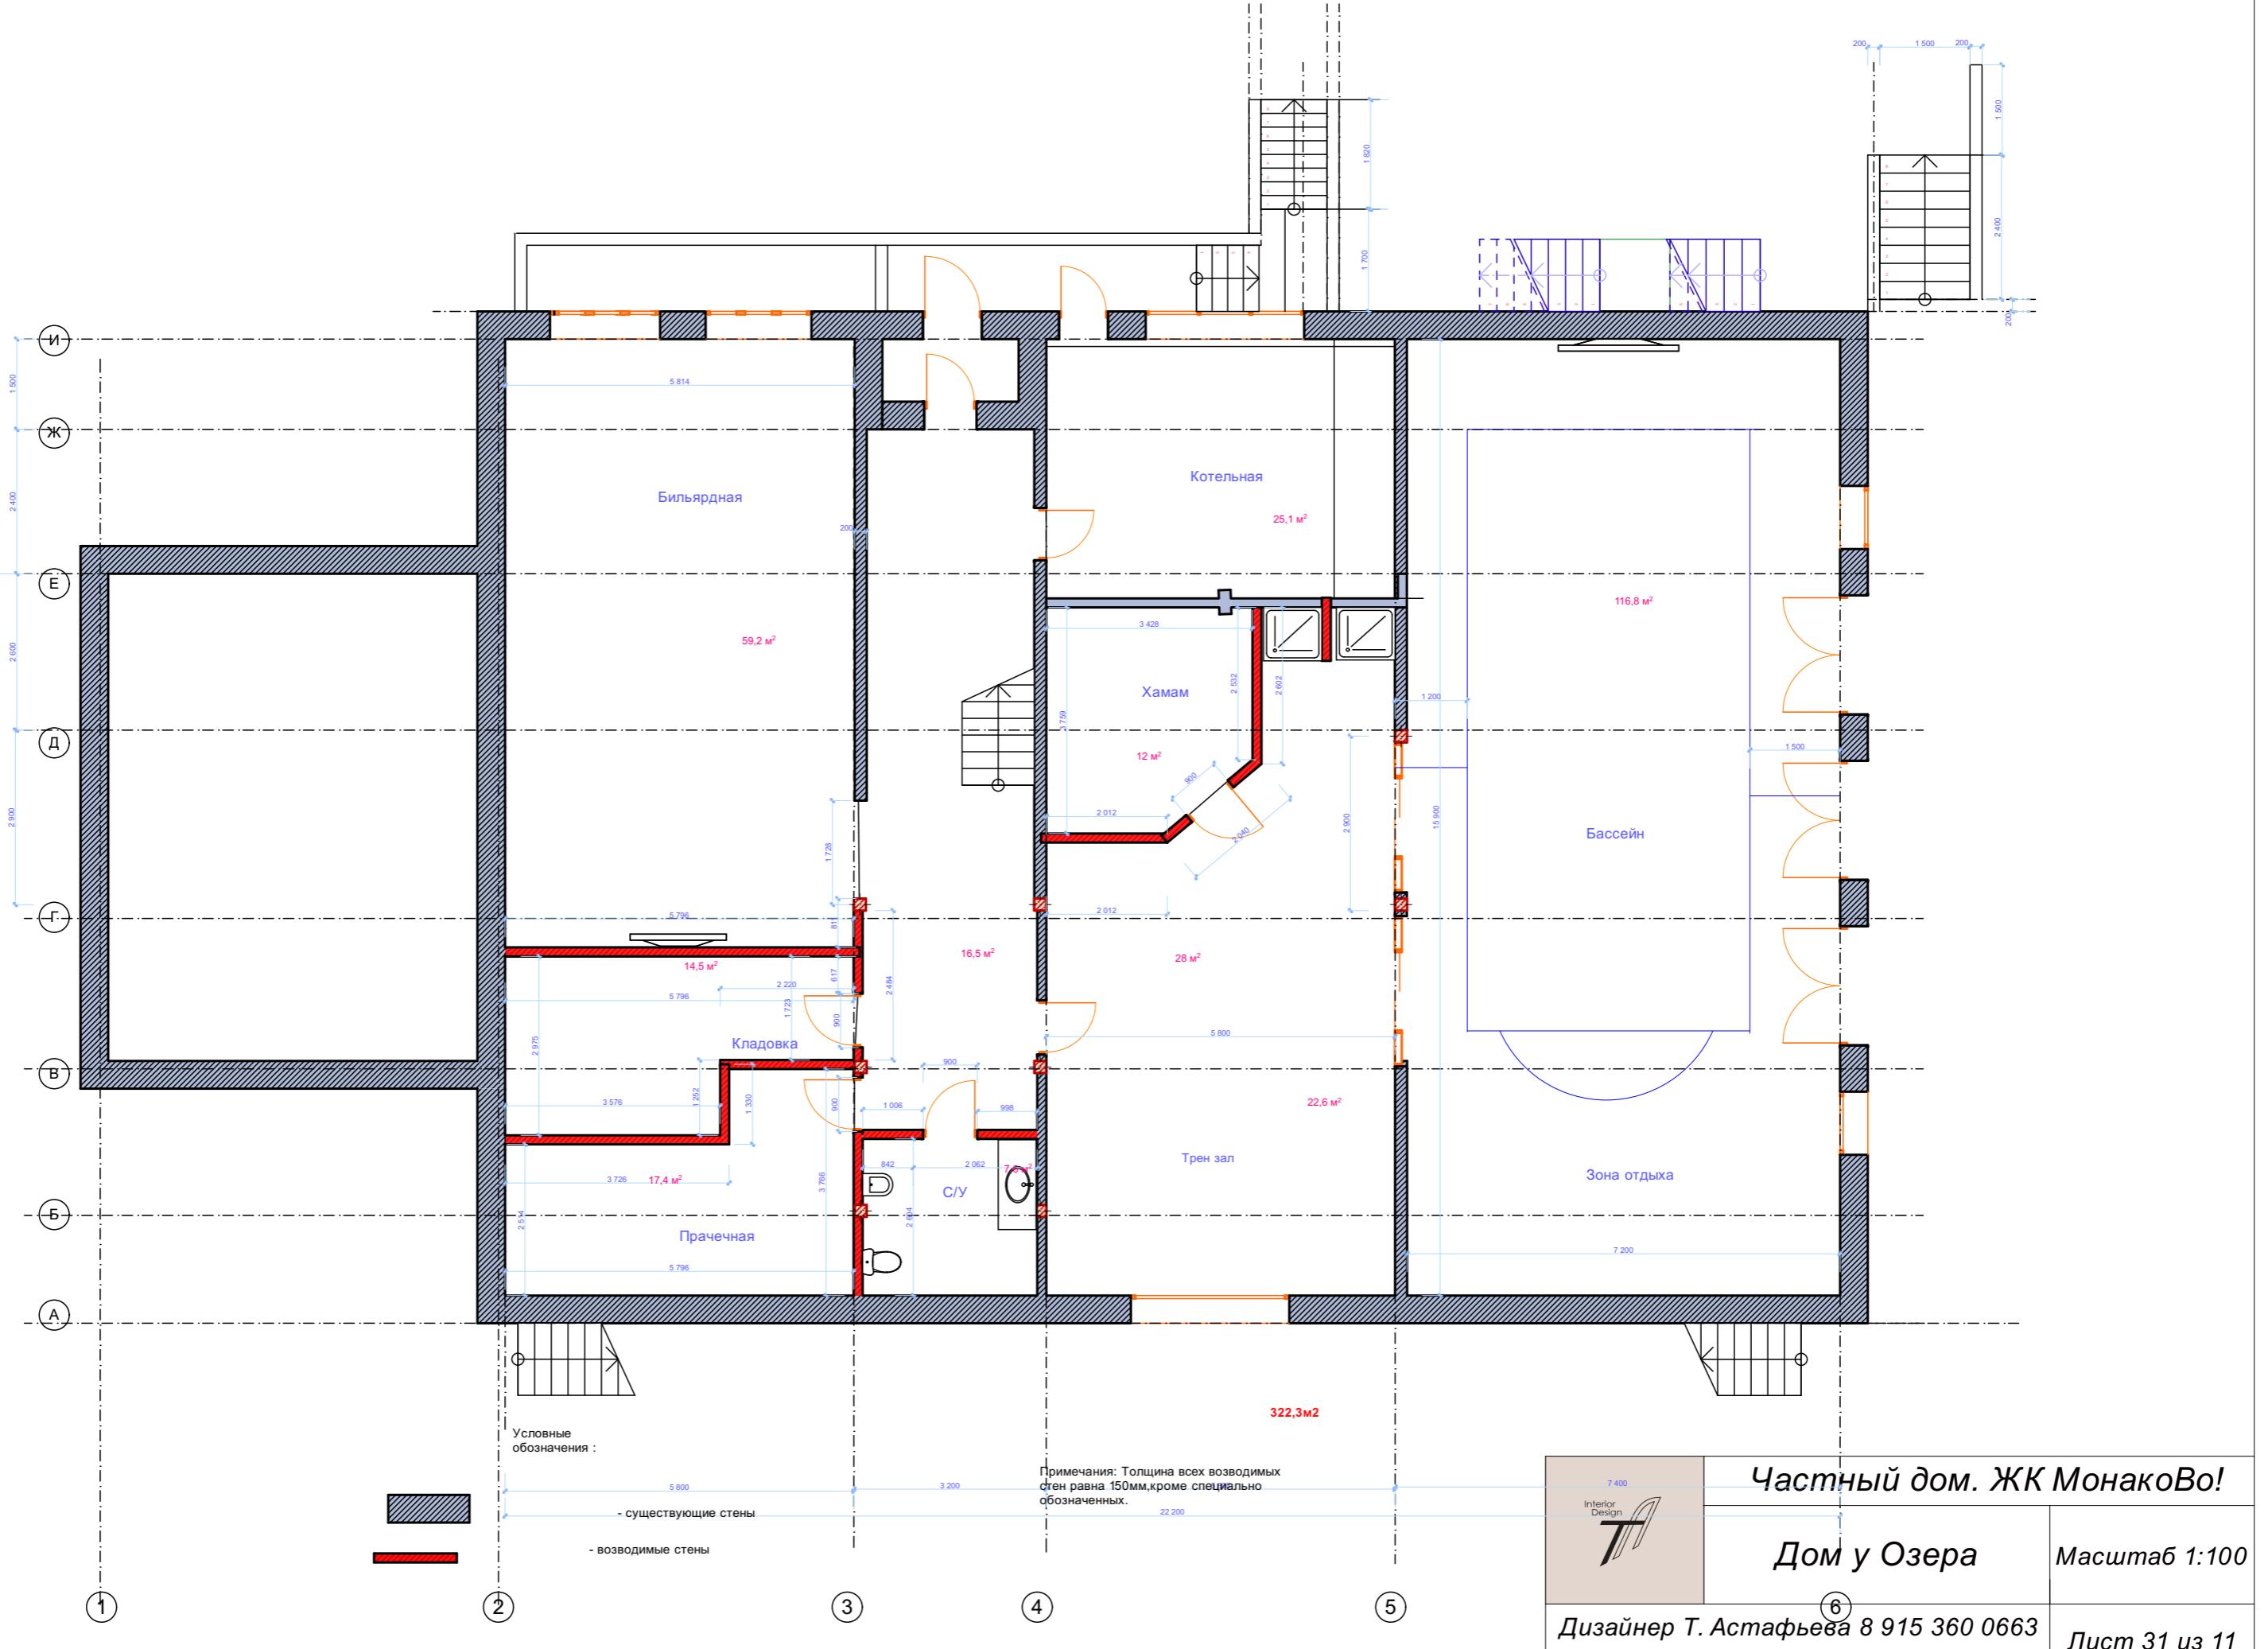


# Монтажно-демонтажный план 1-й этаж

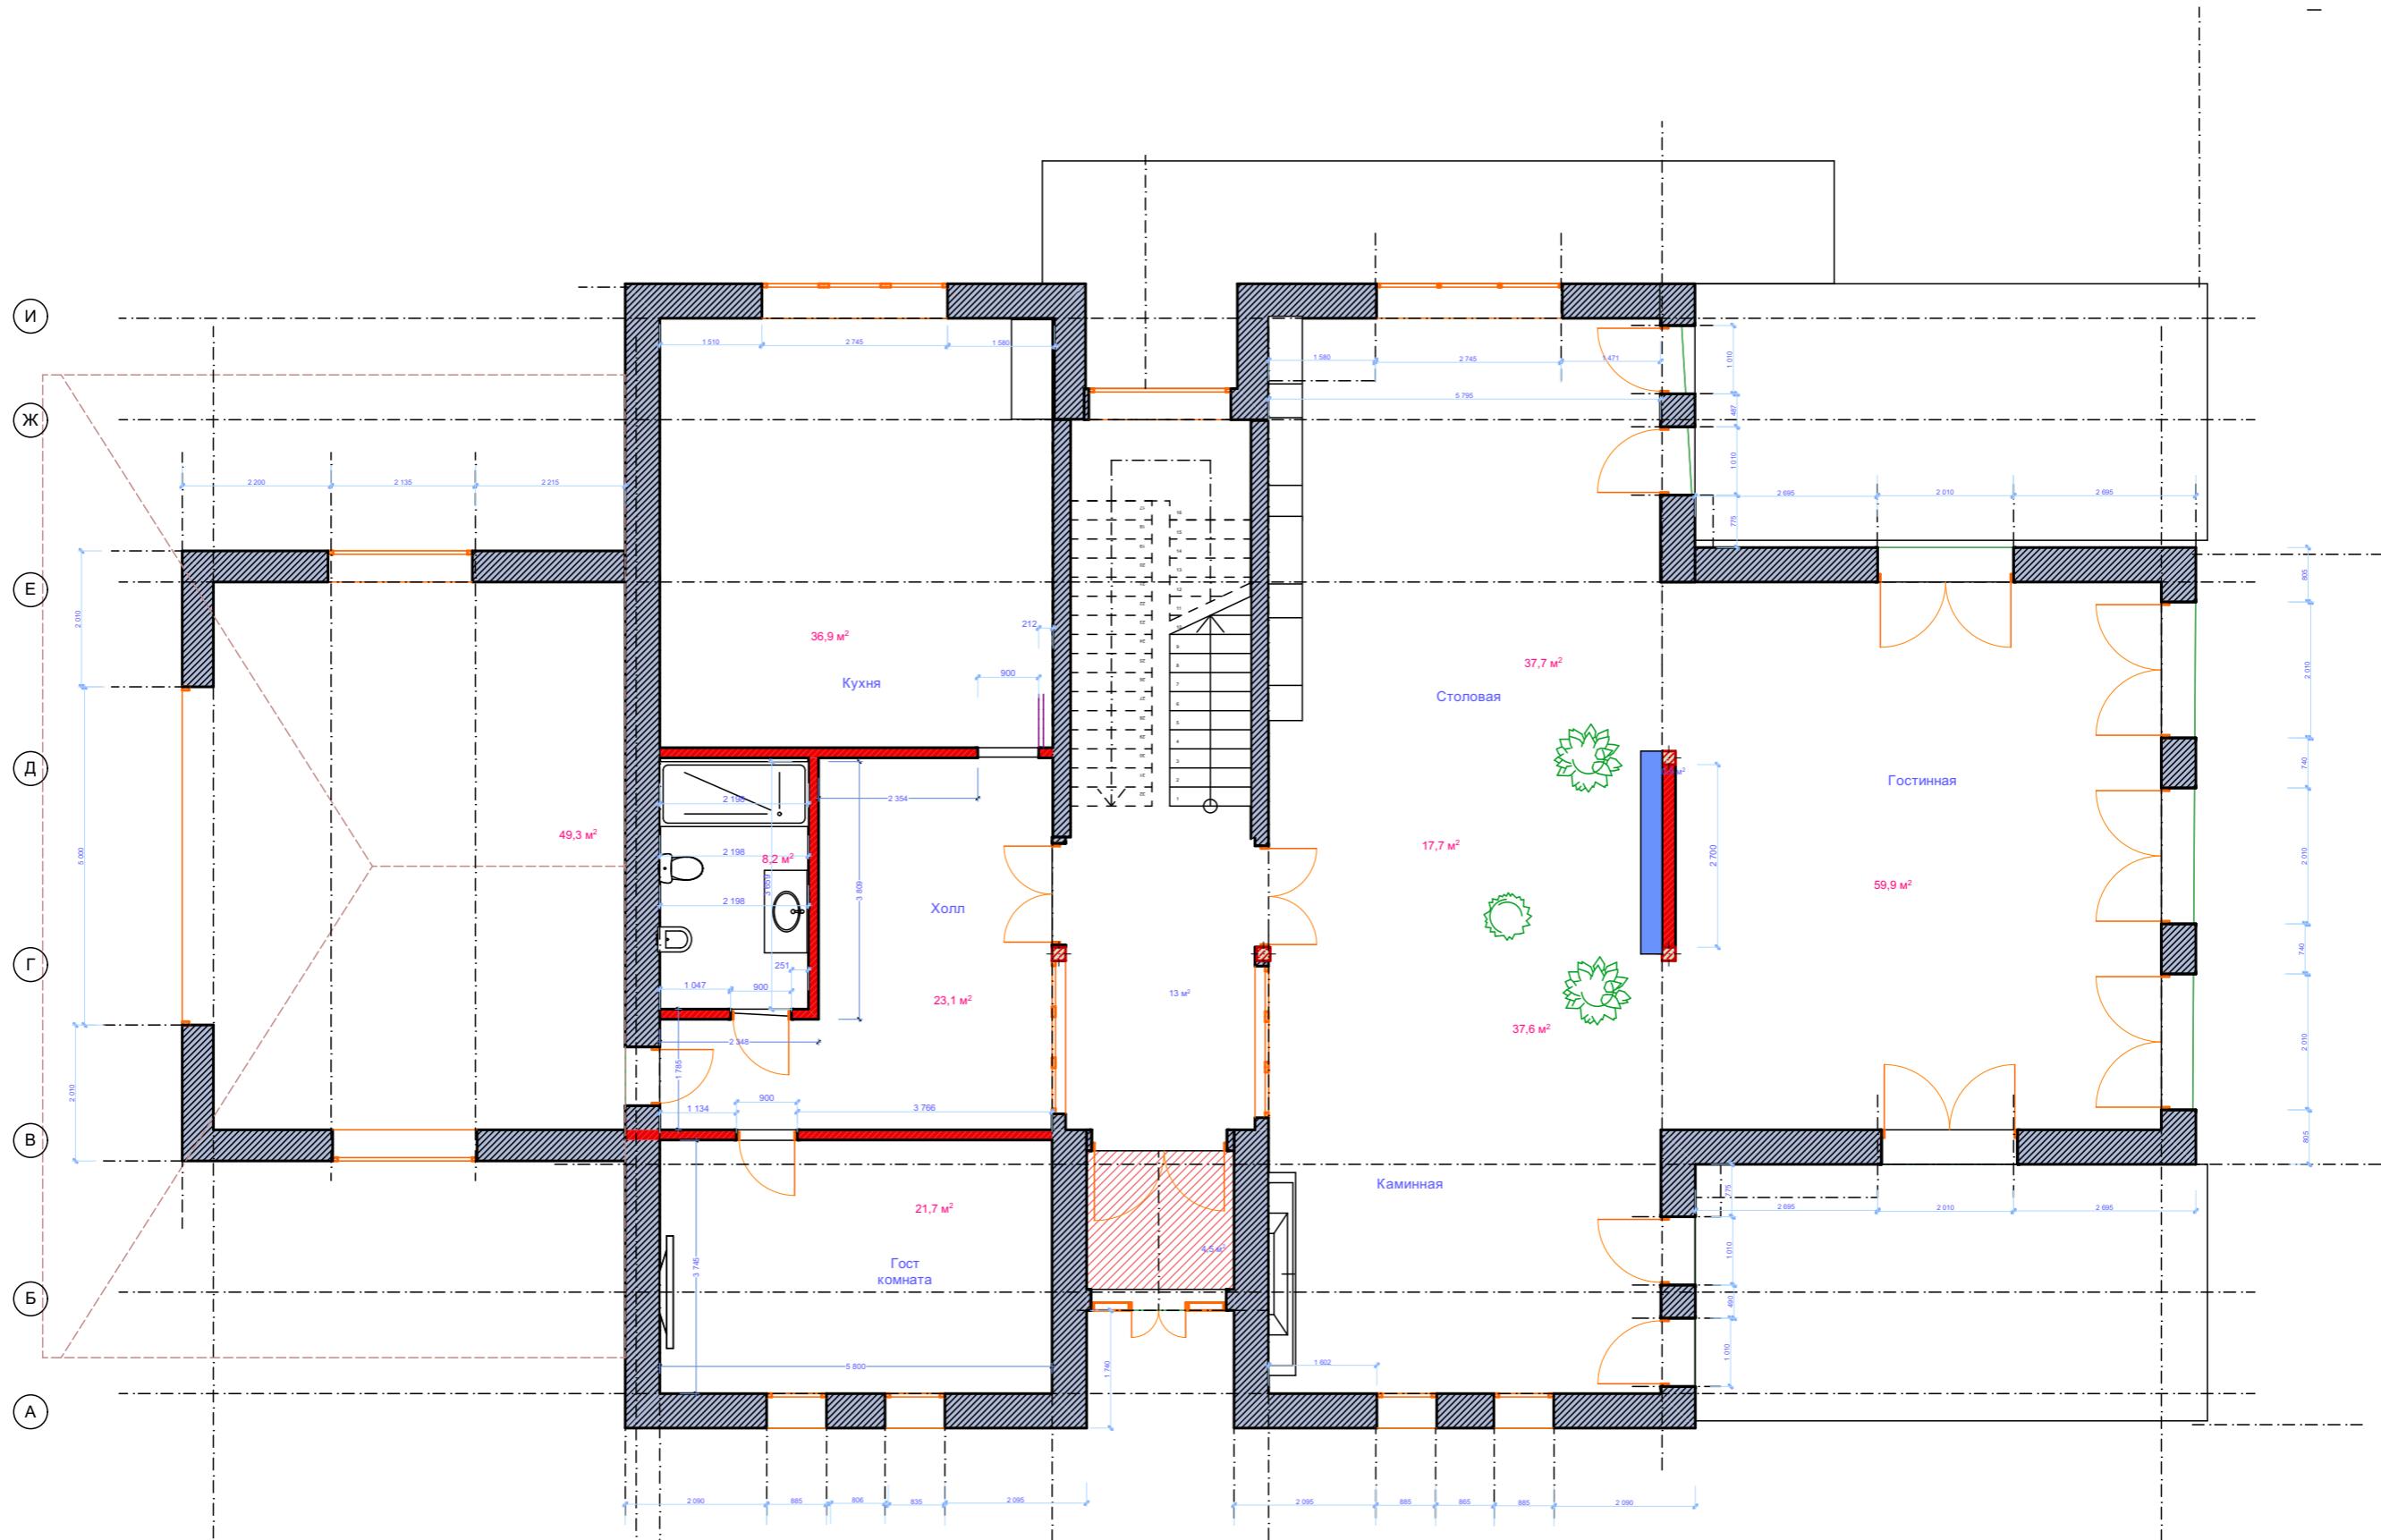

	<b>Частный дом. ЖК МонакоВо!</b>
	<b>Дом у Озера</b>
	Масштаб 1:100
	Дизайнер Т. Астафьев 8 915 360 0663

## **Монтажно-демонтажный план 2-й этаж**

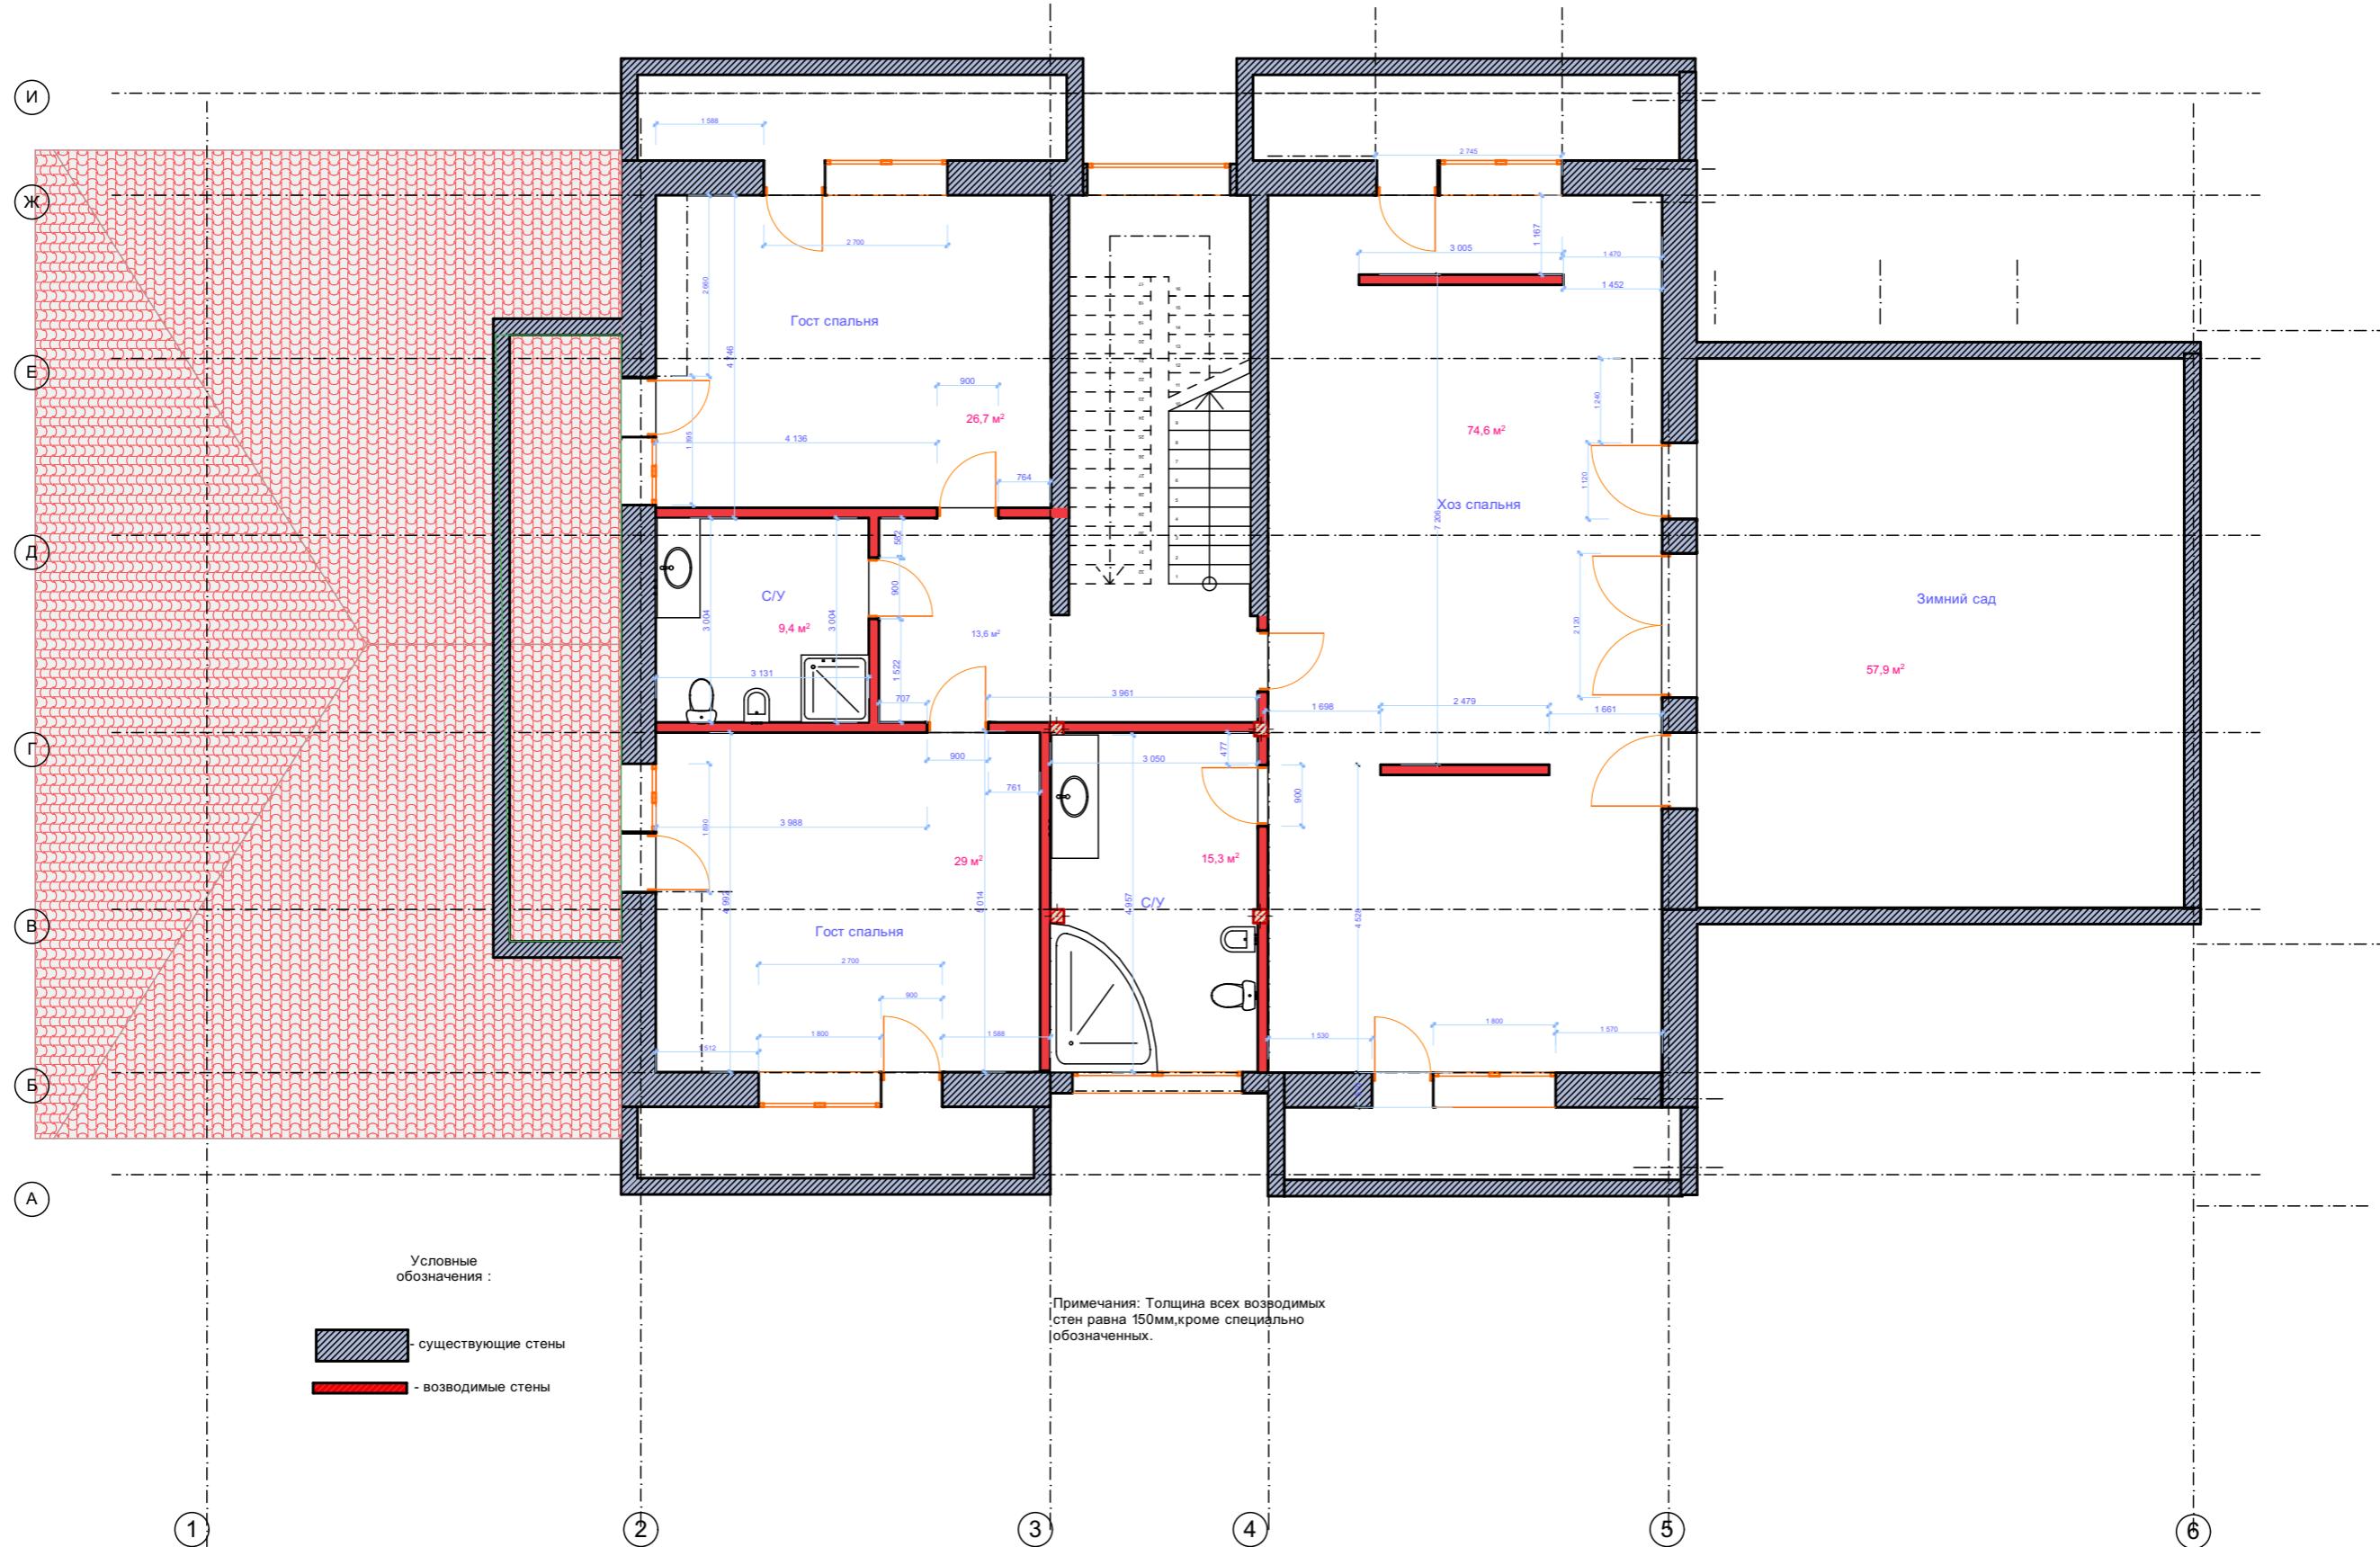

Частный дом. ЖК МонакоВо!


Дом у Озера

Масштаб 1:100

Дизайнер Т. Астафьева 8 915 360 0663

Лист 33 из 11

# План полов цокольный этаж

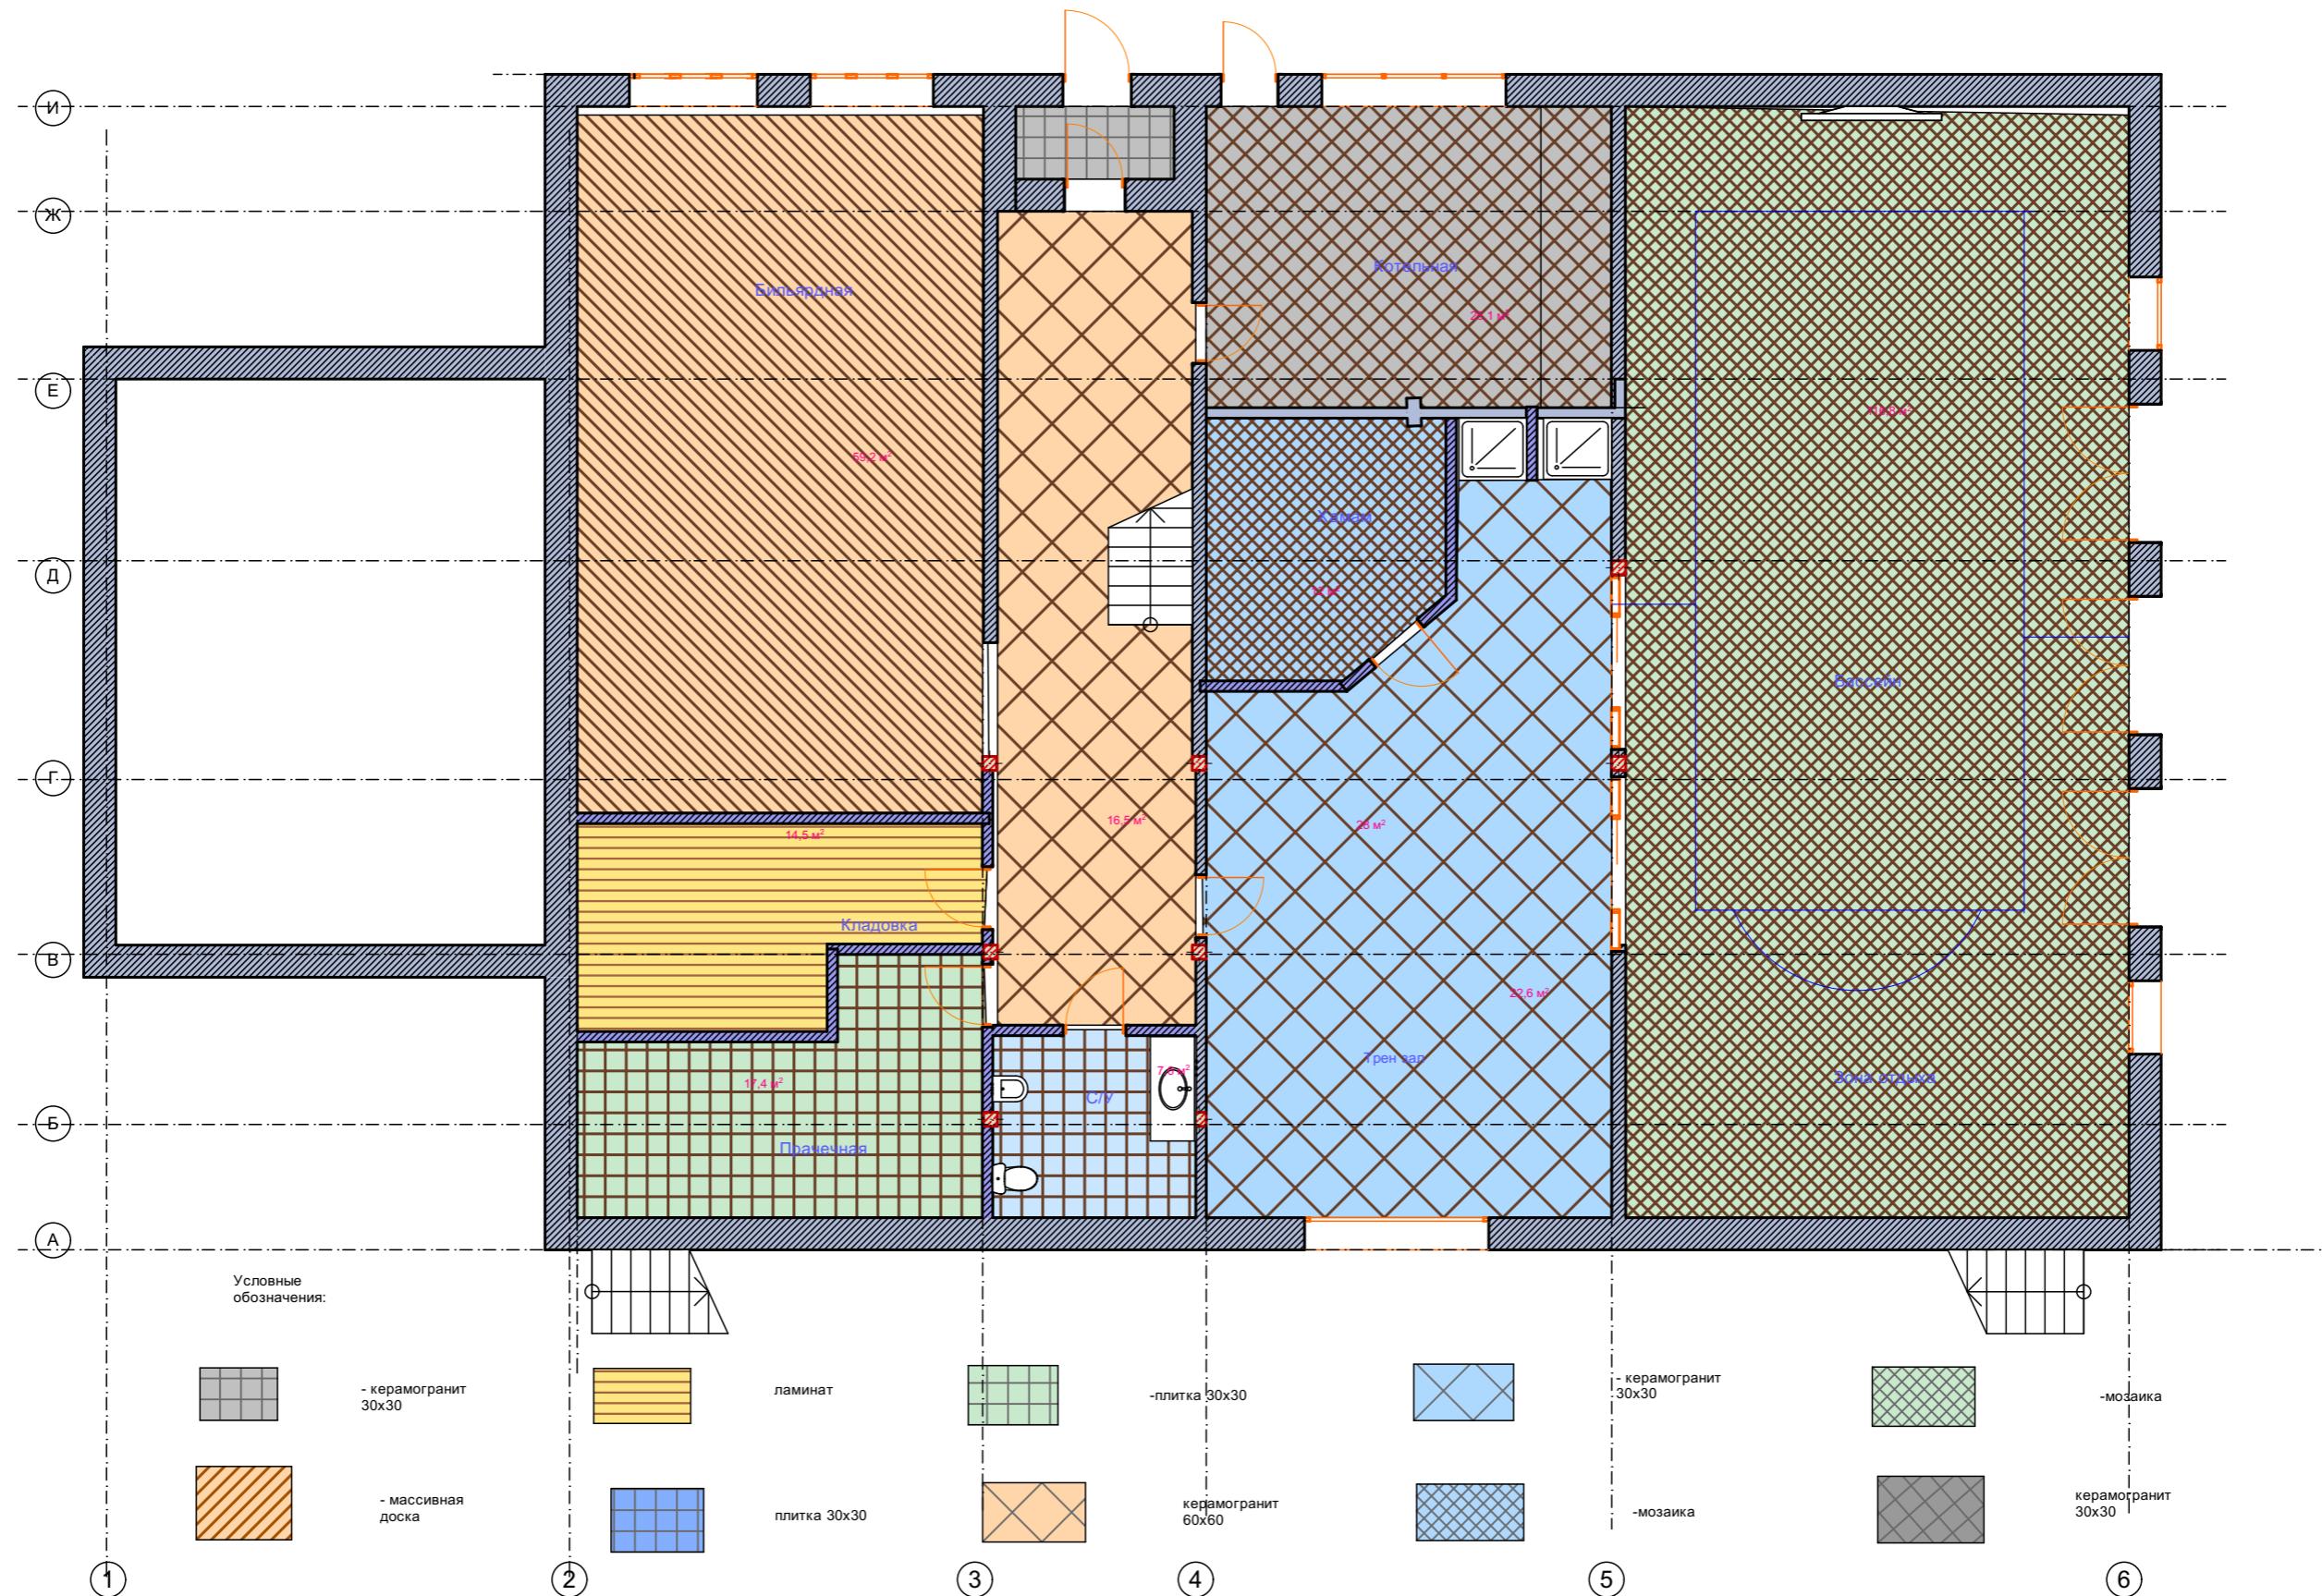

Частный дом. ЖК МонакоВо!


Дом у Озера

Масштаб 1:100

Дизайнер Т. Астафьев 8 915 360 0663

Лист 34 из 11

# План полов 1-й этаж

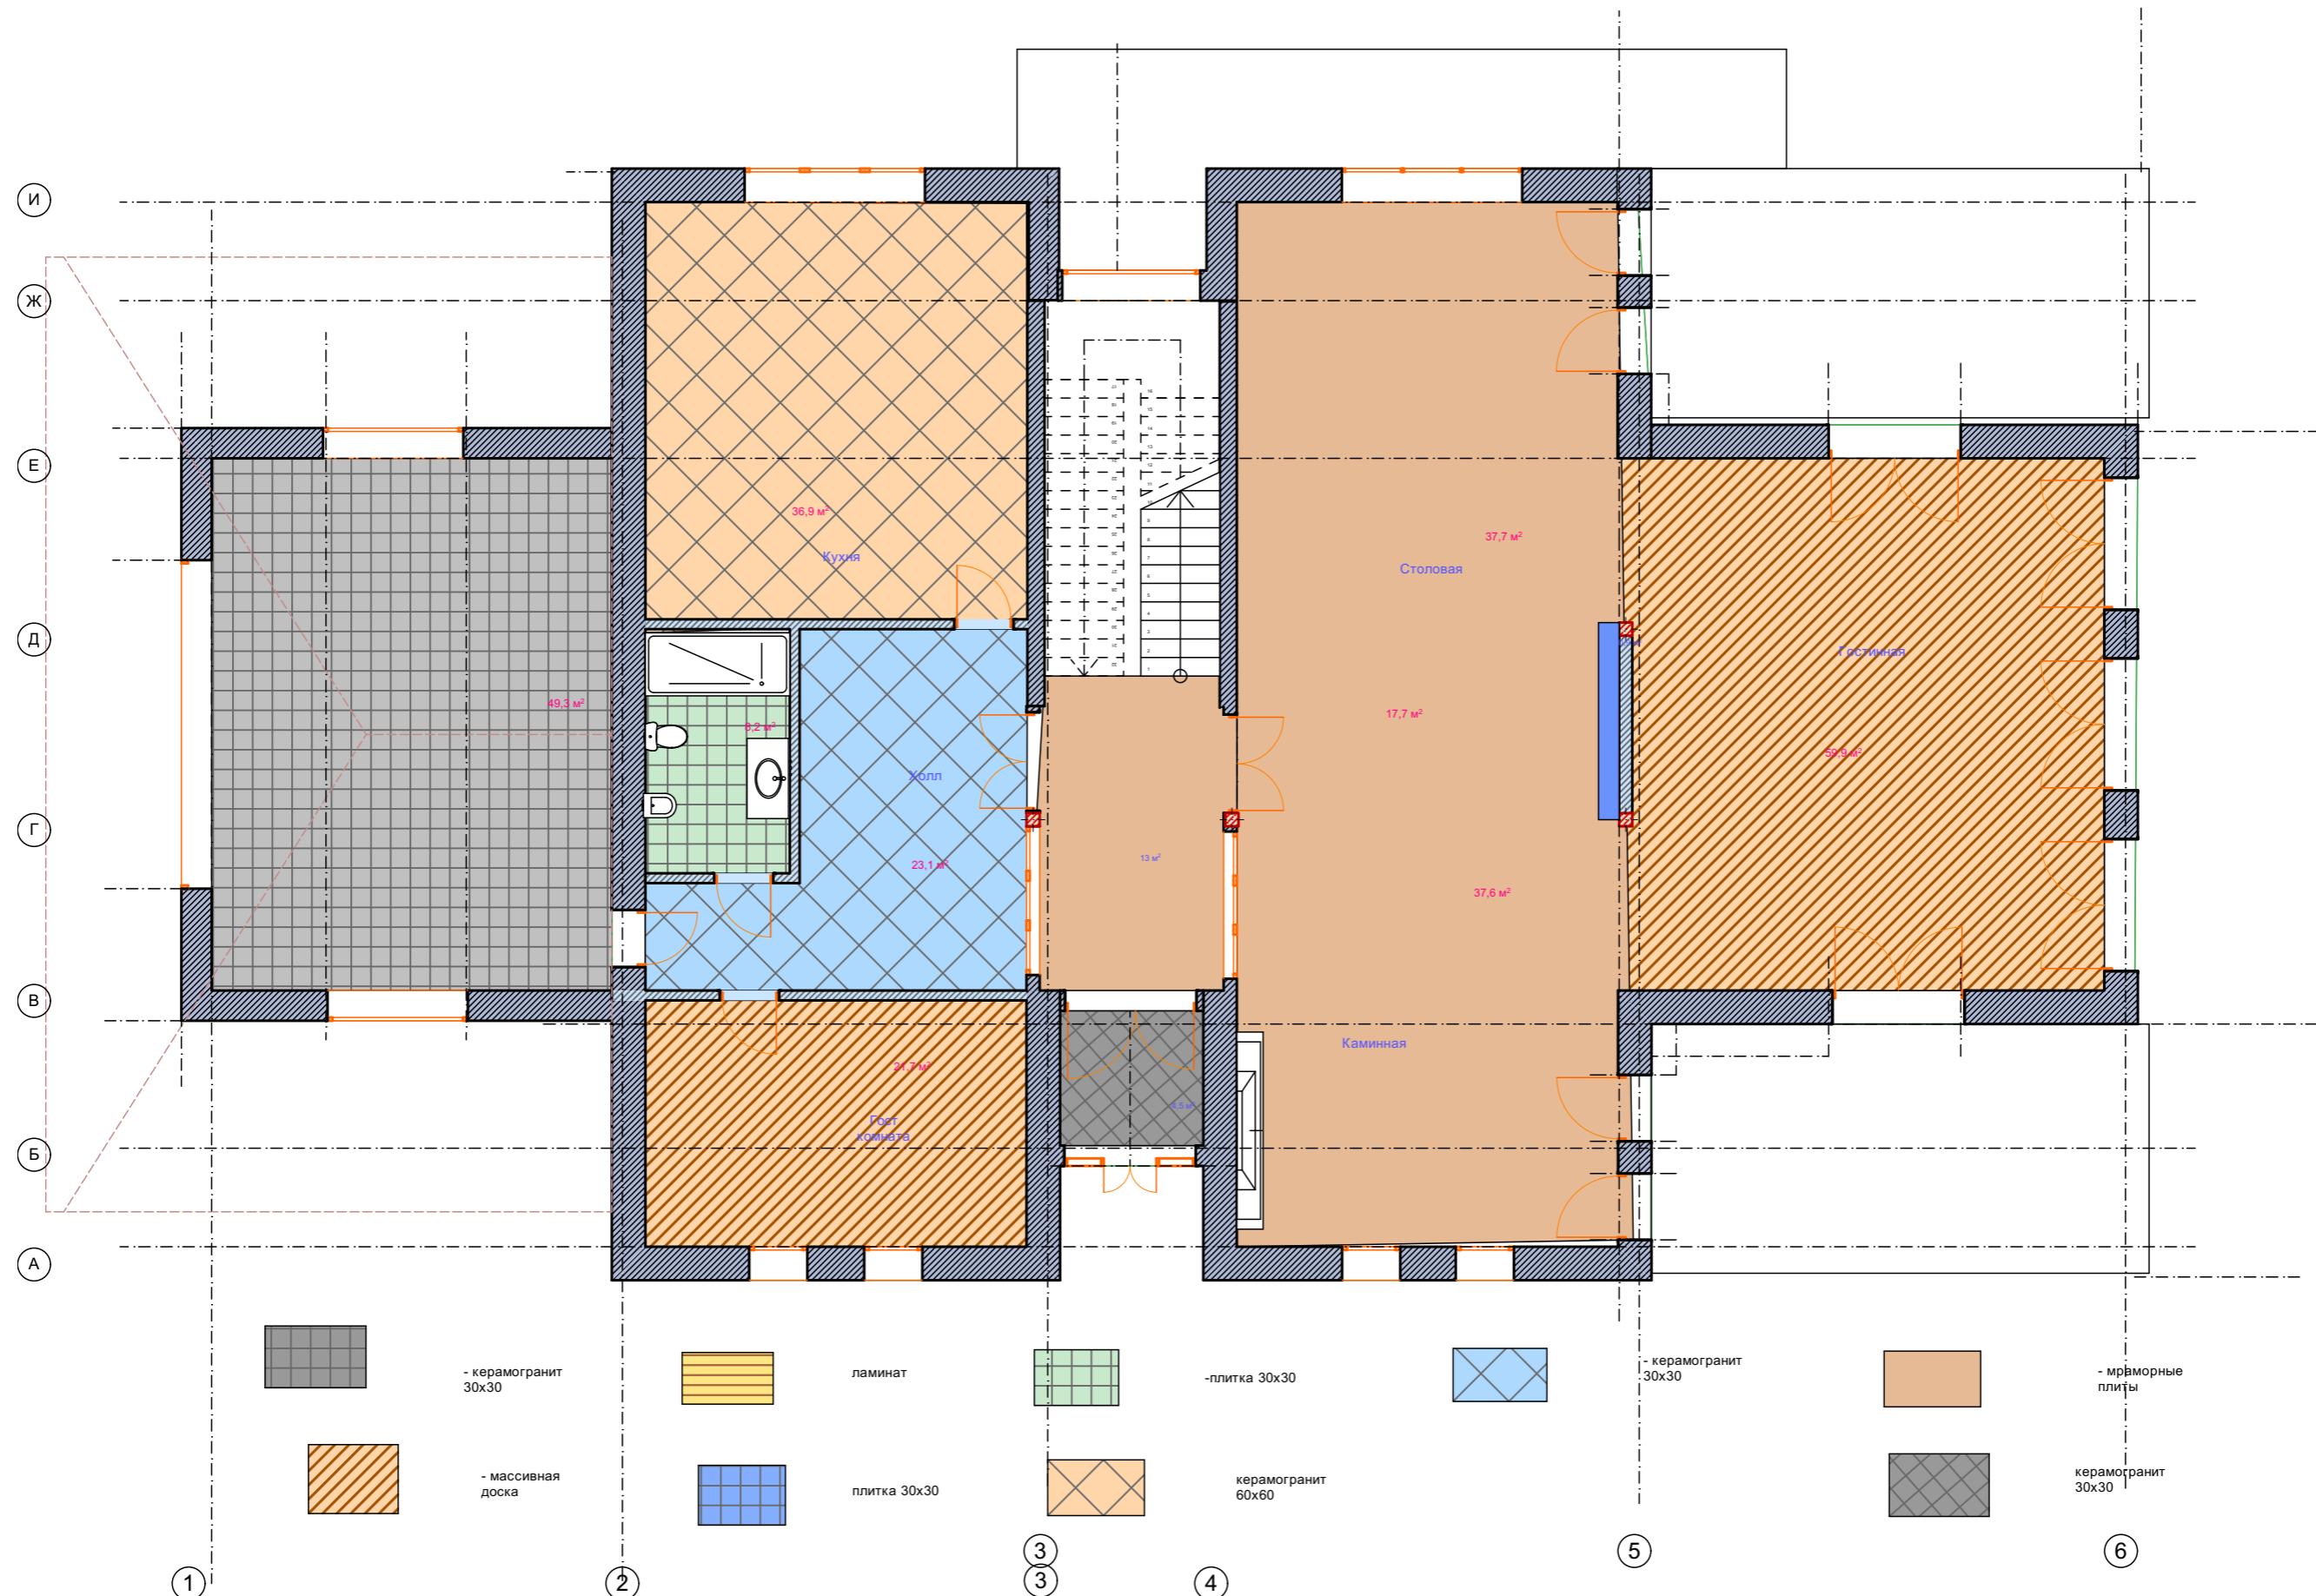

	Частный дом. ЖК МонакоВо!
	Дом у Озера
	Масштаб 1:100
	Дизайнер Т. Астафьев 8 915 360 0663

## План полов 2-й этаж



Частный дом. ЖК МонакоВо!




Дом у Озера

Масштаб 1:100

Дизайнер Т. Астафьев 8 915 360 0663


Лист 36 из 11

# Схема сантехники цокольный этаж

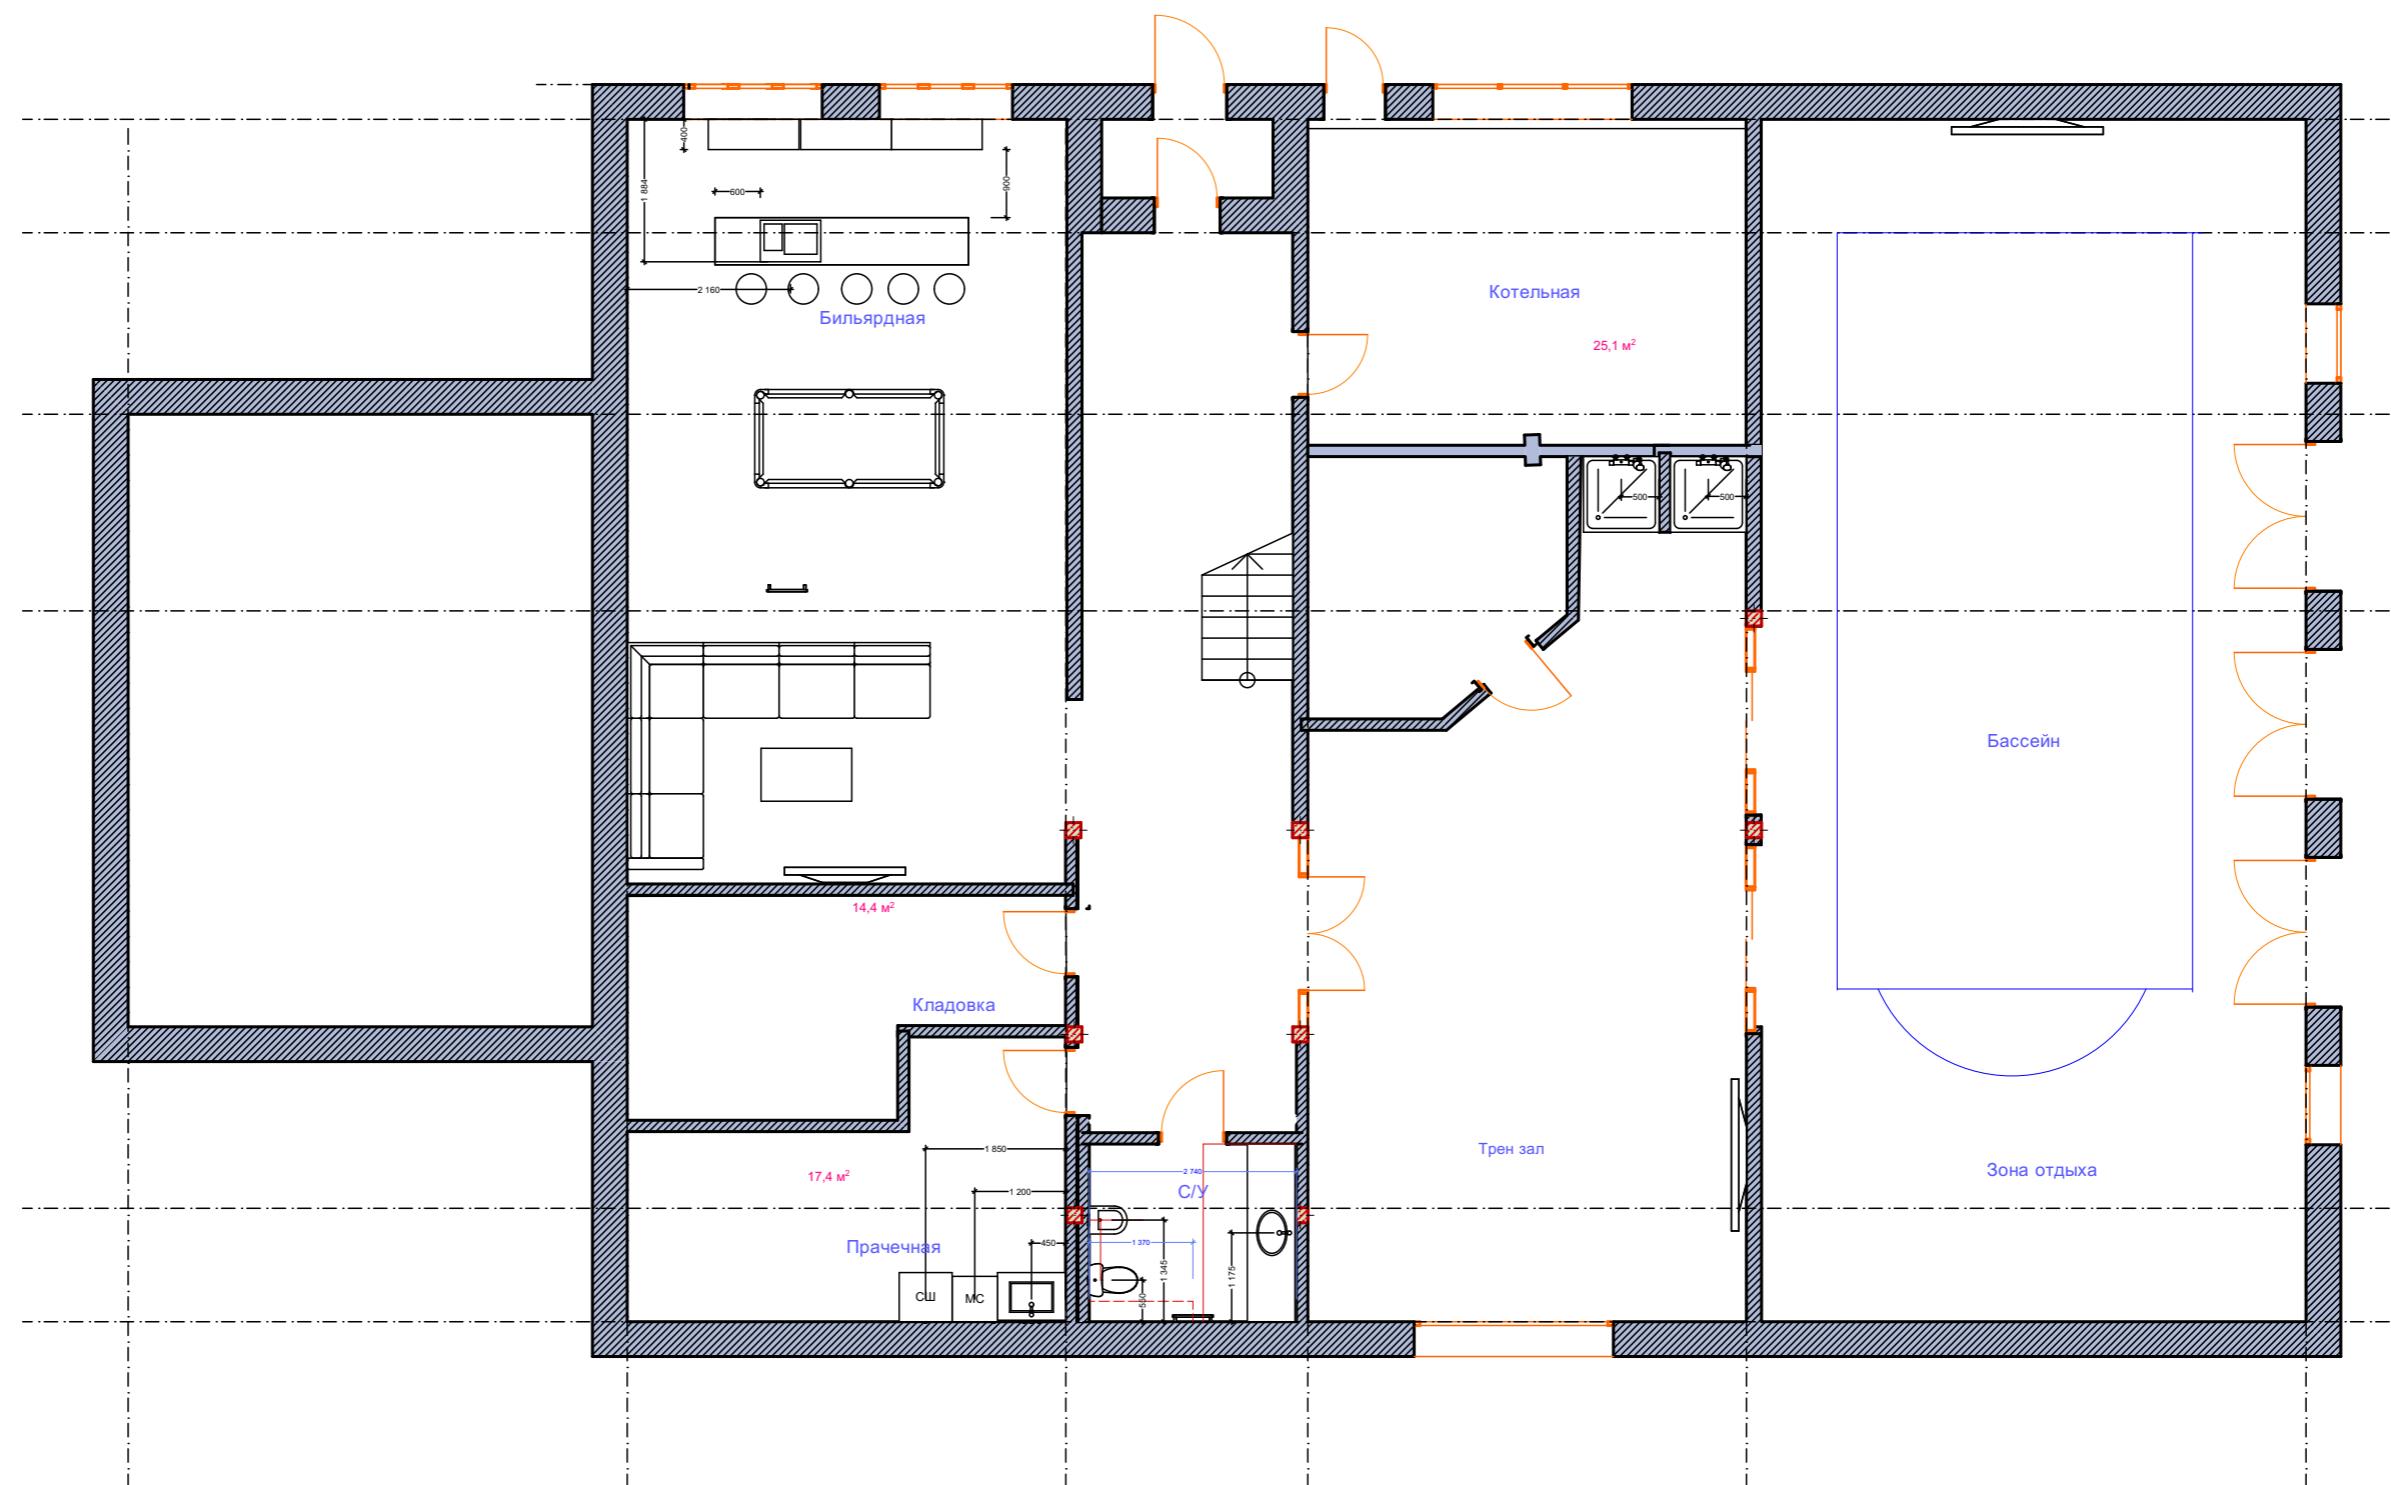


 Interior Design	Частный дом. ЖК МонакоВо!
	Дом у Озера
	Масштаб 1:100
	Дизайнер Т. Астафьев 8 915 360 0663
	Лист 37 из 11

# Схема сантехники 1-й этаж

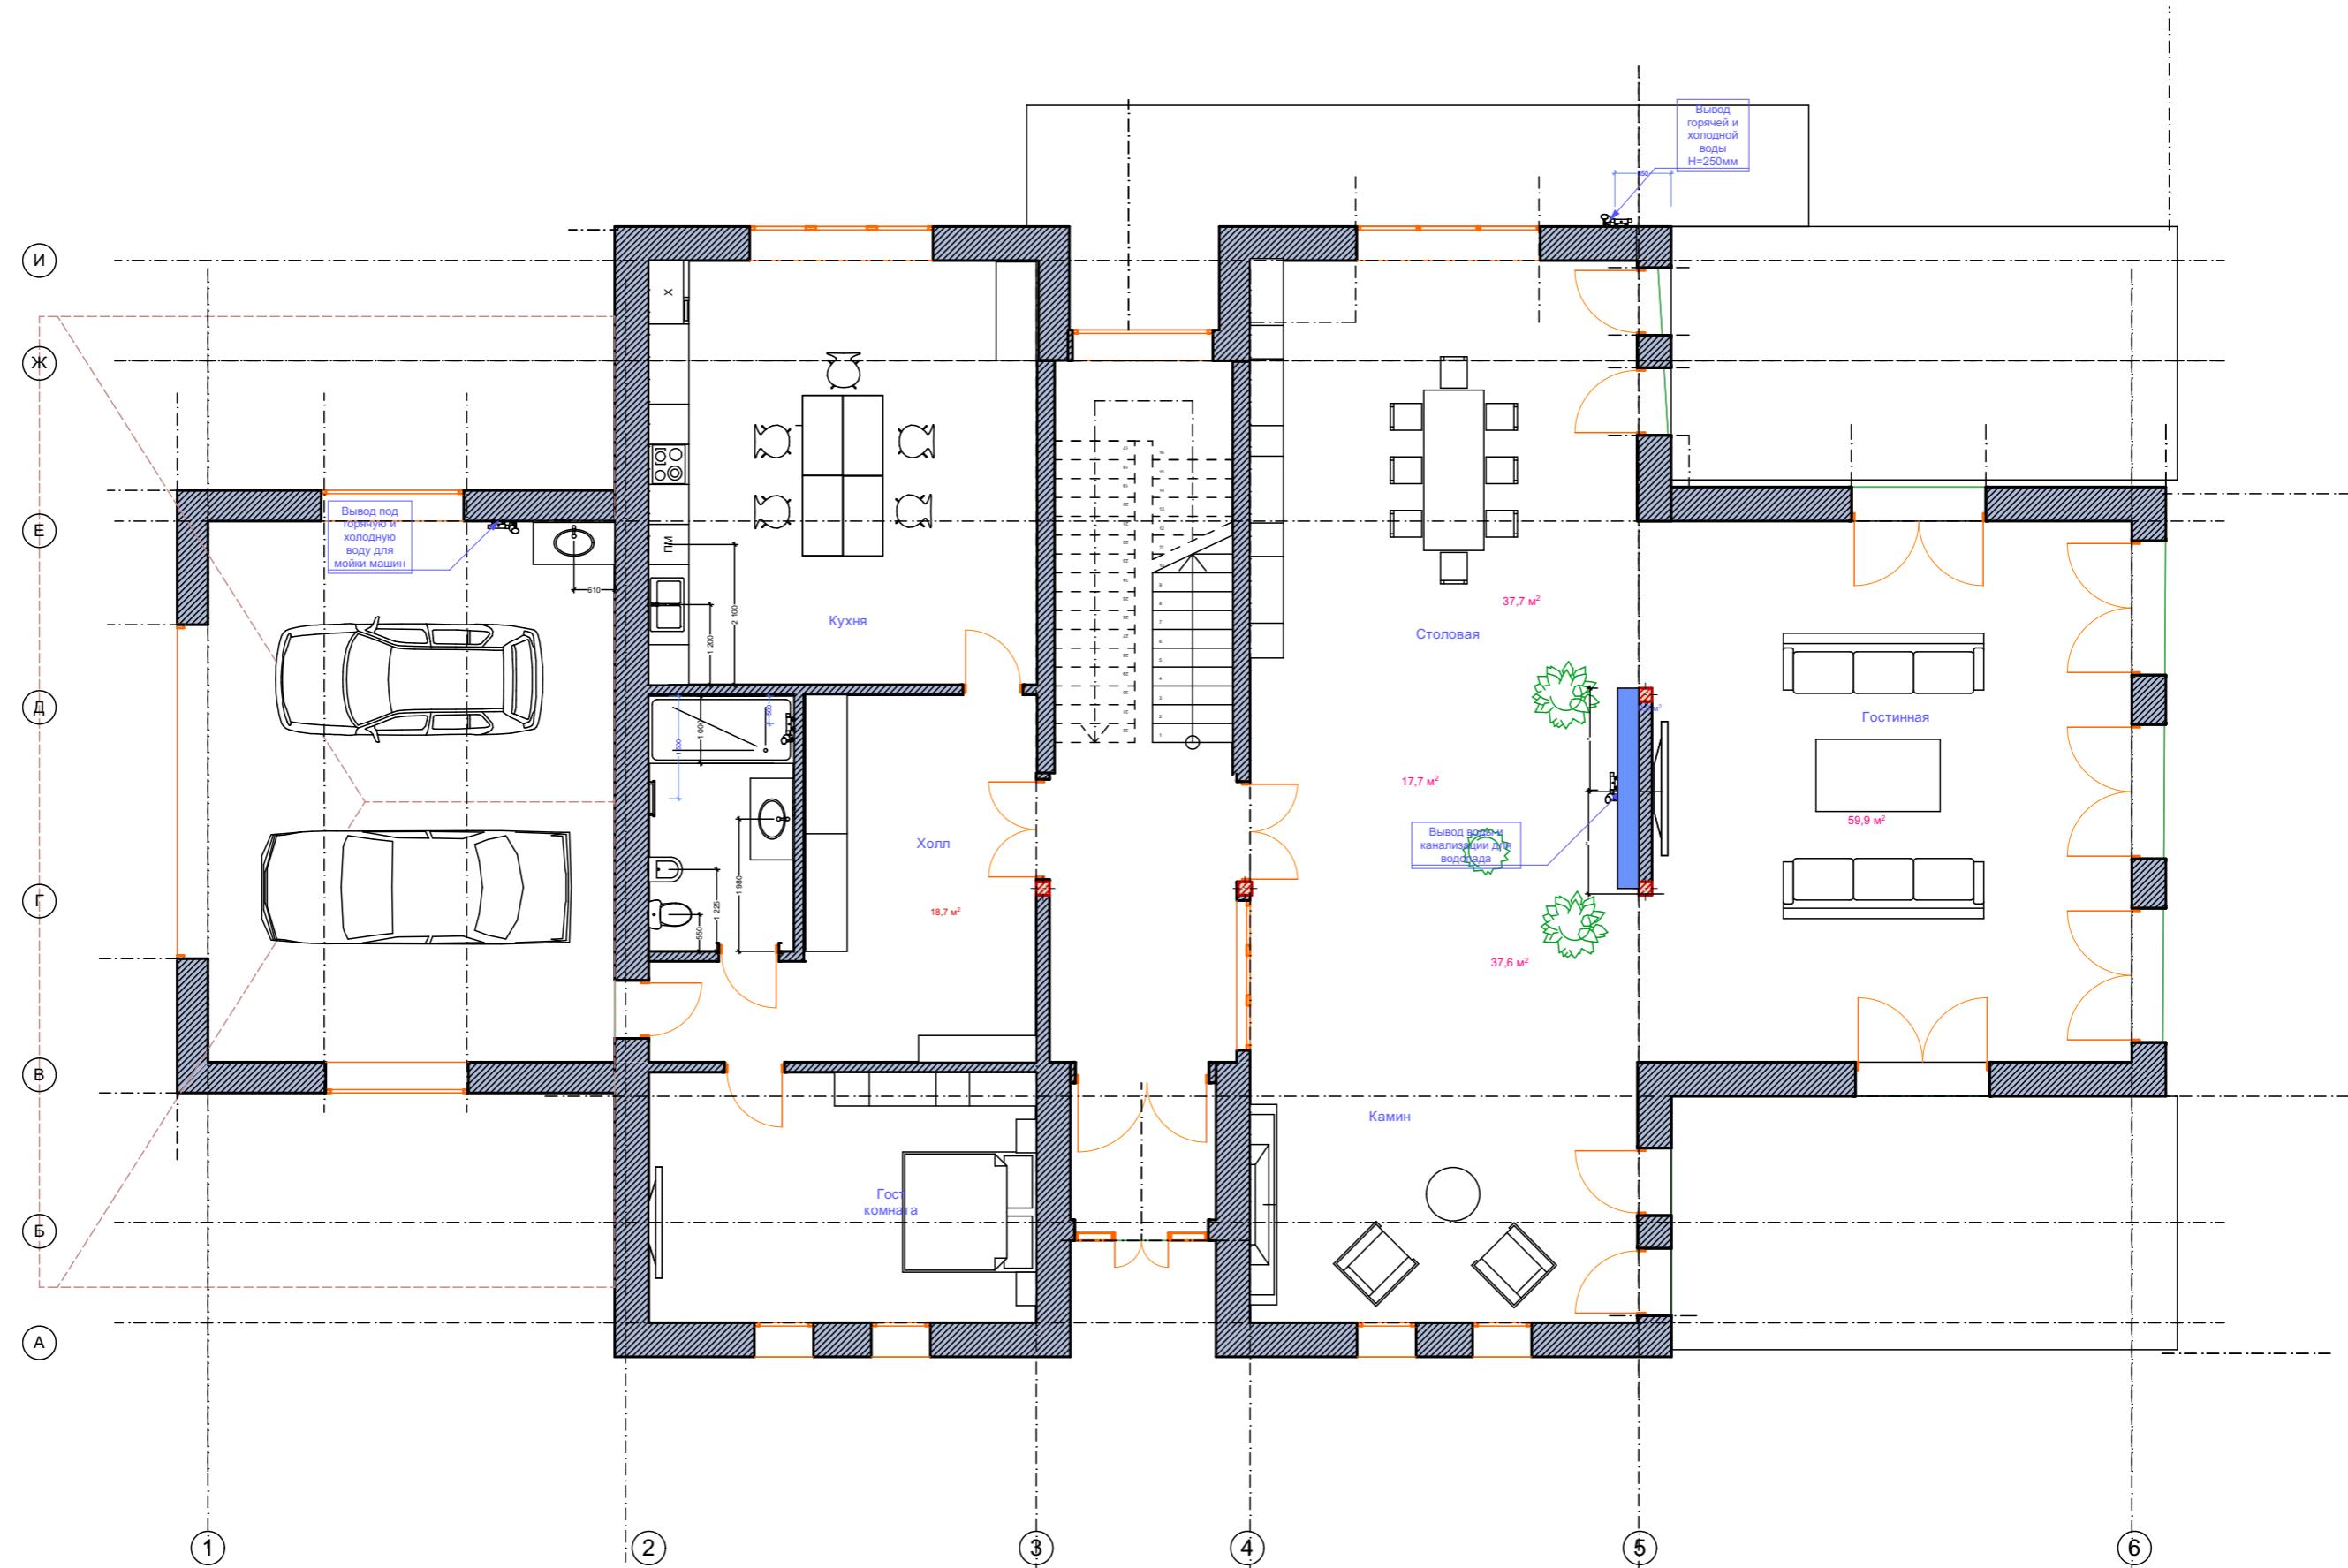

	Частный дом. ЖК МонакоВо!	
	Дом у Озера	Масштаб 1:100
	Дизайнер Т. Астафьев 8 915 360 0663	Лист 38 из 11

## *Схема сантехники 2-й этаж*

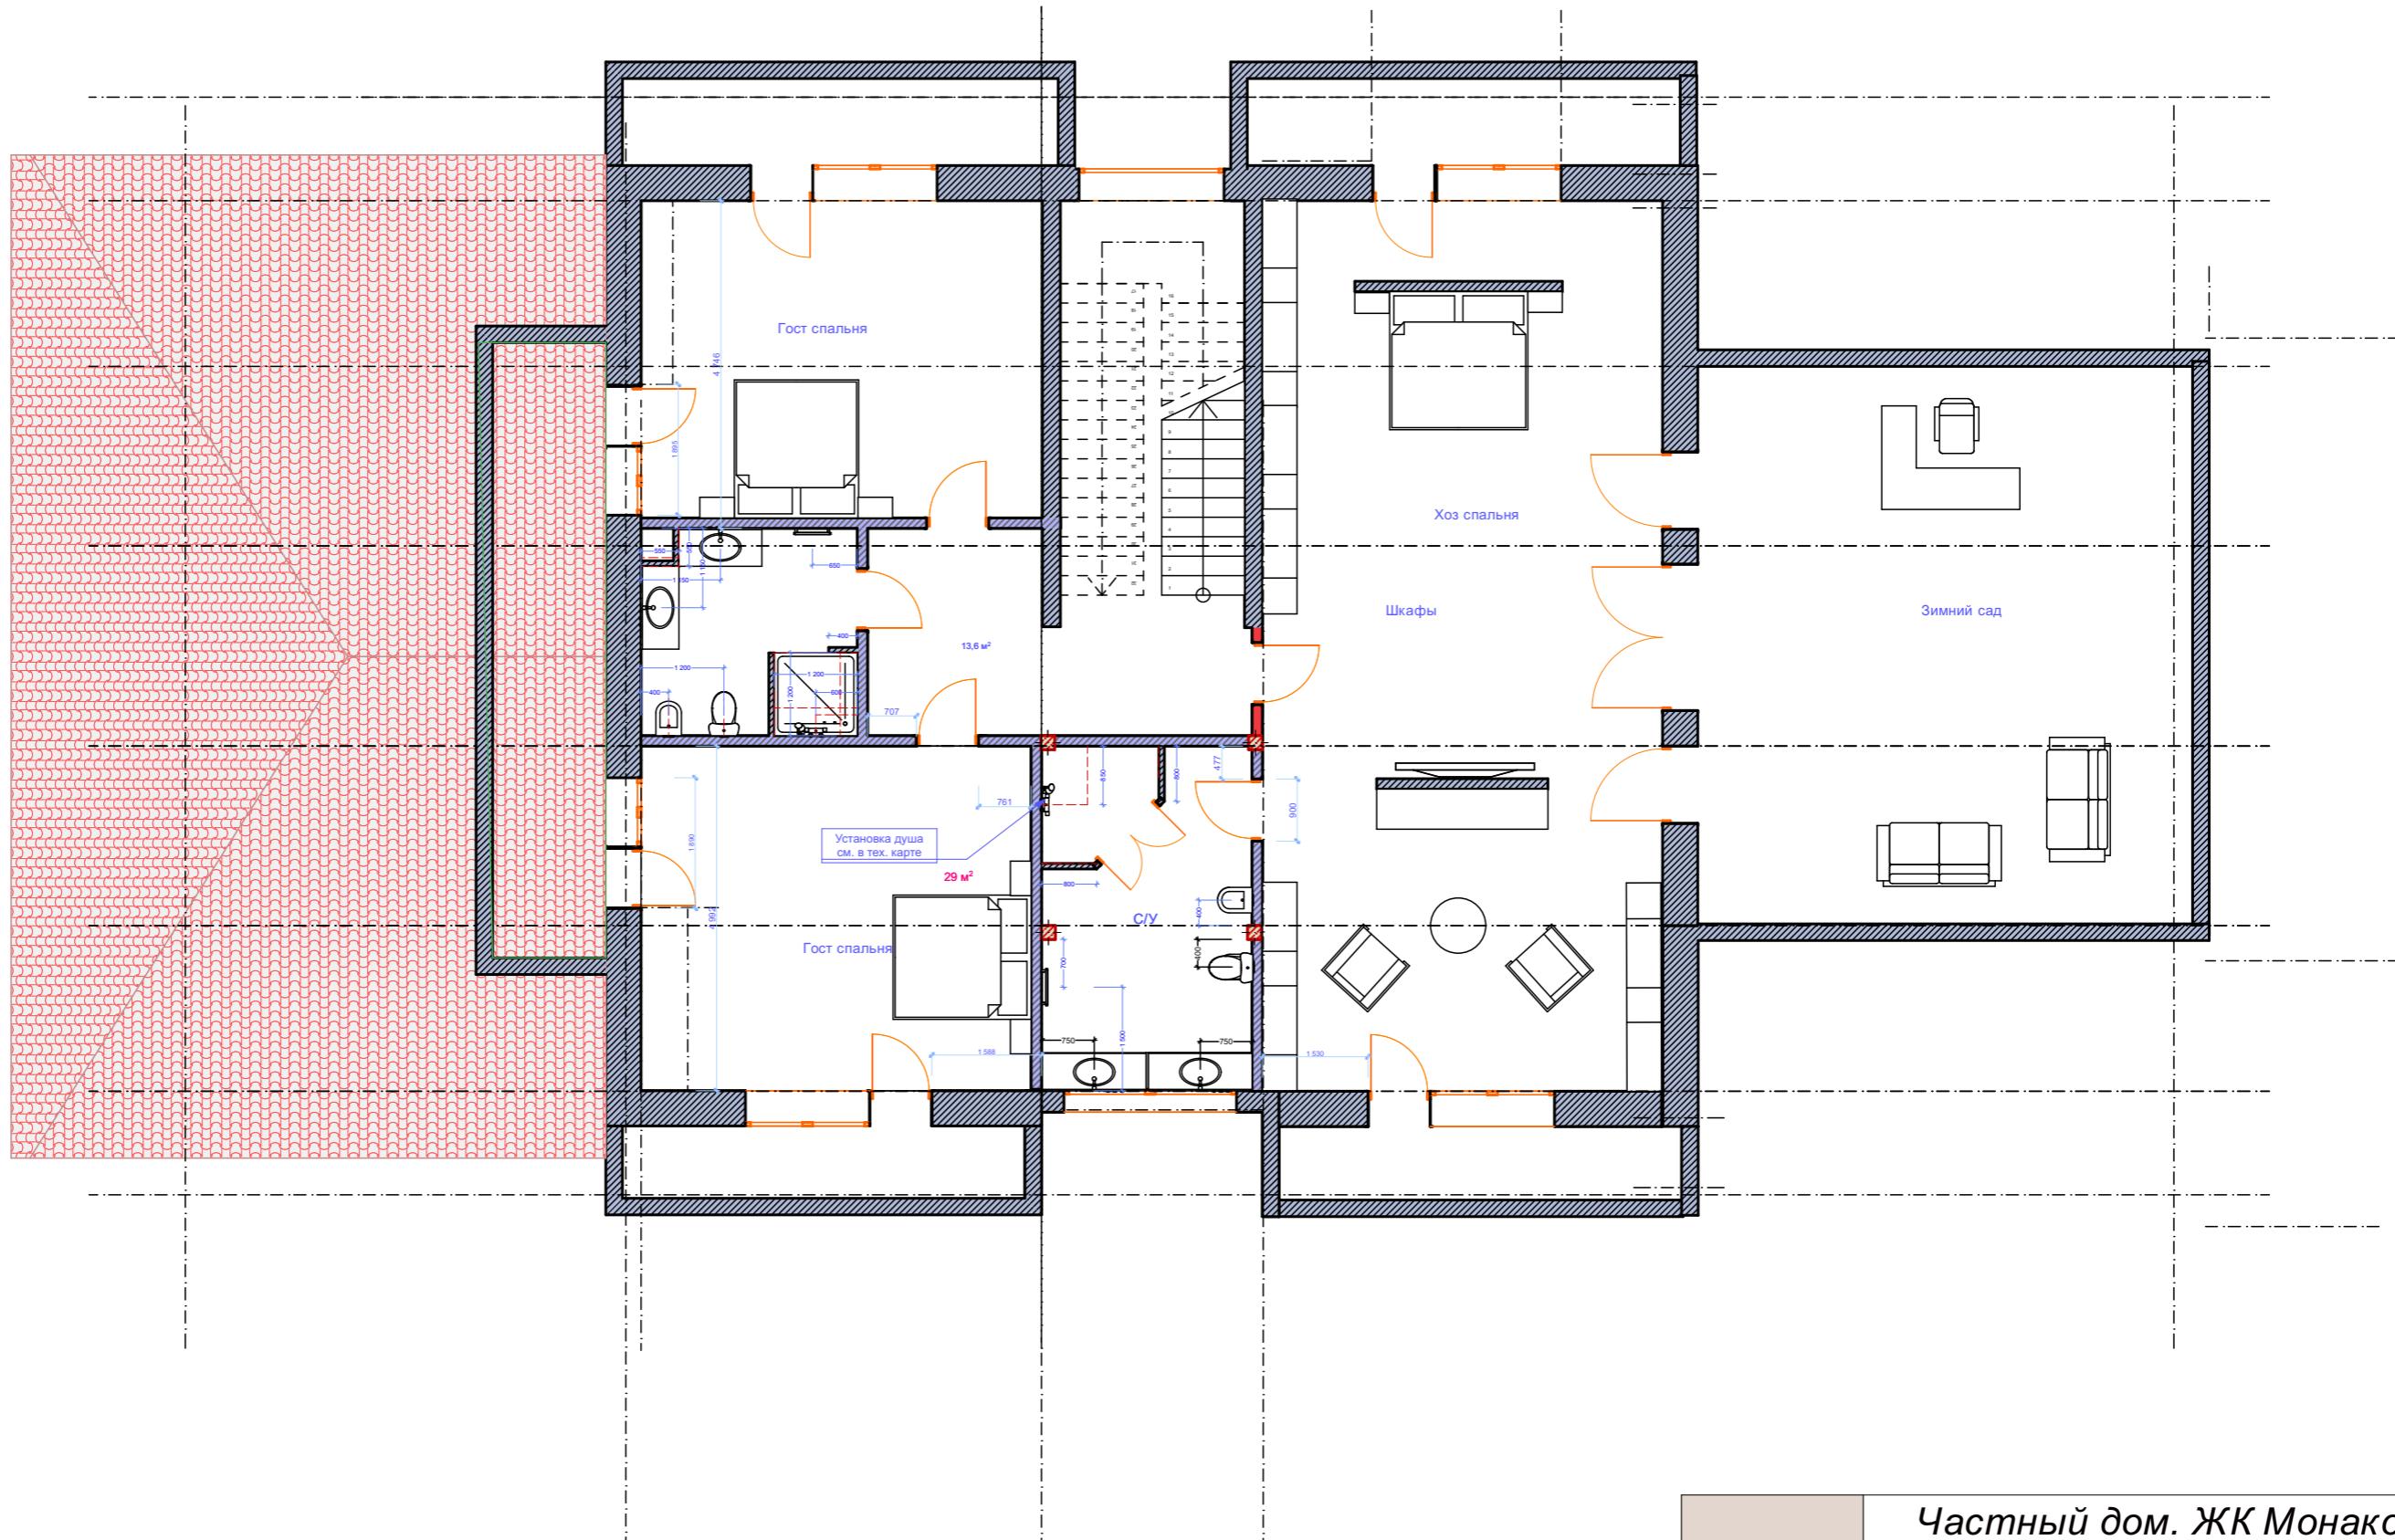

**Частный дом. ЖК МонакоВо!**


Дом у Озера

Масштаб 1:100

*Дизайнер Т. Астафьева 8 915 360 0663*

Лист 39 из 11

# Схема электрики цокольный этаж

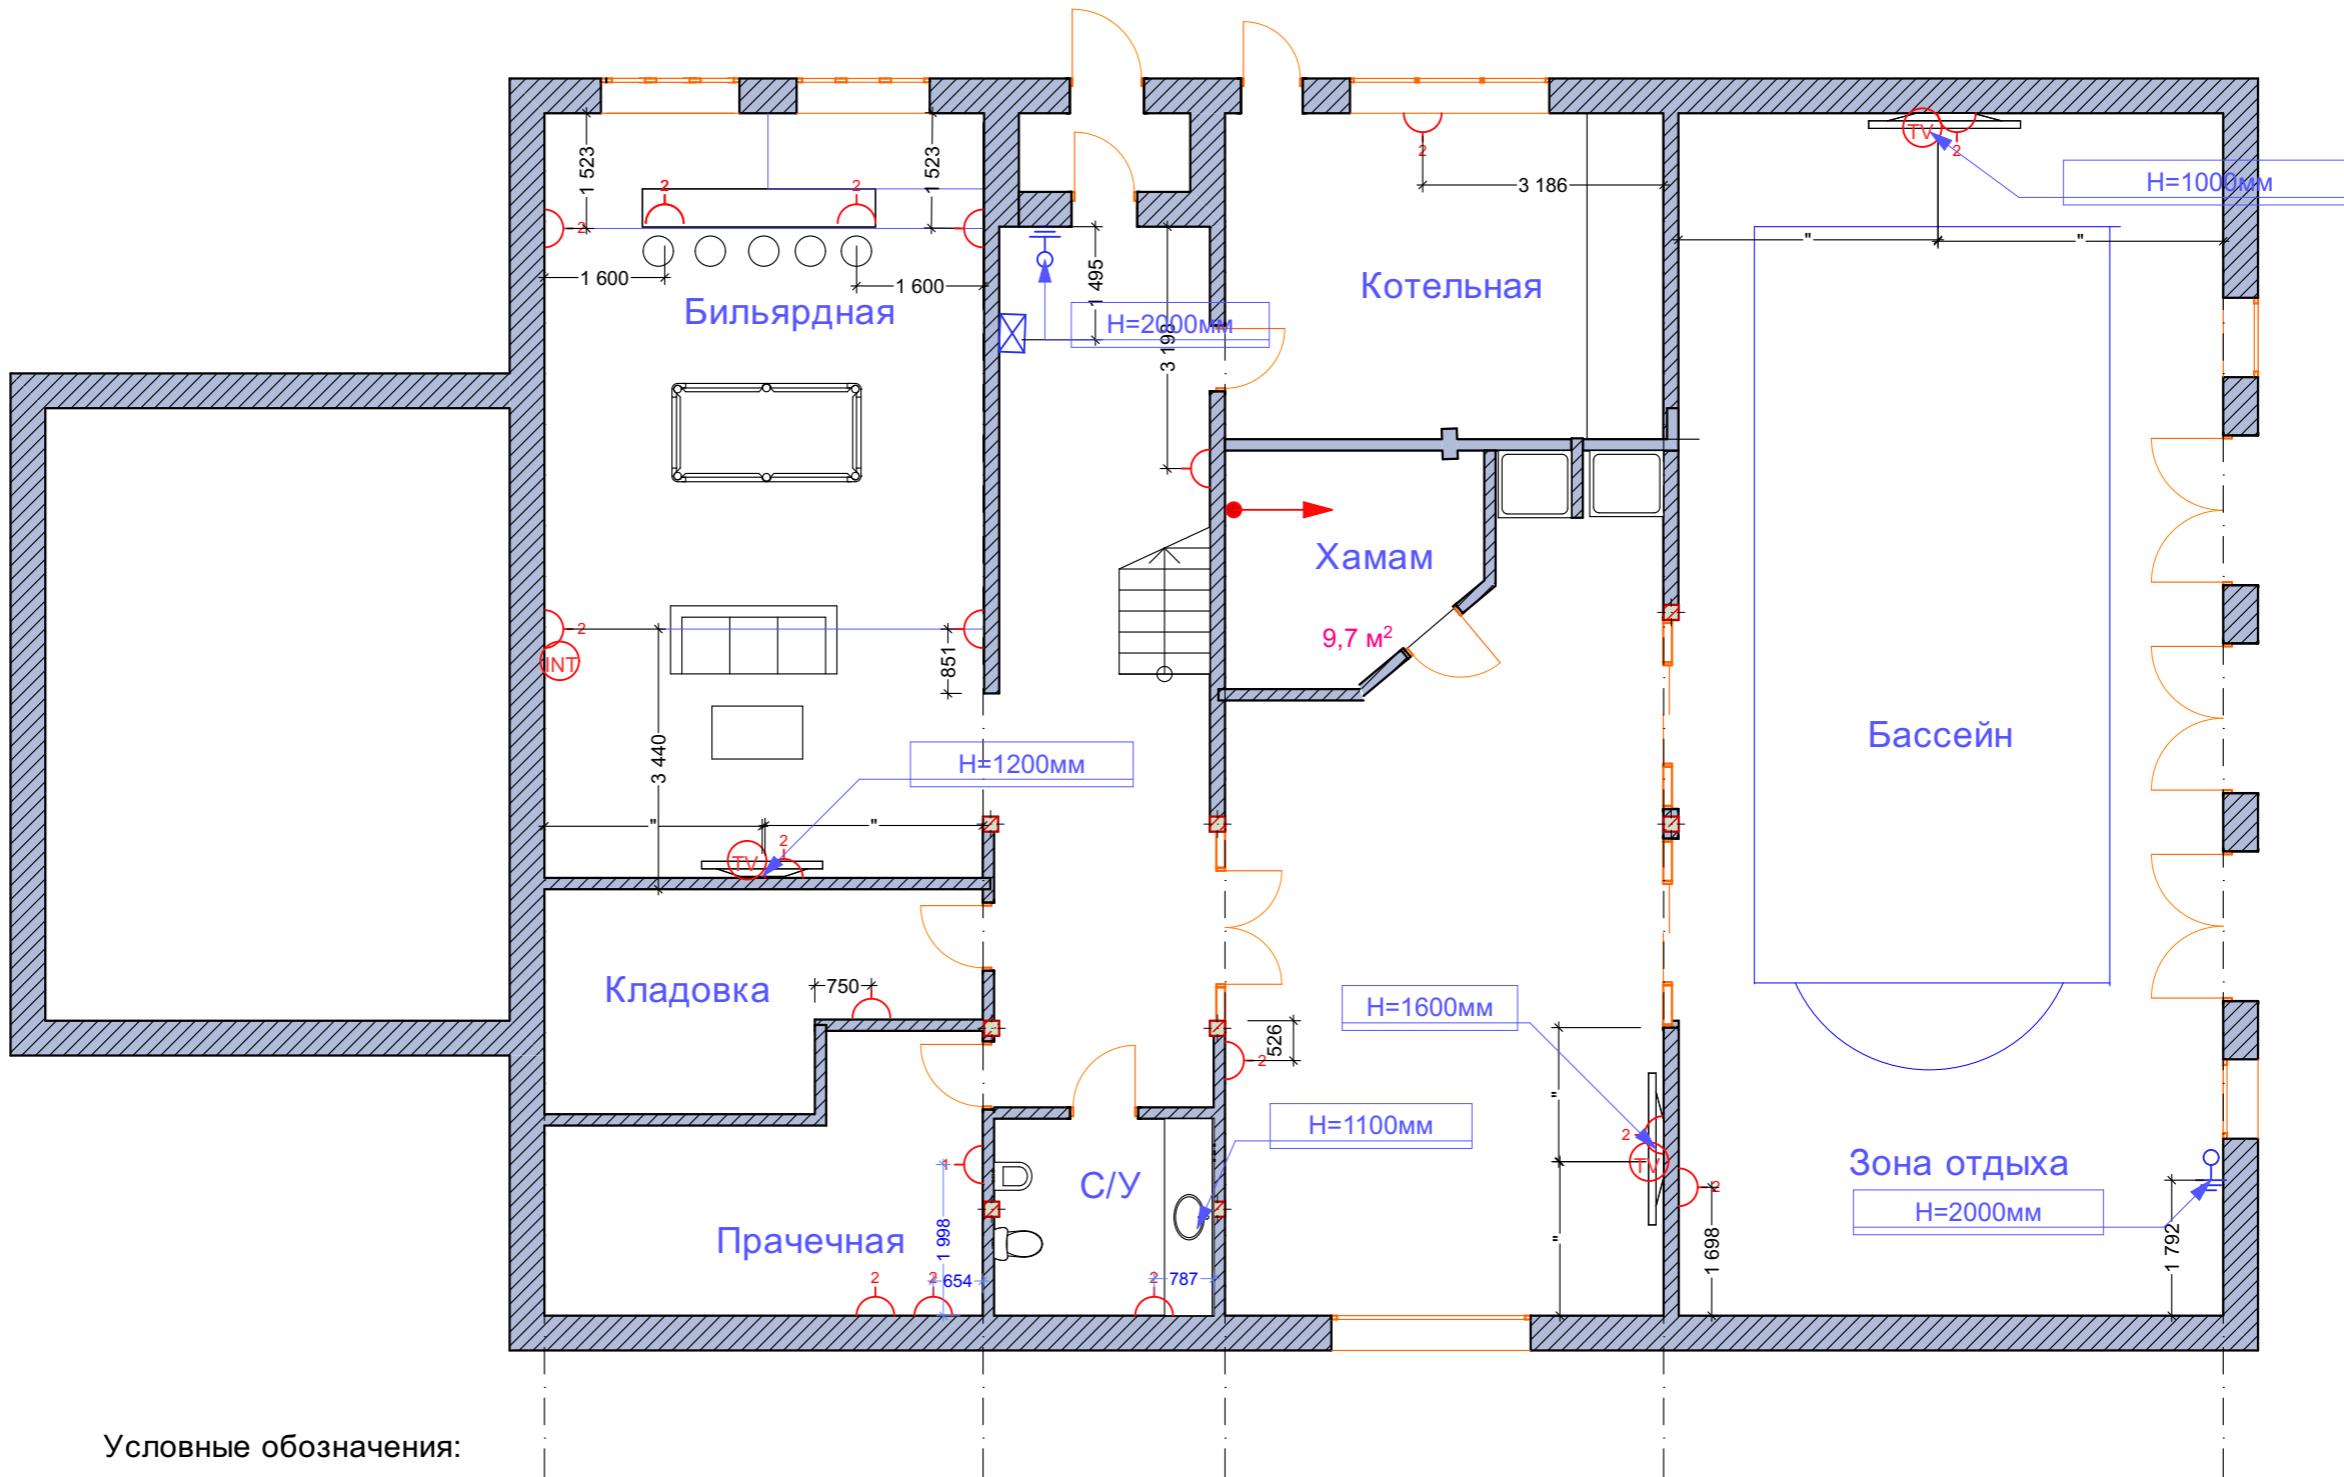

## Условные обозначения:

- |  |                         |
|--|-------------------------|
|  | - розетка с заземлением |
|  | - двойная розетка       |
|  | - тройная розетка       |
|  | - четвертная розетка    |
|  | - телефон               |
|  | - телевизор             |
|  | - интернет              |
|  | - электрический вывод   |
|  | - звонок                |
|  | - электрический щит     |



Частный дом. ЖК МонакоВо!


Дом у Озера

Масштаб 1:100

Дизайнер Т. Астафьев 8 915 360 0663

Лист 40 из 11

# Схема электрики 1-й этаж

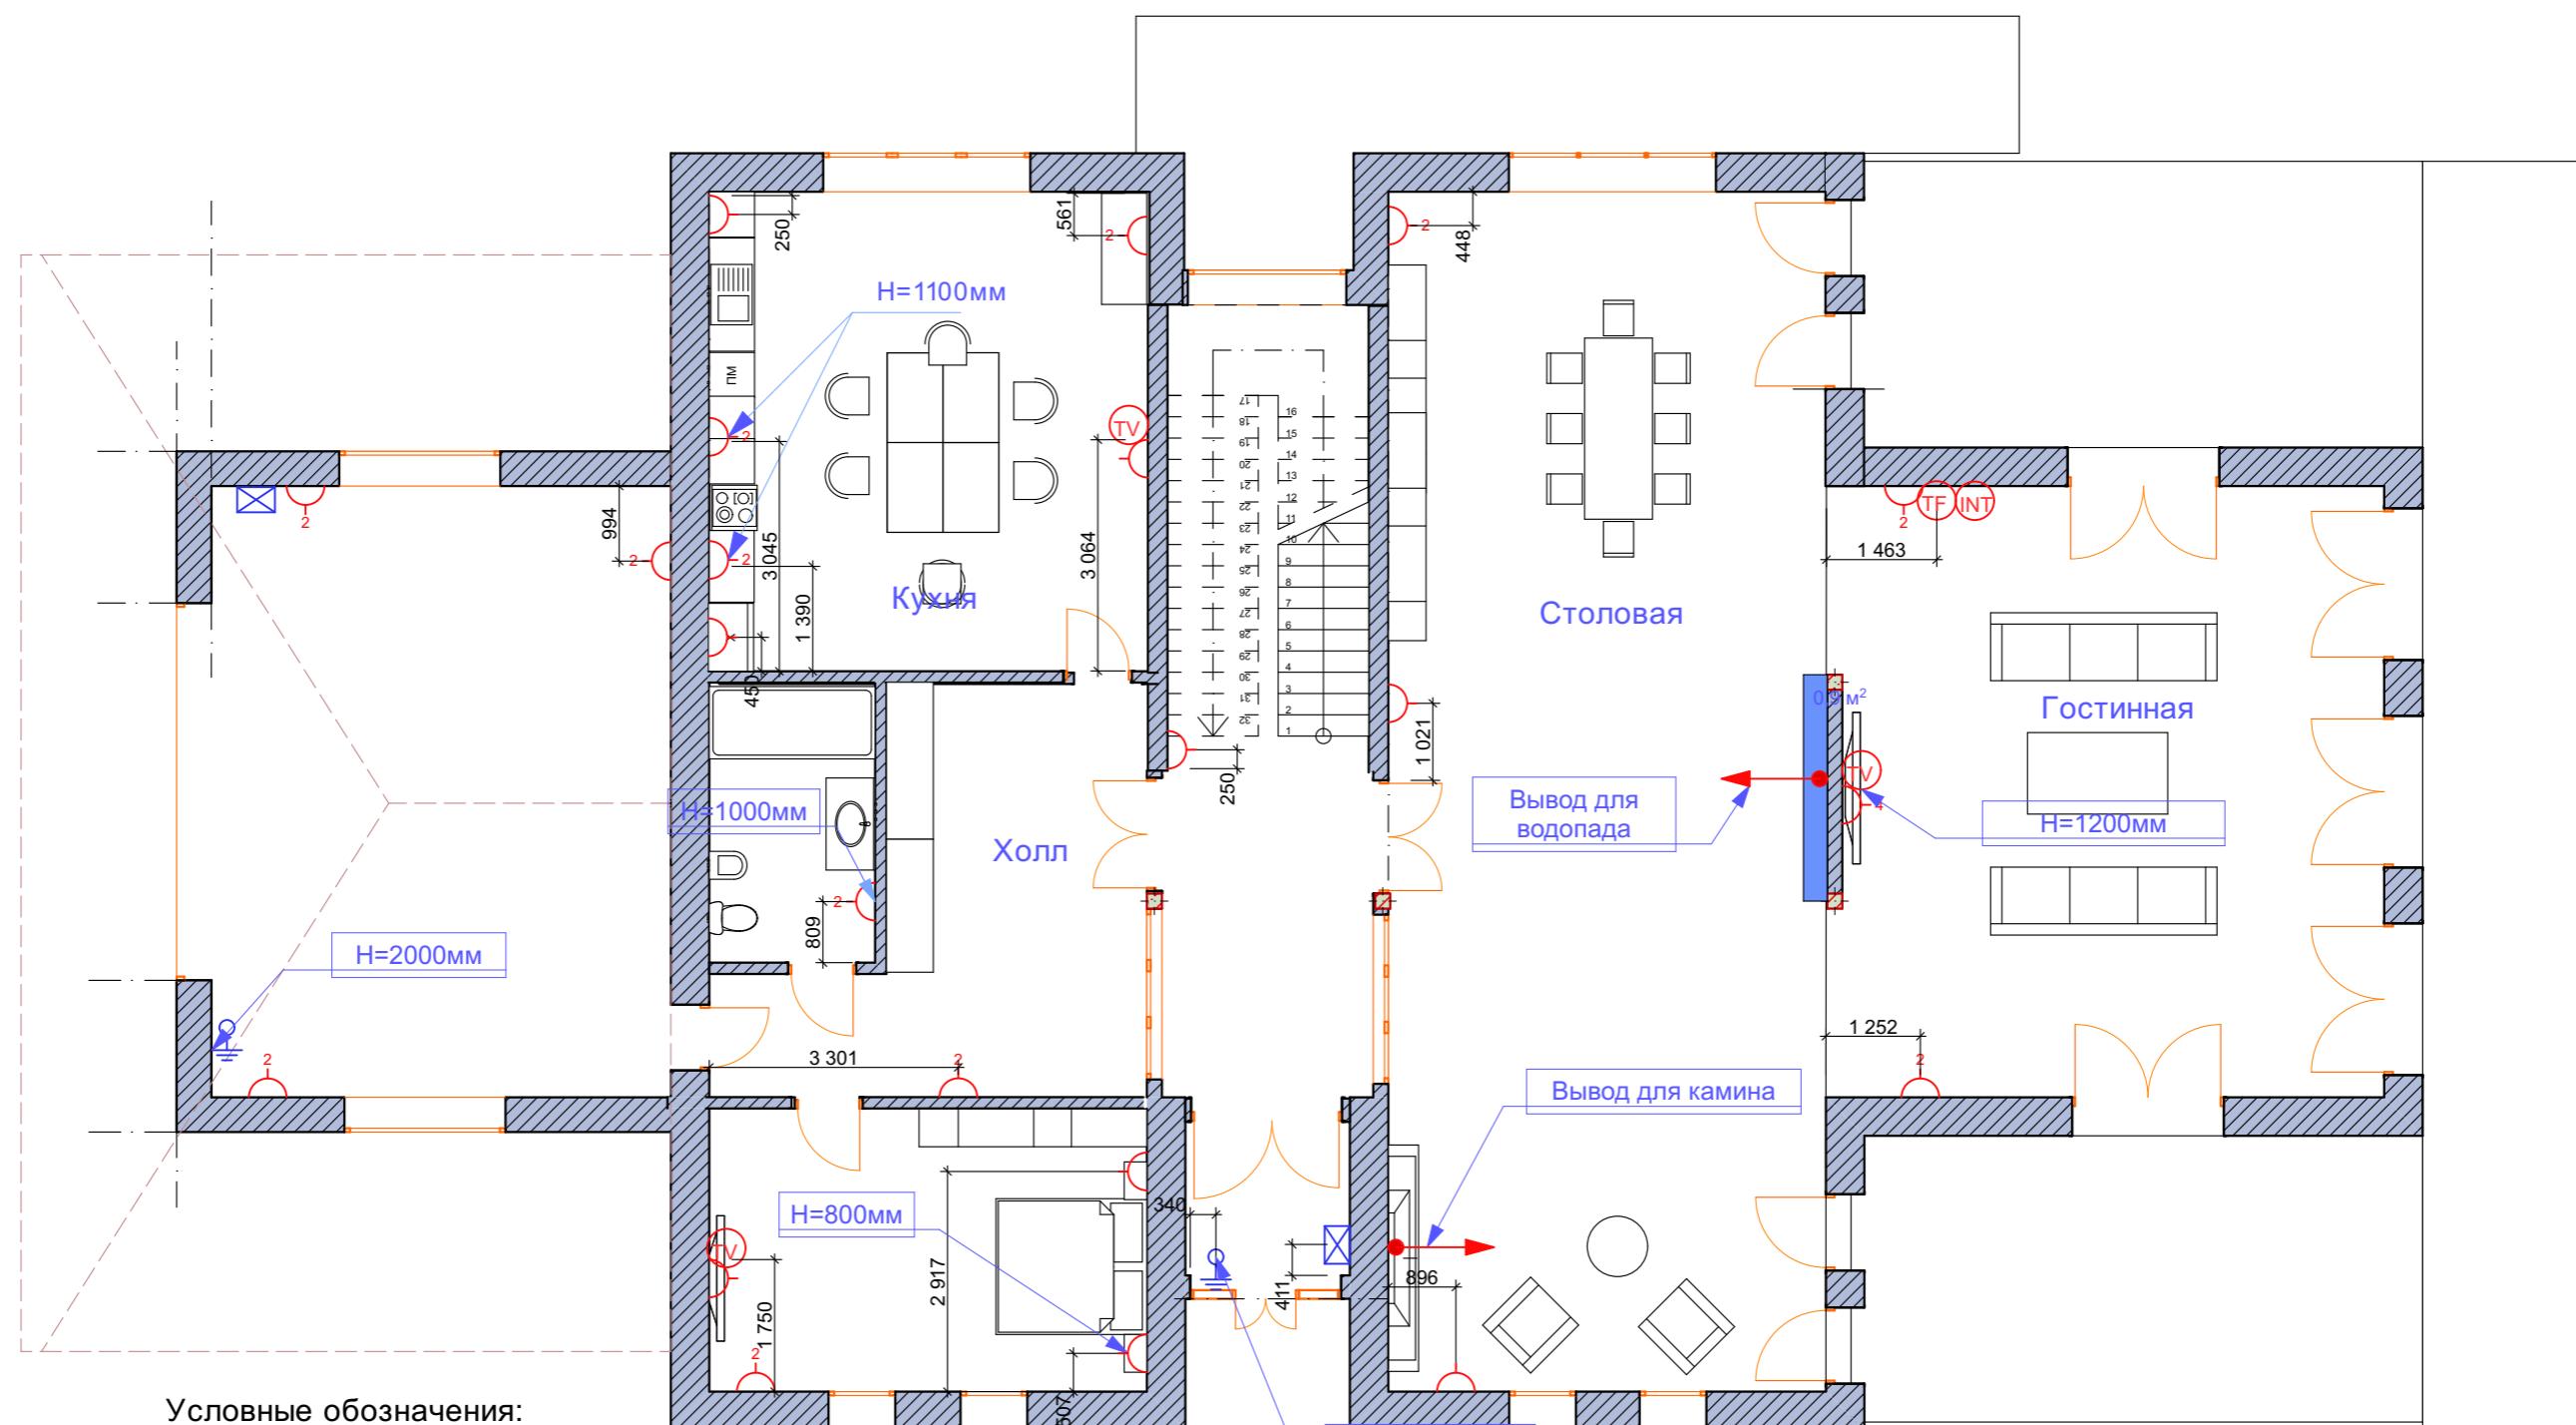

Частный дом. ЖК МонакоВо!


Дом у Озера

Масштаб 1:100

Дизайнер Т. Астафьев 8 915 360 0663

Лист 41 из 11


# Схема электрики 2-й этаж

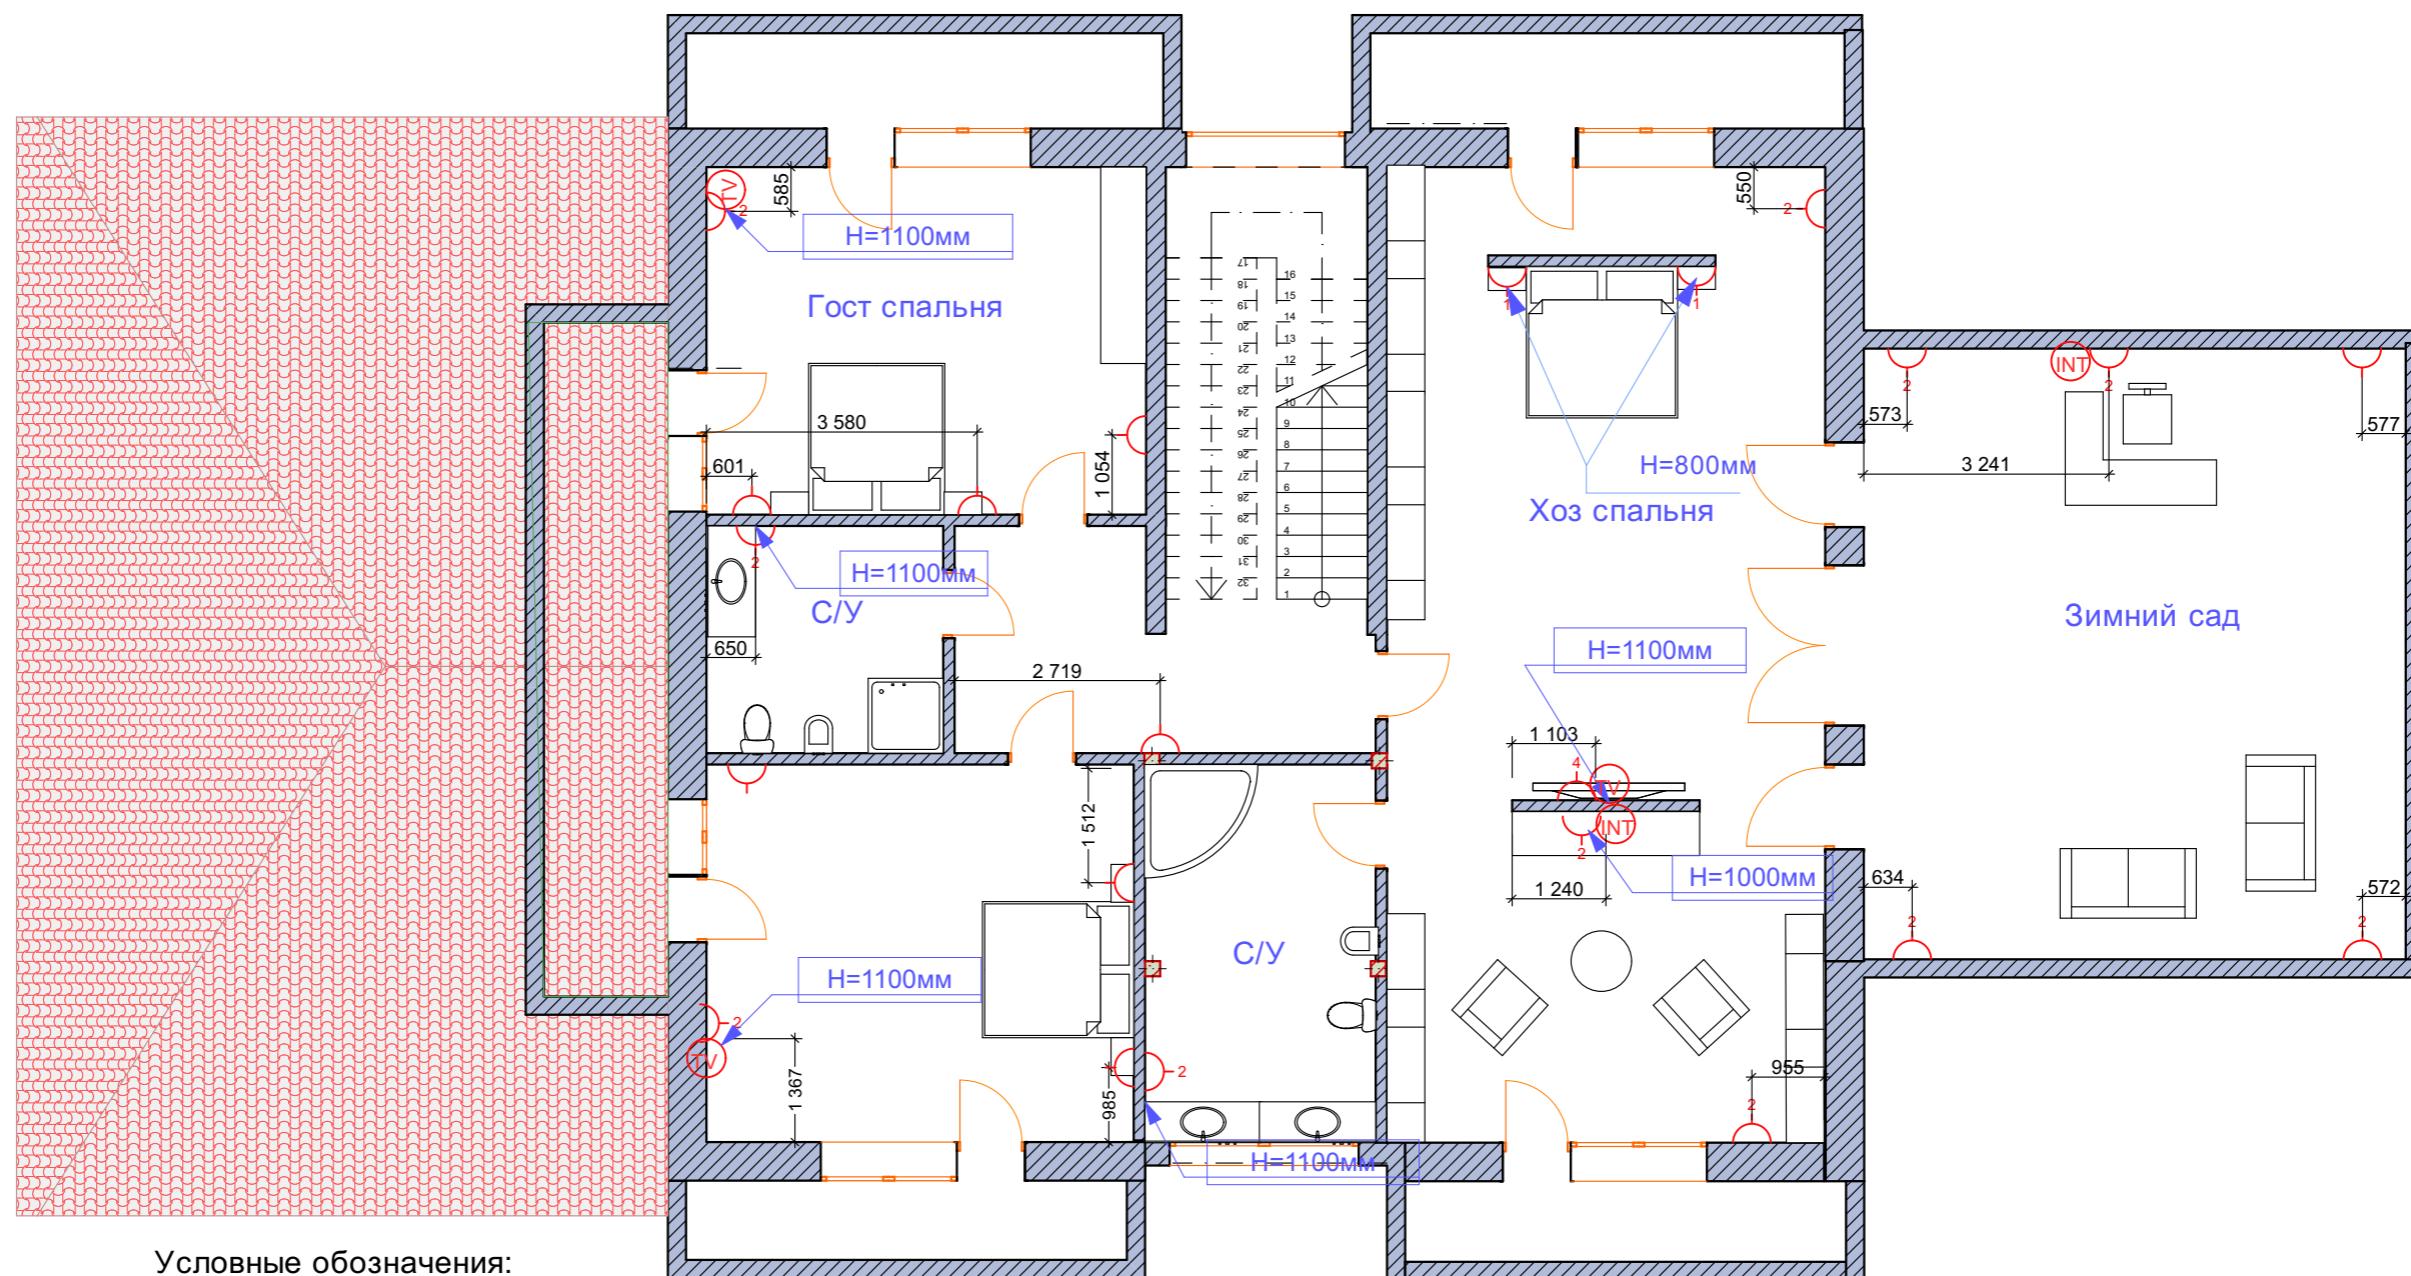

- 1 - розетка с заземлением
- 2 - двойная розетка
- 3 - тройная розетка
- 4 - четверная розетка
- TF - телефон
- TV - телевизор
- (INT) - интернет
- - электрический вывод
- - звонок
- - электрический щит


	Частный дом. ЖК МонакоВо!	
	Дом у Озера	Масштаб 1:100
	Дизайнер Т. Астафьев 8 915 360 0663	
	Лист 42 из 11	

# План потолков цокольный этаж

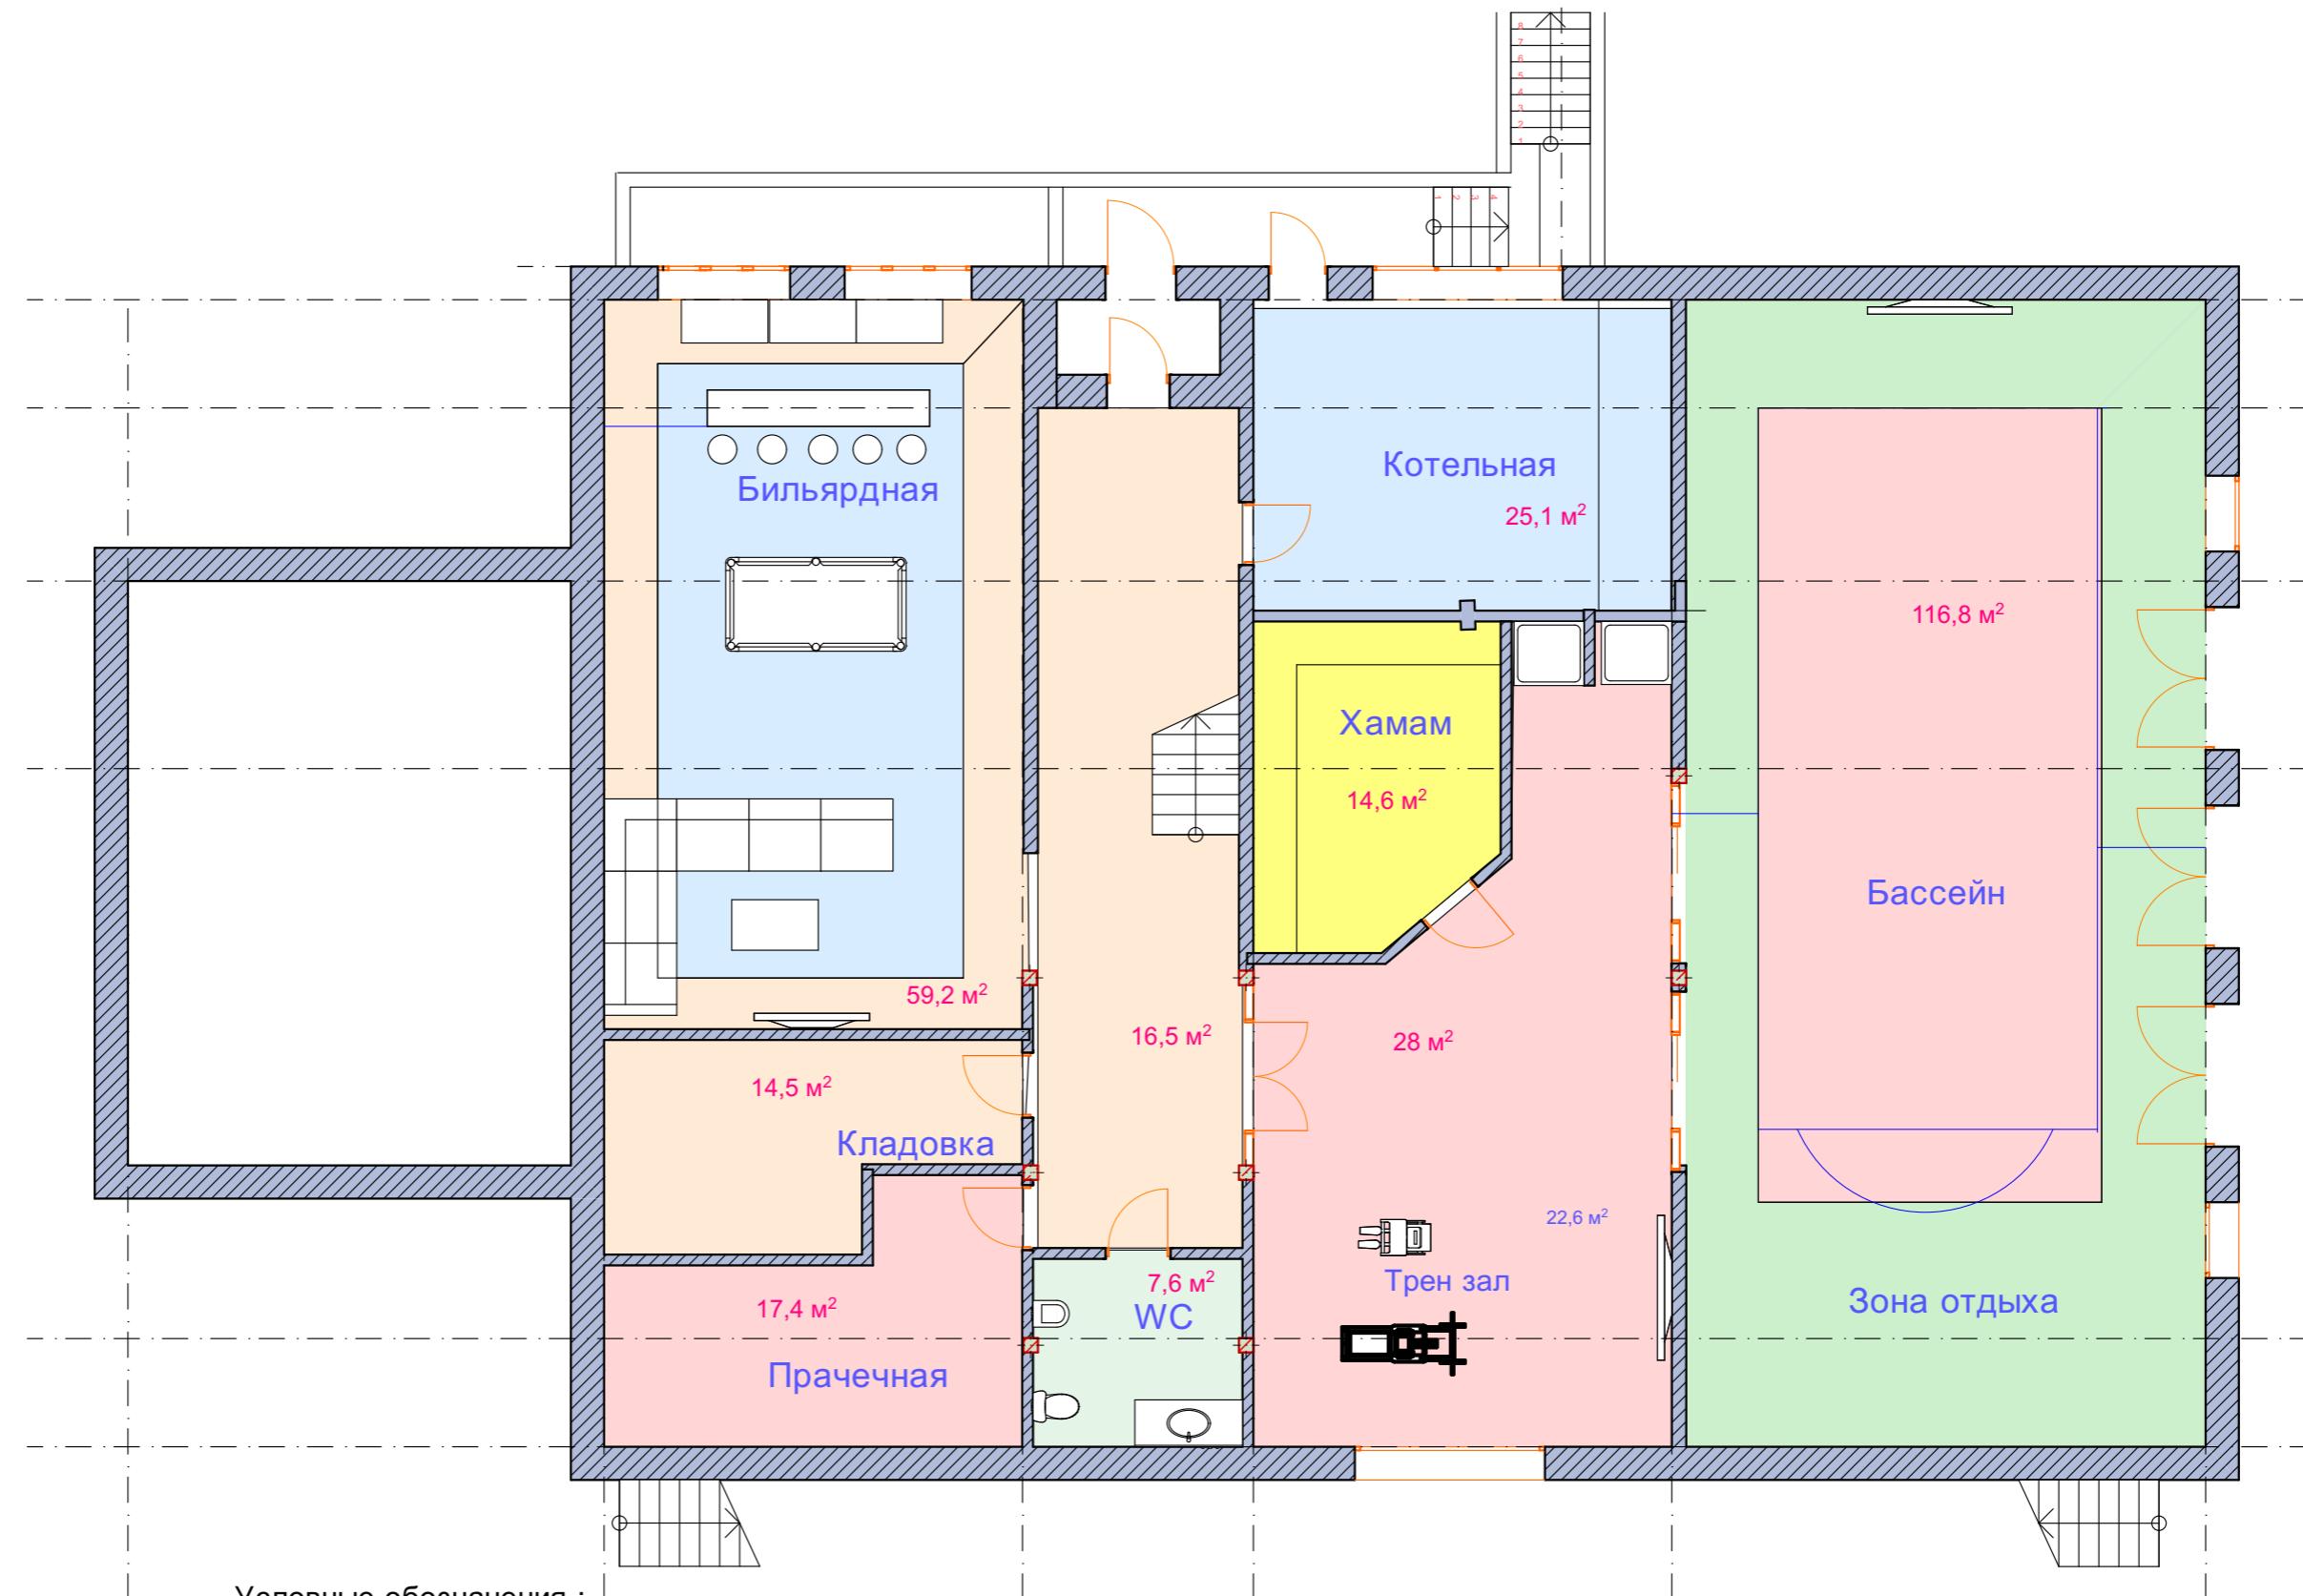

Условные обозначения :

- [Blue square] - существующий потолок
- [Orange square] - потолок из ГКЛ
- [Green square] - потолок из влагостойкого ГКЛ
- [Pink square] - натяжной потолок

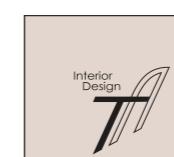

Частный дом. ЖК МонакоВо!


Дом у Озера

Масштаб 1:100

Дизайнер Т. Астафьев 8 915 360 0663


Лист 43 из 11

# План потолков 1-й этаж

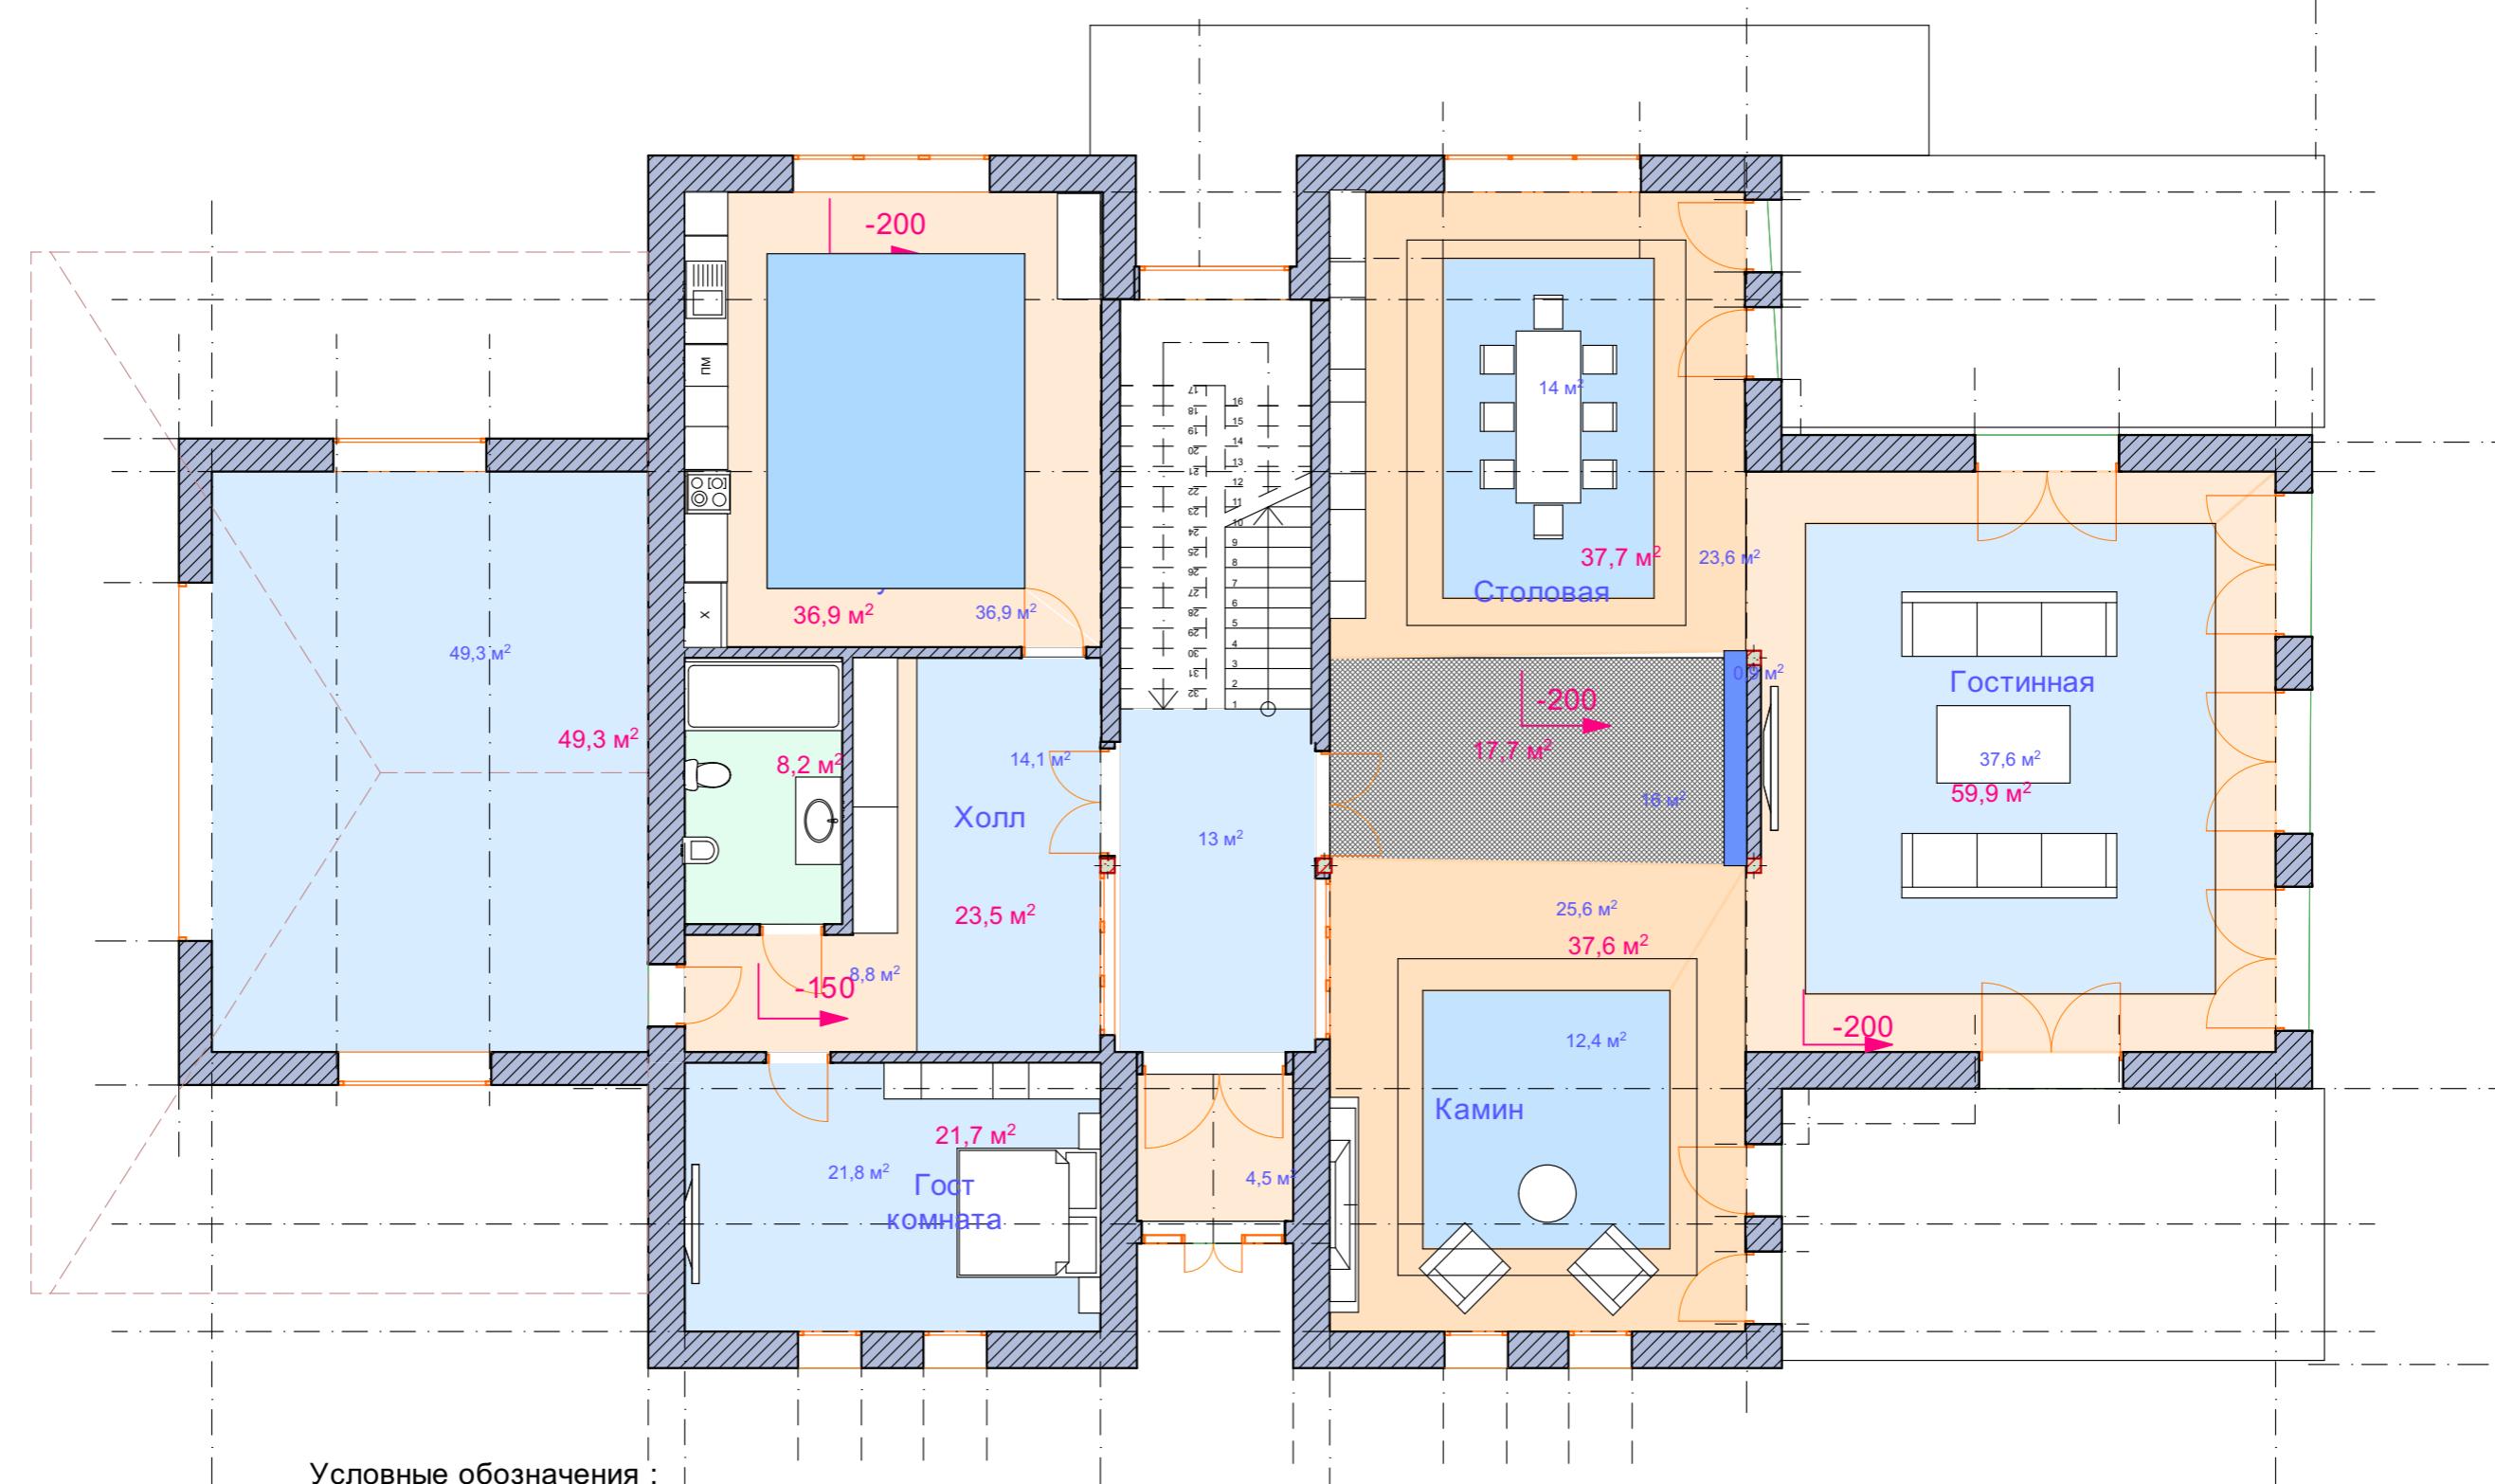


	Частный дом. ЖК МонакоВо!	
	Дом у Озера	Масштаб 1:100
	Дизайнер Т. Астафьев 8 915 360 0663	
	Лист 44 из 11	

## План потолков 2-й этаж

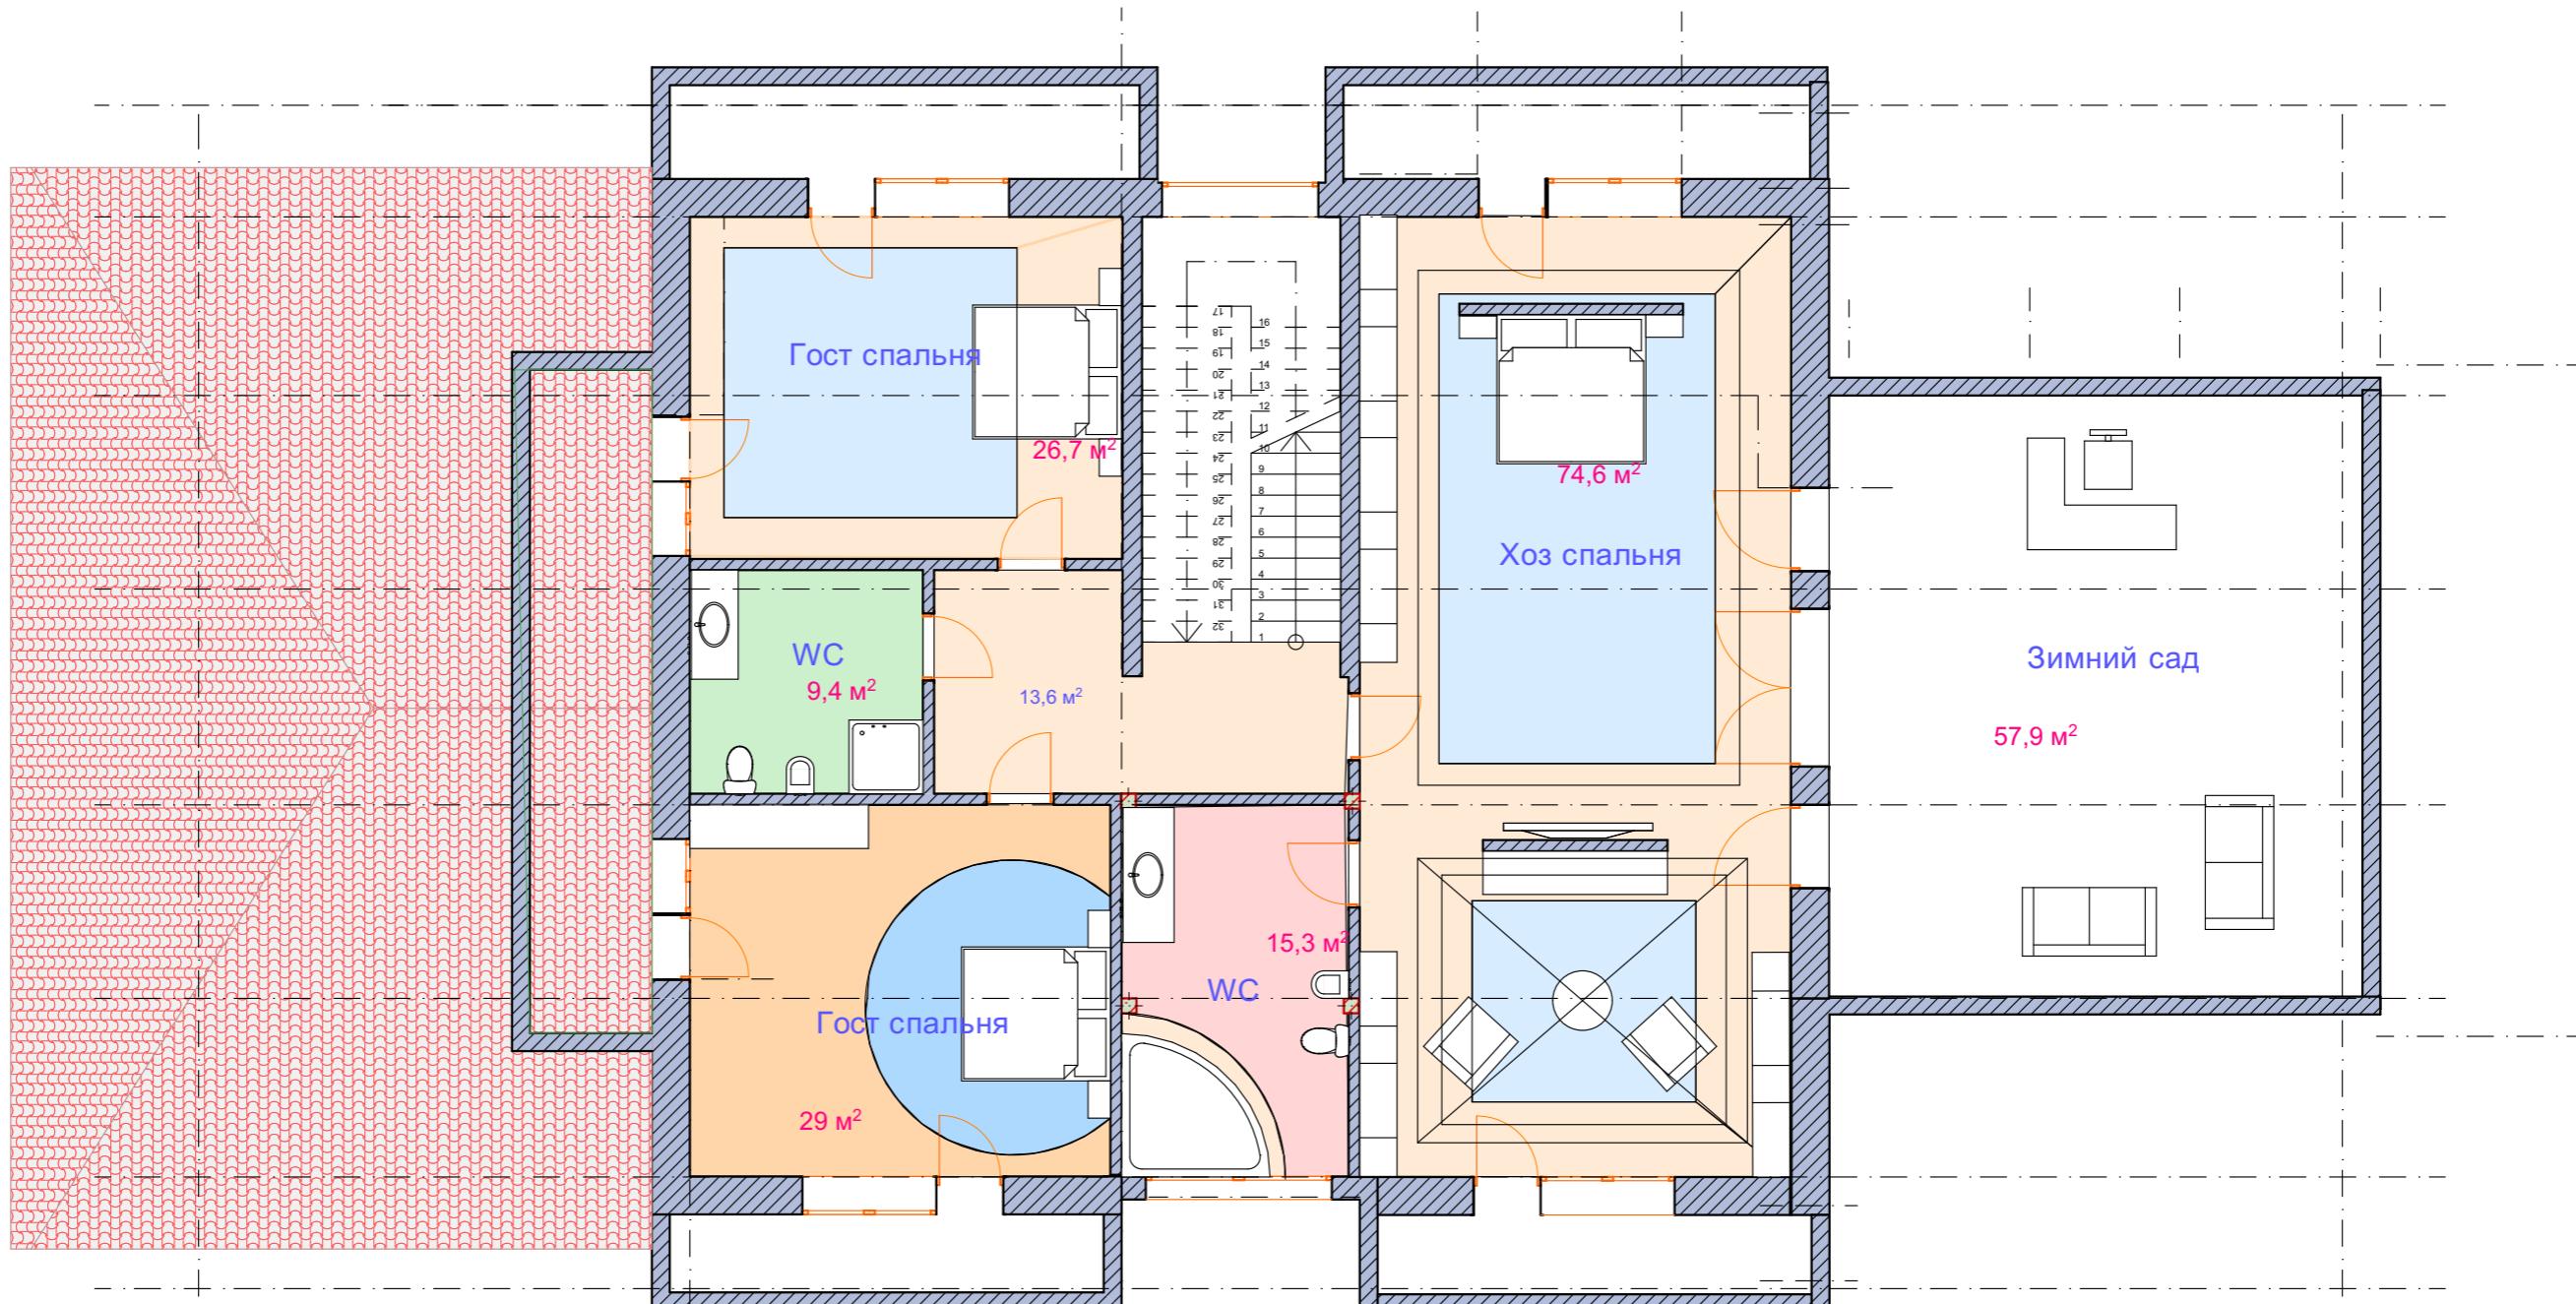

### Условные обозначения :

- существующий потолок
- потолок из ГКЛ
- потолок из влагостойкого ГКЛ
- натяжной потолок
- уровни потолков

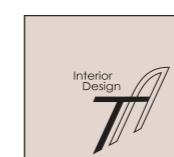

Частный дом. ЖК МонакоВо!


Дом у Озера

Масштаб 1:100

Дизайнер Т. Астафьев 8 915 360 0663

Лист 45 из 11

# Схема расположения светильников цокольный этаж

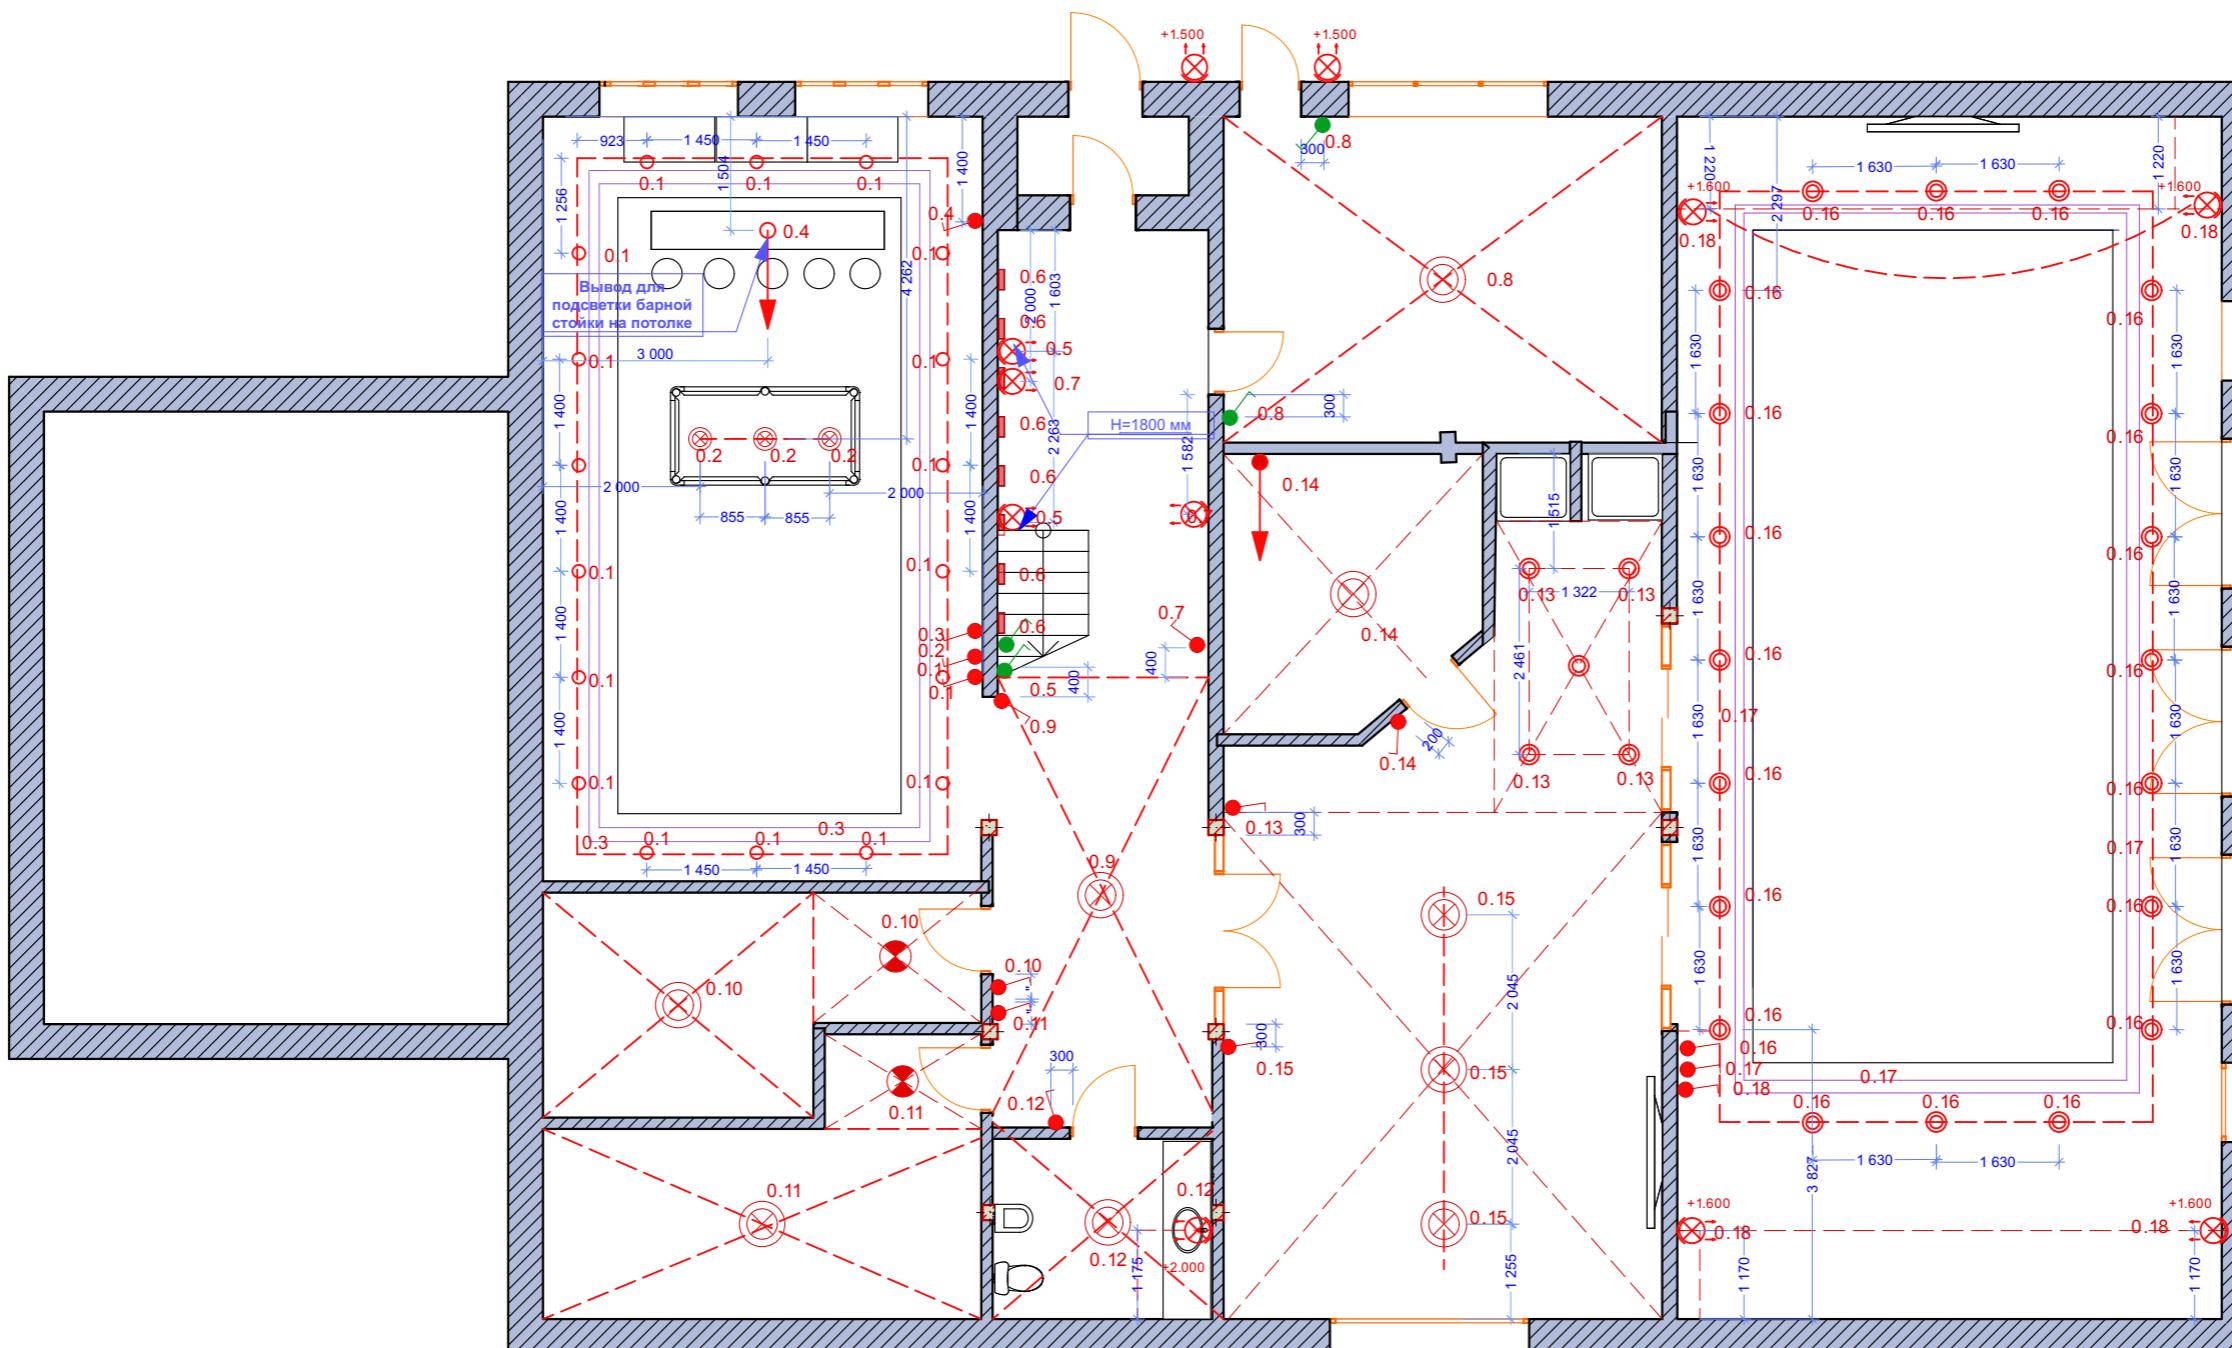

## Условные обозначения:

### УСЛОВНЫЕ ОБОЗНАЧЕНИЯ

- ( ) - потолочные светильники (не менее 60 Вт)  
энергосберегающая лампа
- ( ) - бра на отм.+1.800 от Ч.П.этажа  
энергосберегающая лампа
- ( ) - точечные светильники
- подсветка пола в стене 250 мм от чистого пола

- однорожковые светильн. Герм.

- бра на отм. +1.600 от Ч.П. этажа Герм.

- выводы под подсветку

00 - группа включения


- проходные переключатели

- переключ. на отм. +1.000 от Ч.П. этажа

## ПРИМЕЧАНИЯ

БЛОКИ ВЫКЛЮЧАТЕЛЕЙ (КРОМЕ ОГОВОРЕННЫХ)  
НА ОТМ. 1.000 ОТ Ч.П. ЭТАЖЕЙ  
ПРИВЯЗКИ ДАНЫ ПО ЦЕНТРУ БЛОКОВ

ВСЕ ОТМЕТКИ ДАНЫ ОТ ЧИСТОГО ПОЛА !!!

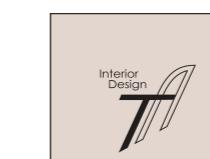

Частный дом. ЖК МонакоВо!


Дом у Озера

Масштаб 1:100

Дизайнер Т. Астафьев 8 915 360 0663

Лист 46 из 11

# Схема расположения светильников 1-й этаж

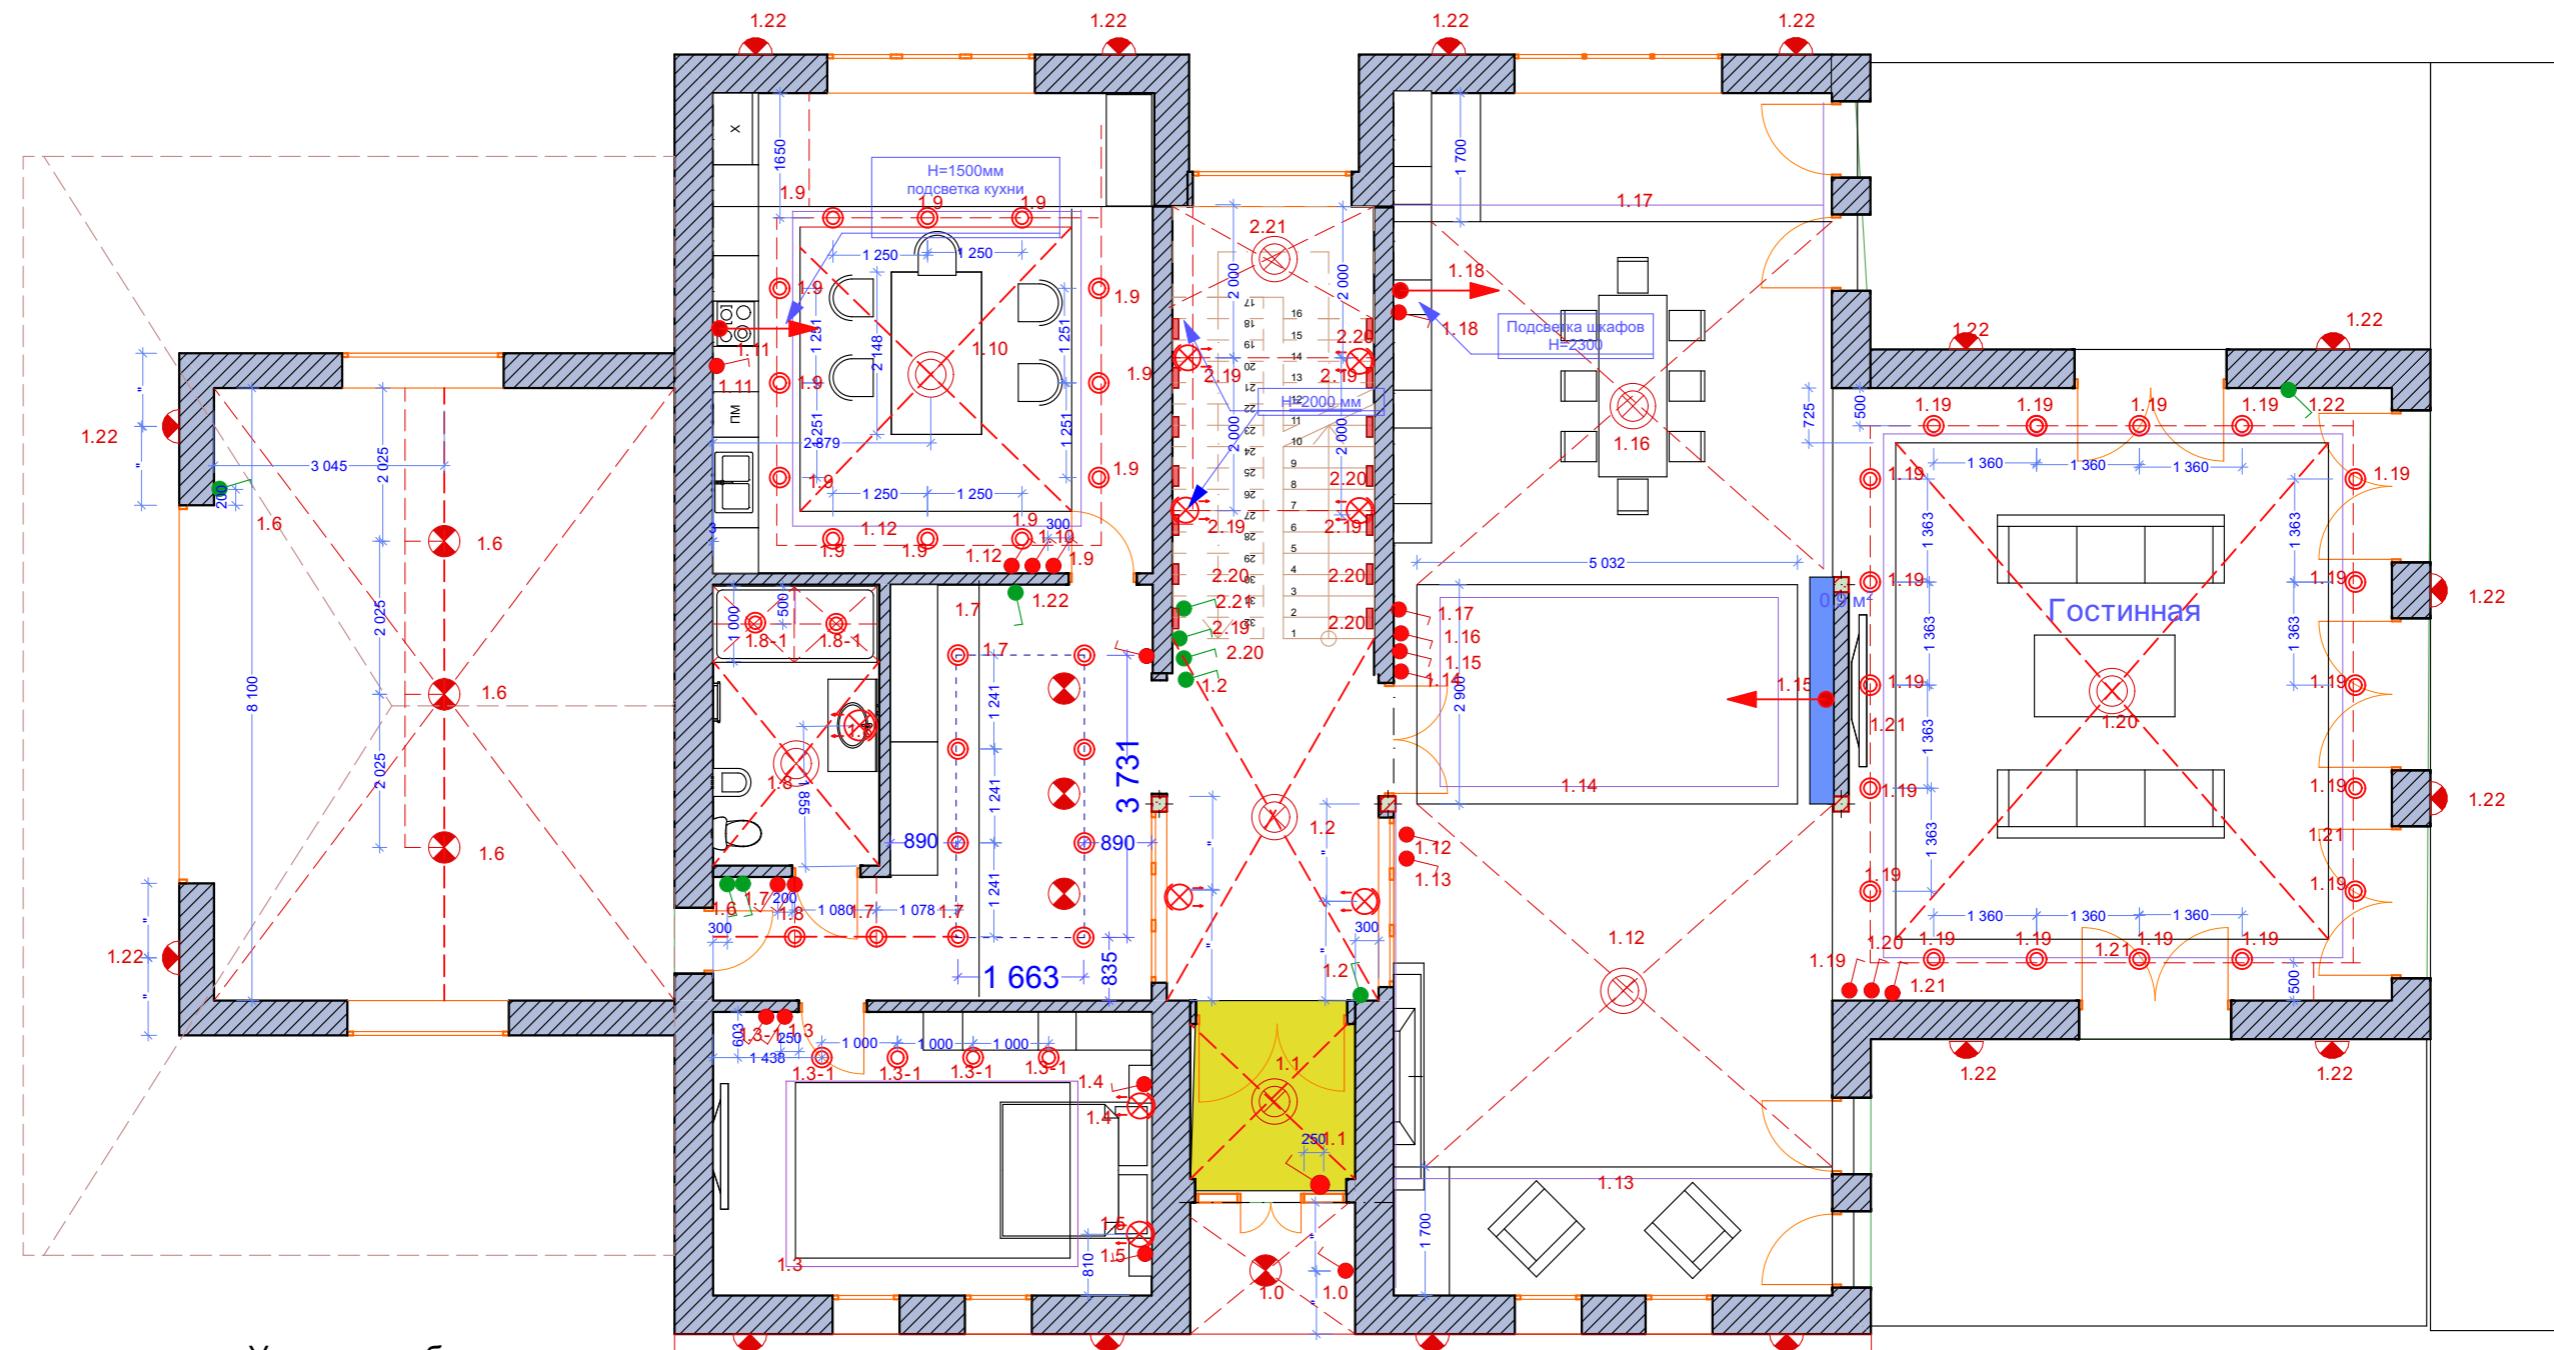

()- потолочные светильники (не менее 60 Вт)

энергосберегающая лампа

()- бра на отм.+1.800 от Ч.П. этажа

энергосберегающая лампа

()- точечные светильники

- подсветка пола в стене 250 мм от чистого пола

()- бра на отм. +1.600 от Ч.П. этажа Герм.

выводы под подсветку

00 группа включения

зеленый проходные переключатели

красный - переключ. на отм. +1.000 от Ч.П. этажа



Частный дом. ЖК МонакоВо!

Дом у Озера


2.9

Масштаб 1:100

Дизайнер Т. Астафьев 8 915 360 0663

Лист 47 из 11

# Схема расположения светильников 2-й этаж

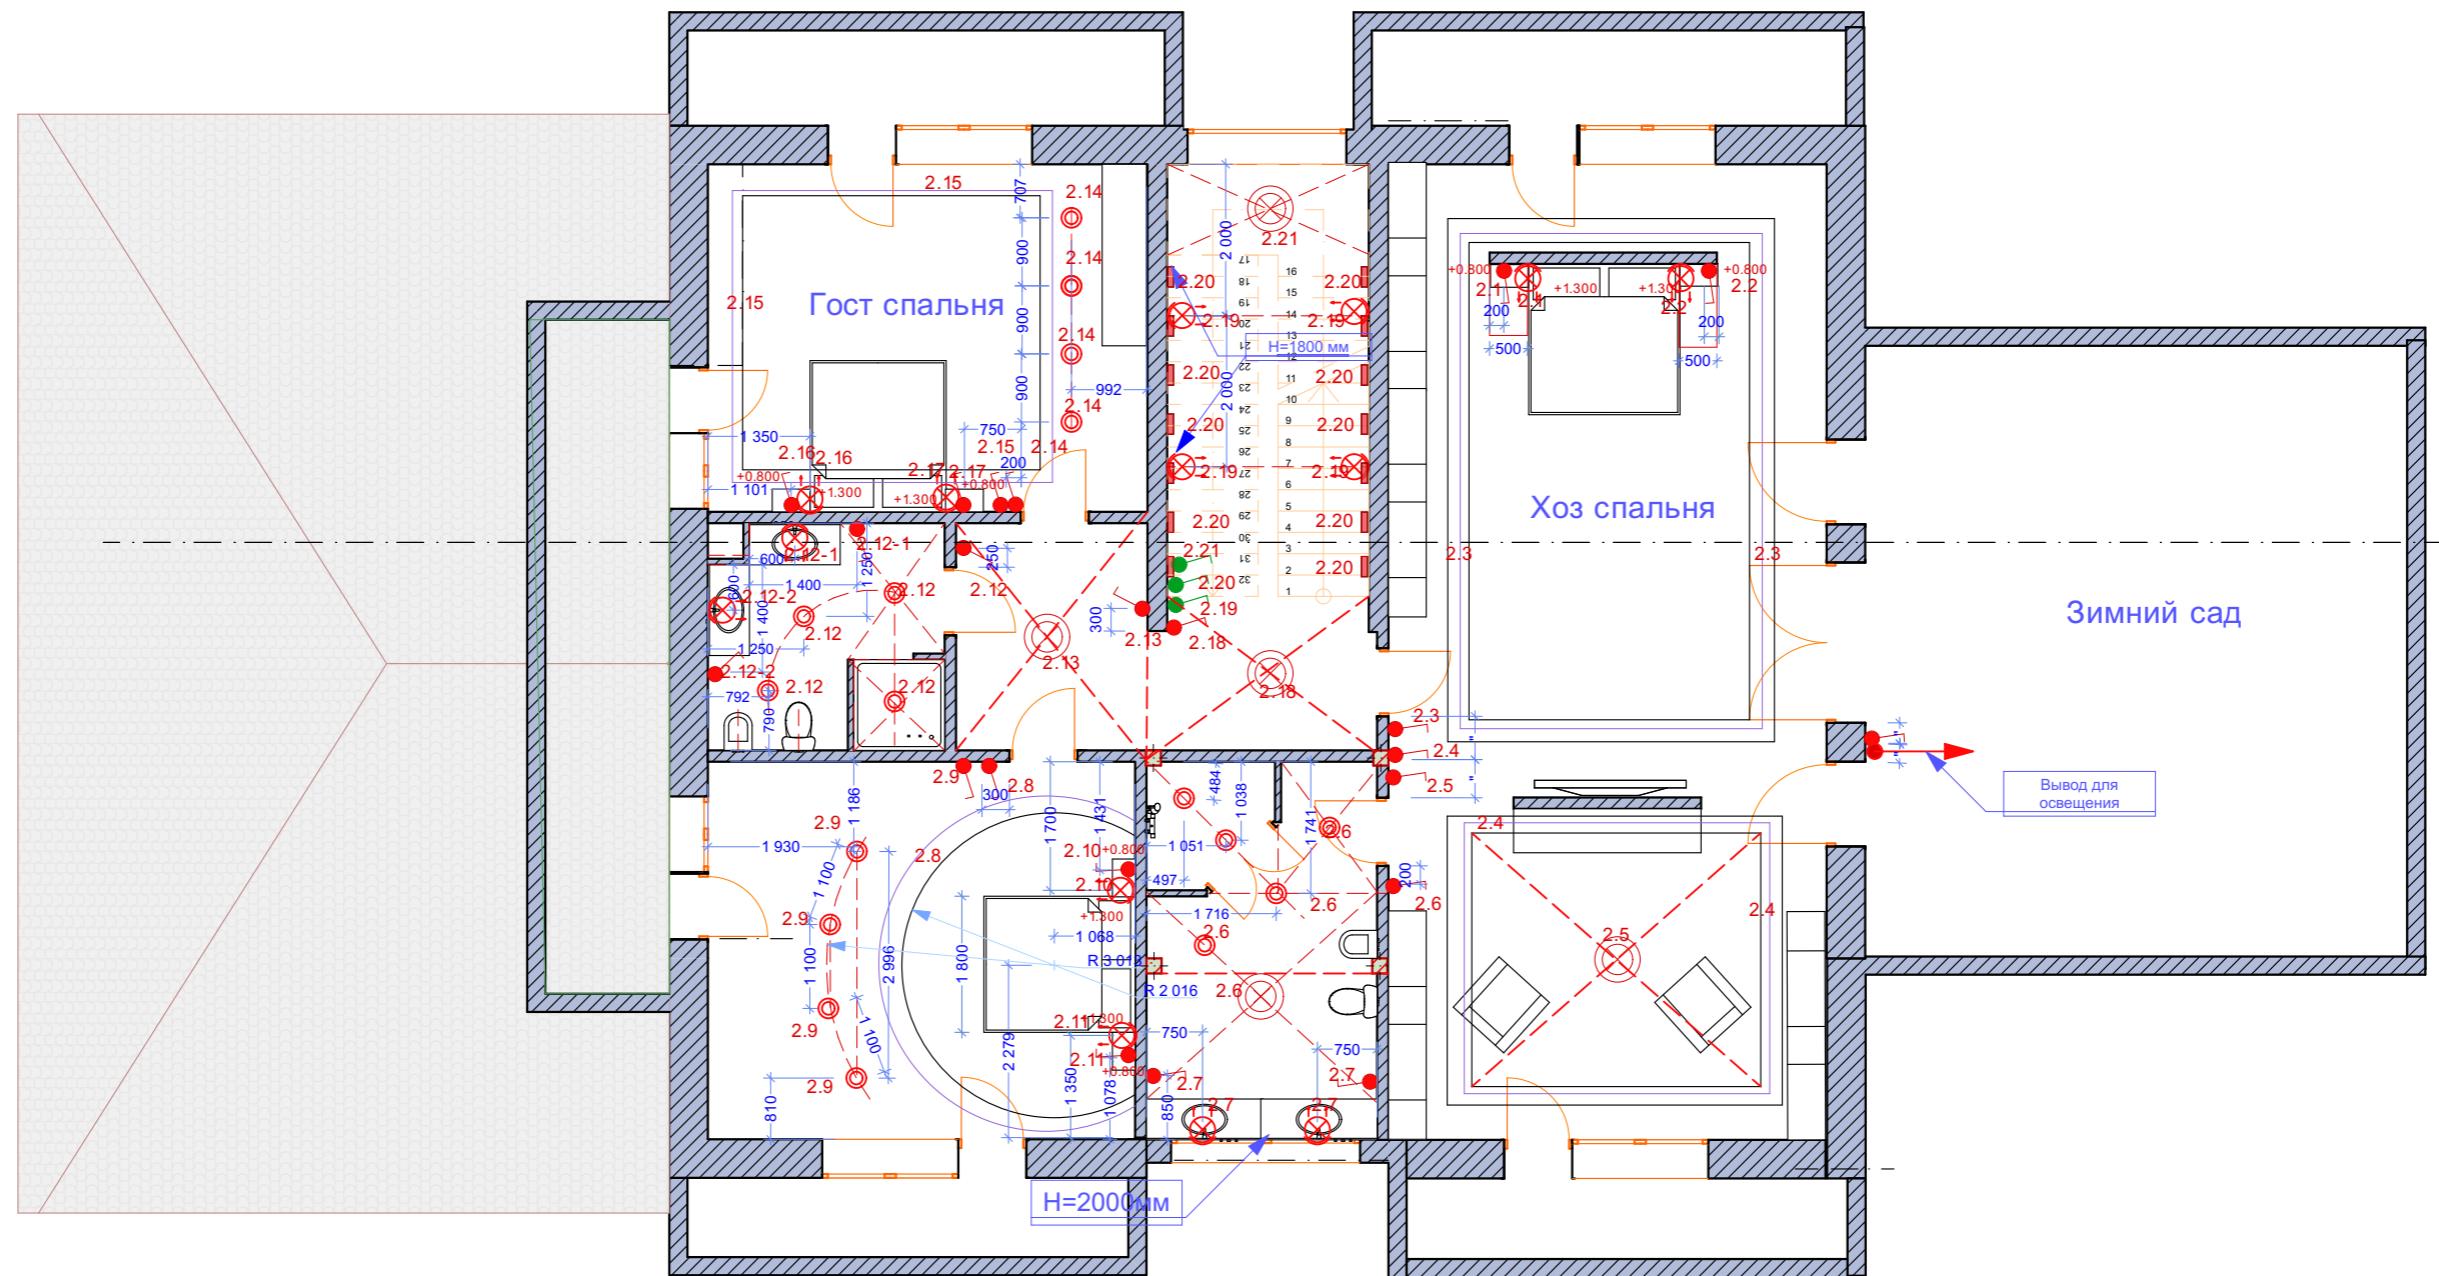

## Условные обозначения:

### УСЛОВНЫЕ ОБОЗНАЧЕНИЯ

- ()- потолочные светильники (не менее 60 Вт) энергосберегающая лампа
- ()- бра на отм.+1.800 от Ч.П.этажа энергосберегающая лампа
- ()- точечные светильники
- подсветка пола в стене 250 мм от чистого пола

()- однорожковые светильн. Герм.

()- бра на отм. +1.600 от Ч.П. этажа Герм.

- выводы под подсветку

00- группа включения


- проходные переключатели

- переключ. на отм. +1.000 от Ч.П. этажа

### ПРИМЕЧАНИЯ

БЛОКИ ВЫКЛЮЧАТЕЛЕЙ (КРОМЕ ОГОВОРЕННЫХ)  
НА ОТМ. 1.000 ОТ Ч.П. ЭТАЖЕЙ  
ПРИВЯЗКИ ДАНЫ ПО ЦЕНТРУ БЛОКОВ

ВСЕ ОТМЕТКИ ДАНЫ ОТ ЧИСТОГО ПОЛА !!!

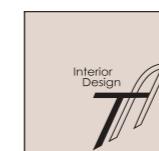

Частный дом. ЖК МонакоВо!


Дом у Озера

Масштаб 1:100

Дизайнер Т. Астафьев 8 915 360 0663

Лист 48 из 11

# Схема расположения теплых полов цокольный этаж

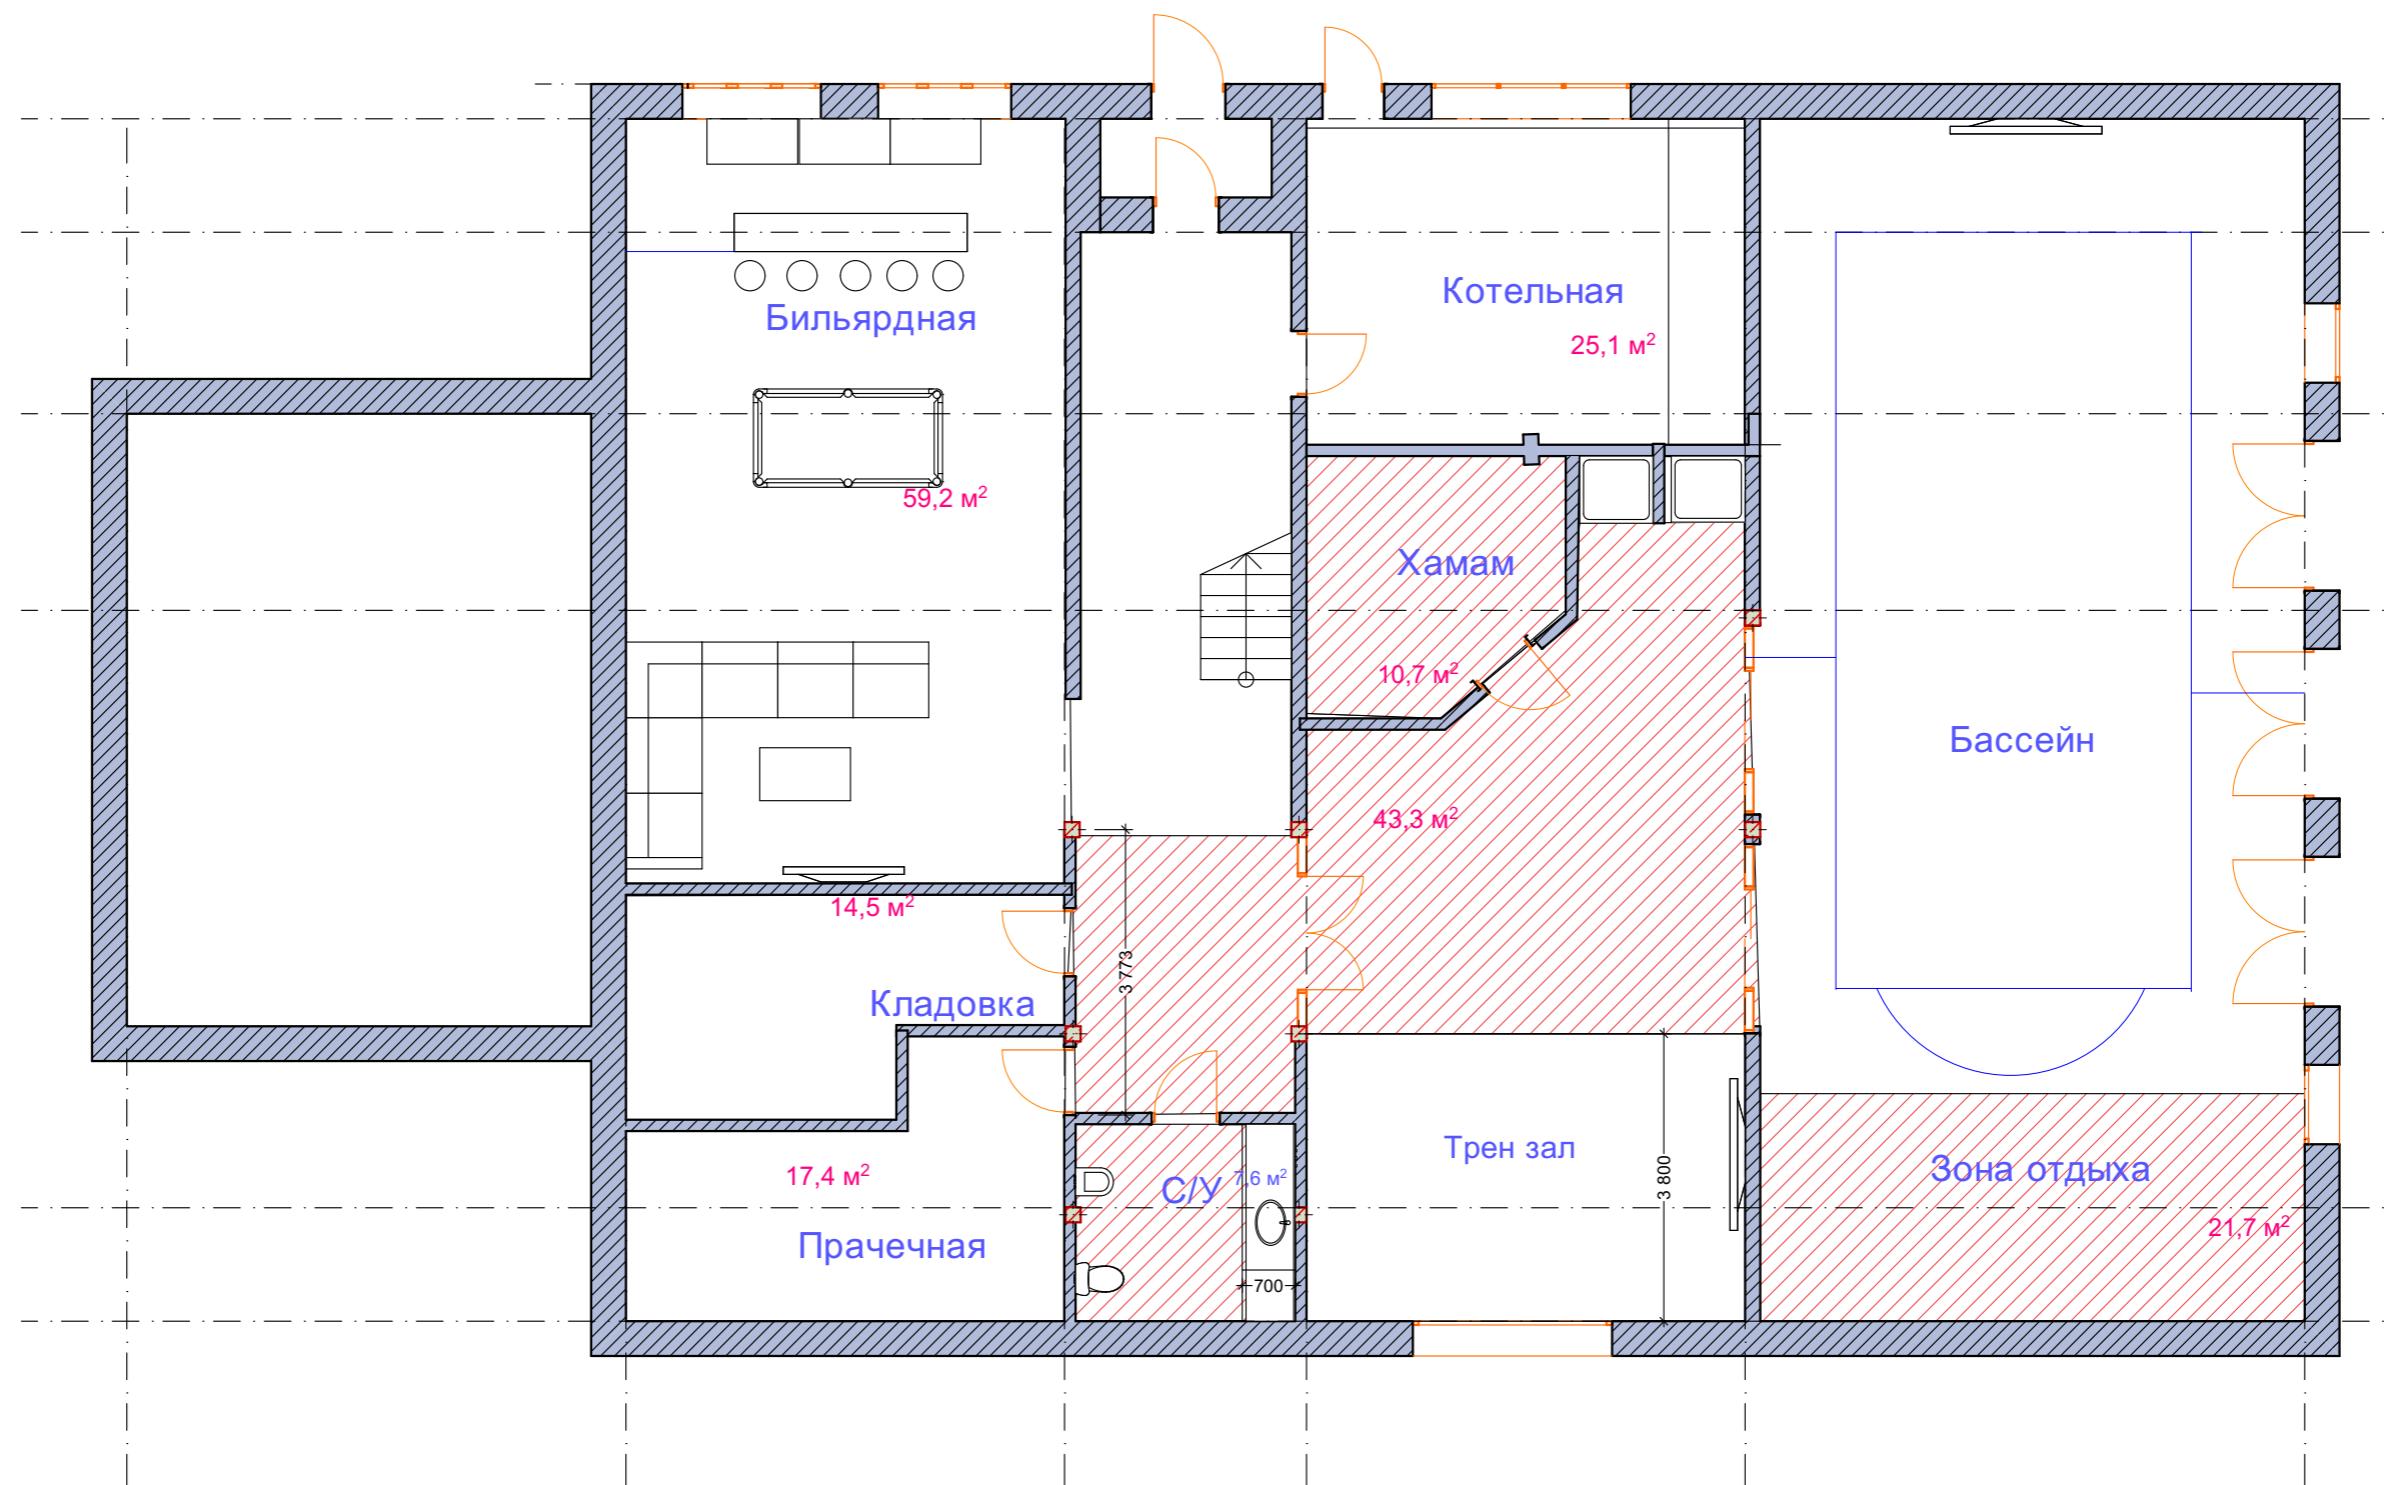

Условные обозначения :



- теплый пол



Частный дом. ЖК МонакоВо!


Дом у Озера

Масштаб 1:100

Дизайнер Т. Астафьев 8 915 360 0663

Лист 49 из 11


# Схема расположения теплых полов 1 этаж

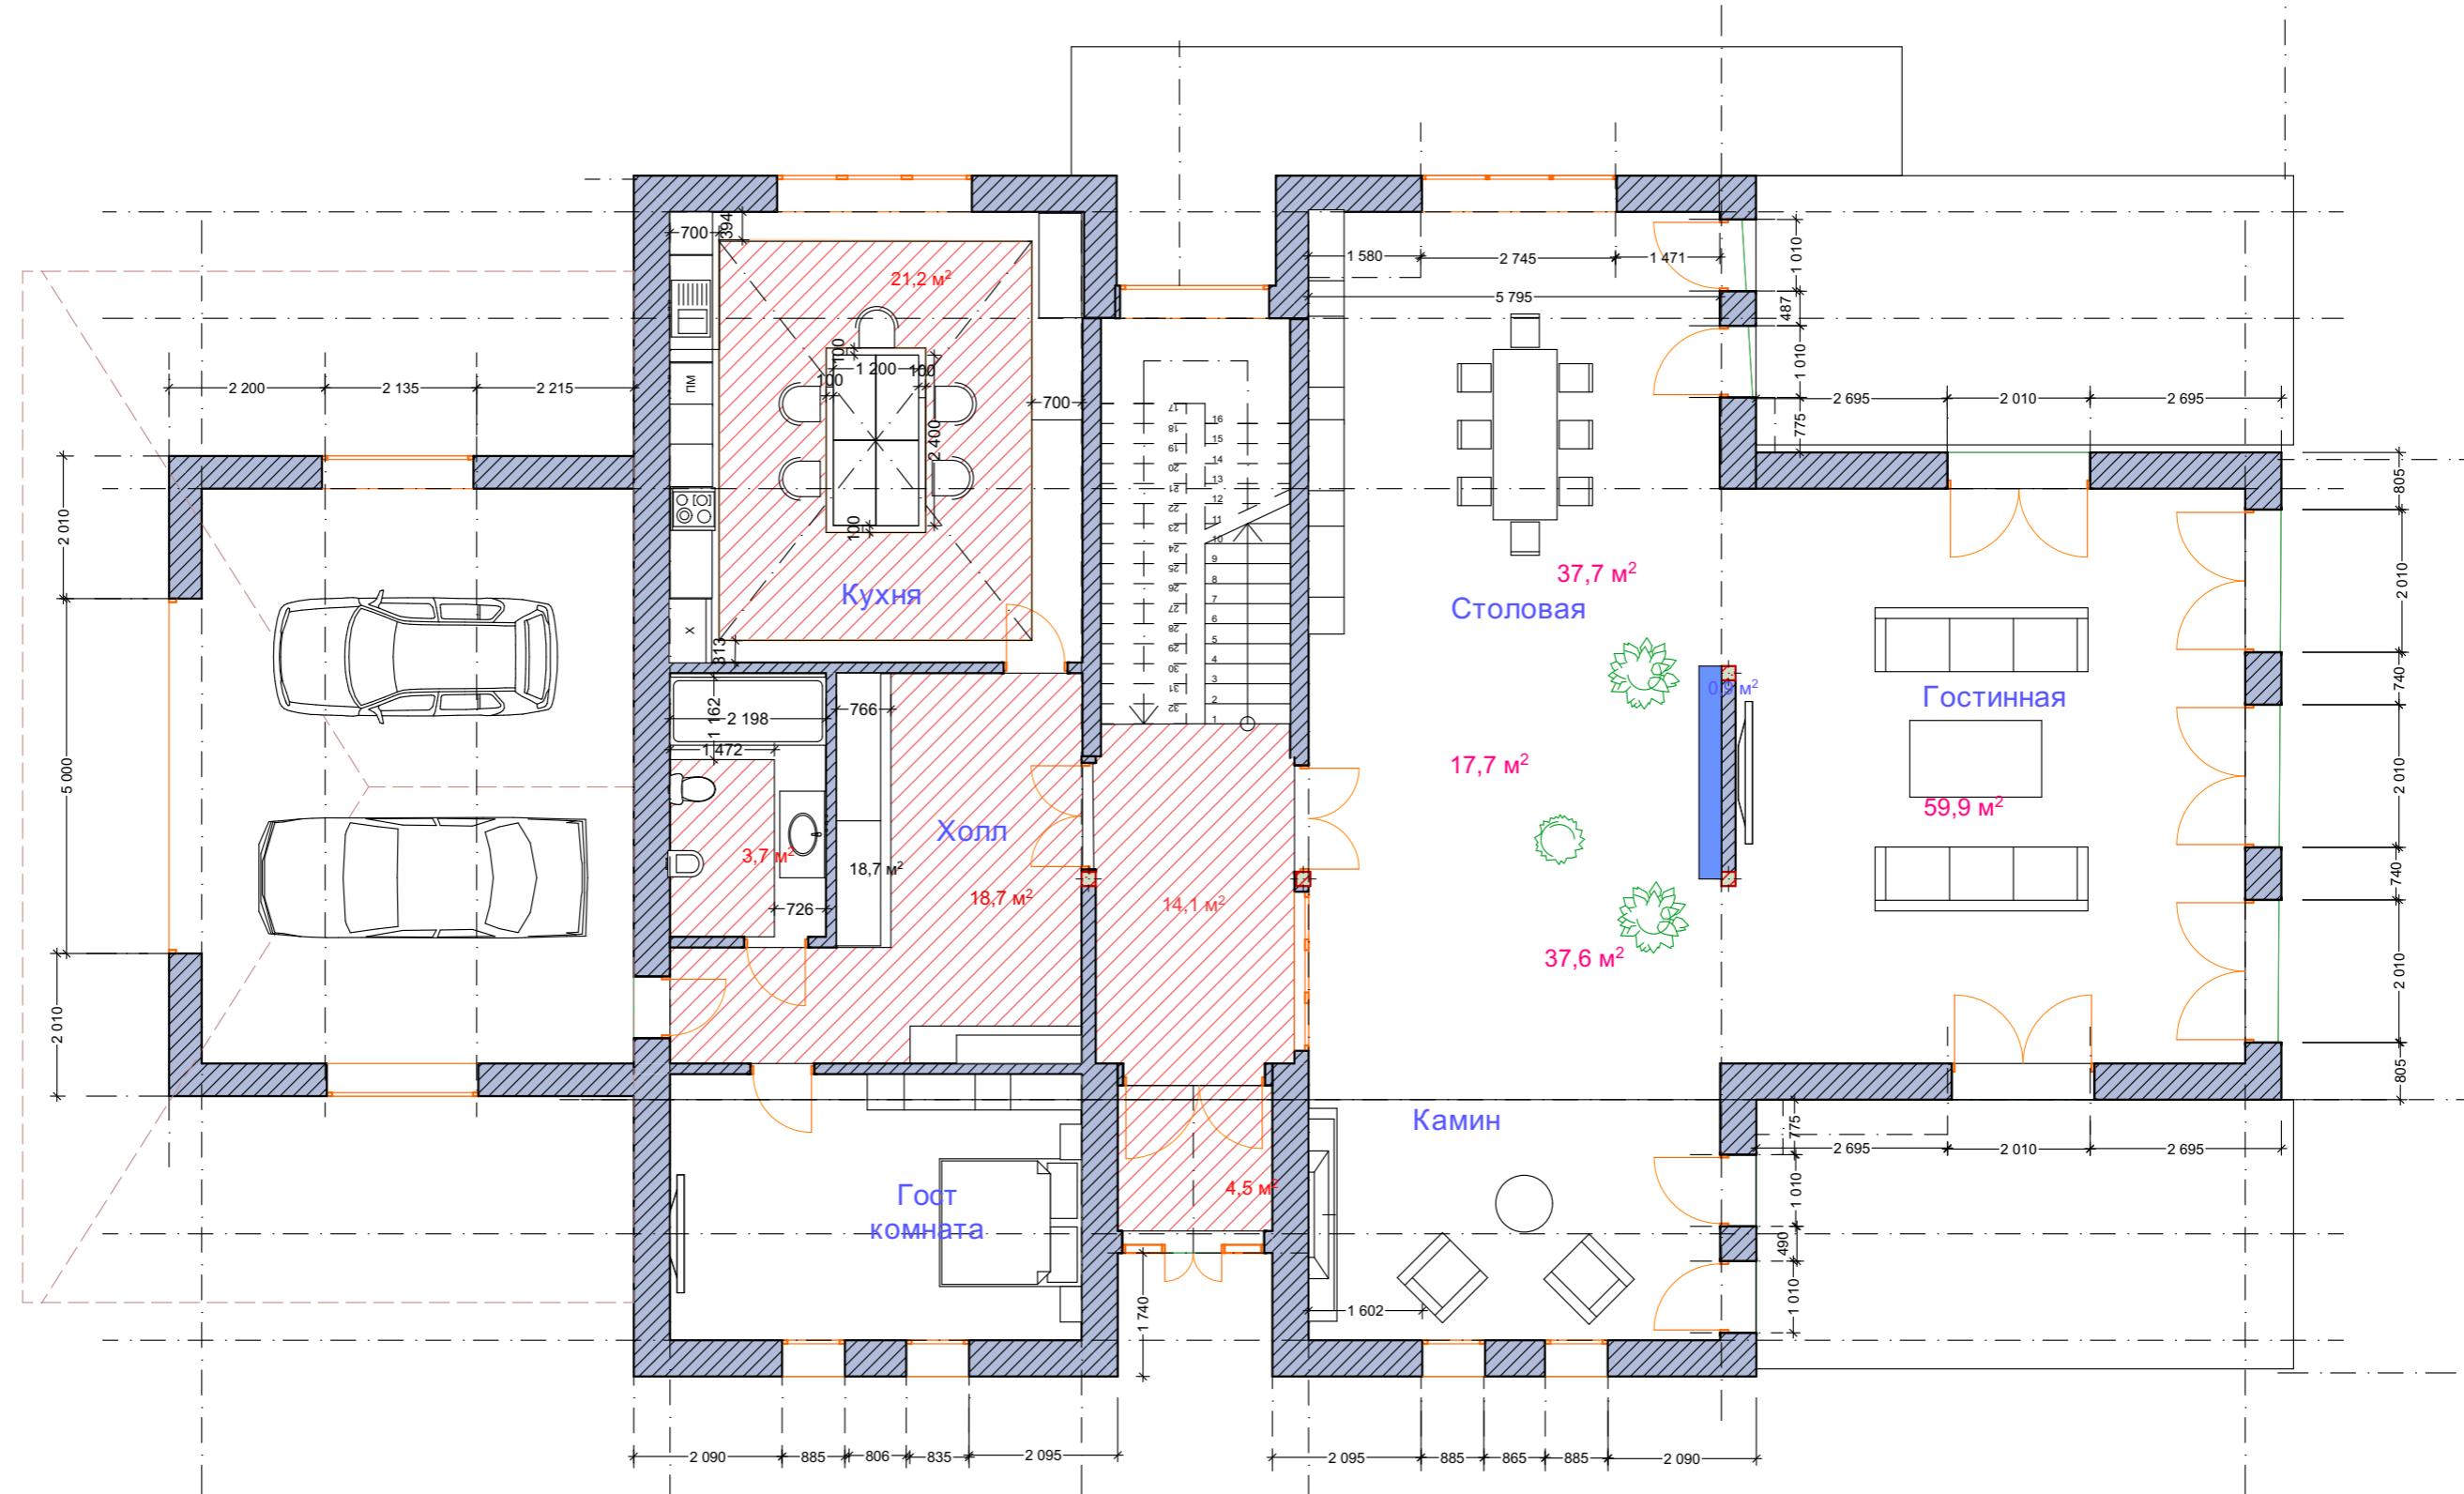

Условные обозначения :



- теплый пол

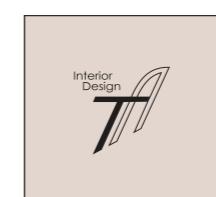

Частный дом. ЖК МонакоВо!


Дом у Озера

Масштаб 1:100

Дизайнер Т. Астафьев 8 915 360 0663

Лист 50 из 11


## Схема расположения теплых полов 2-й этаж

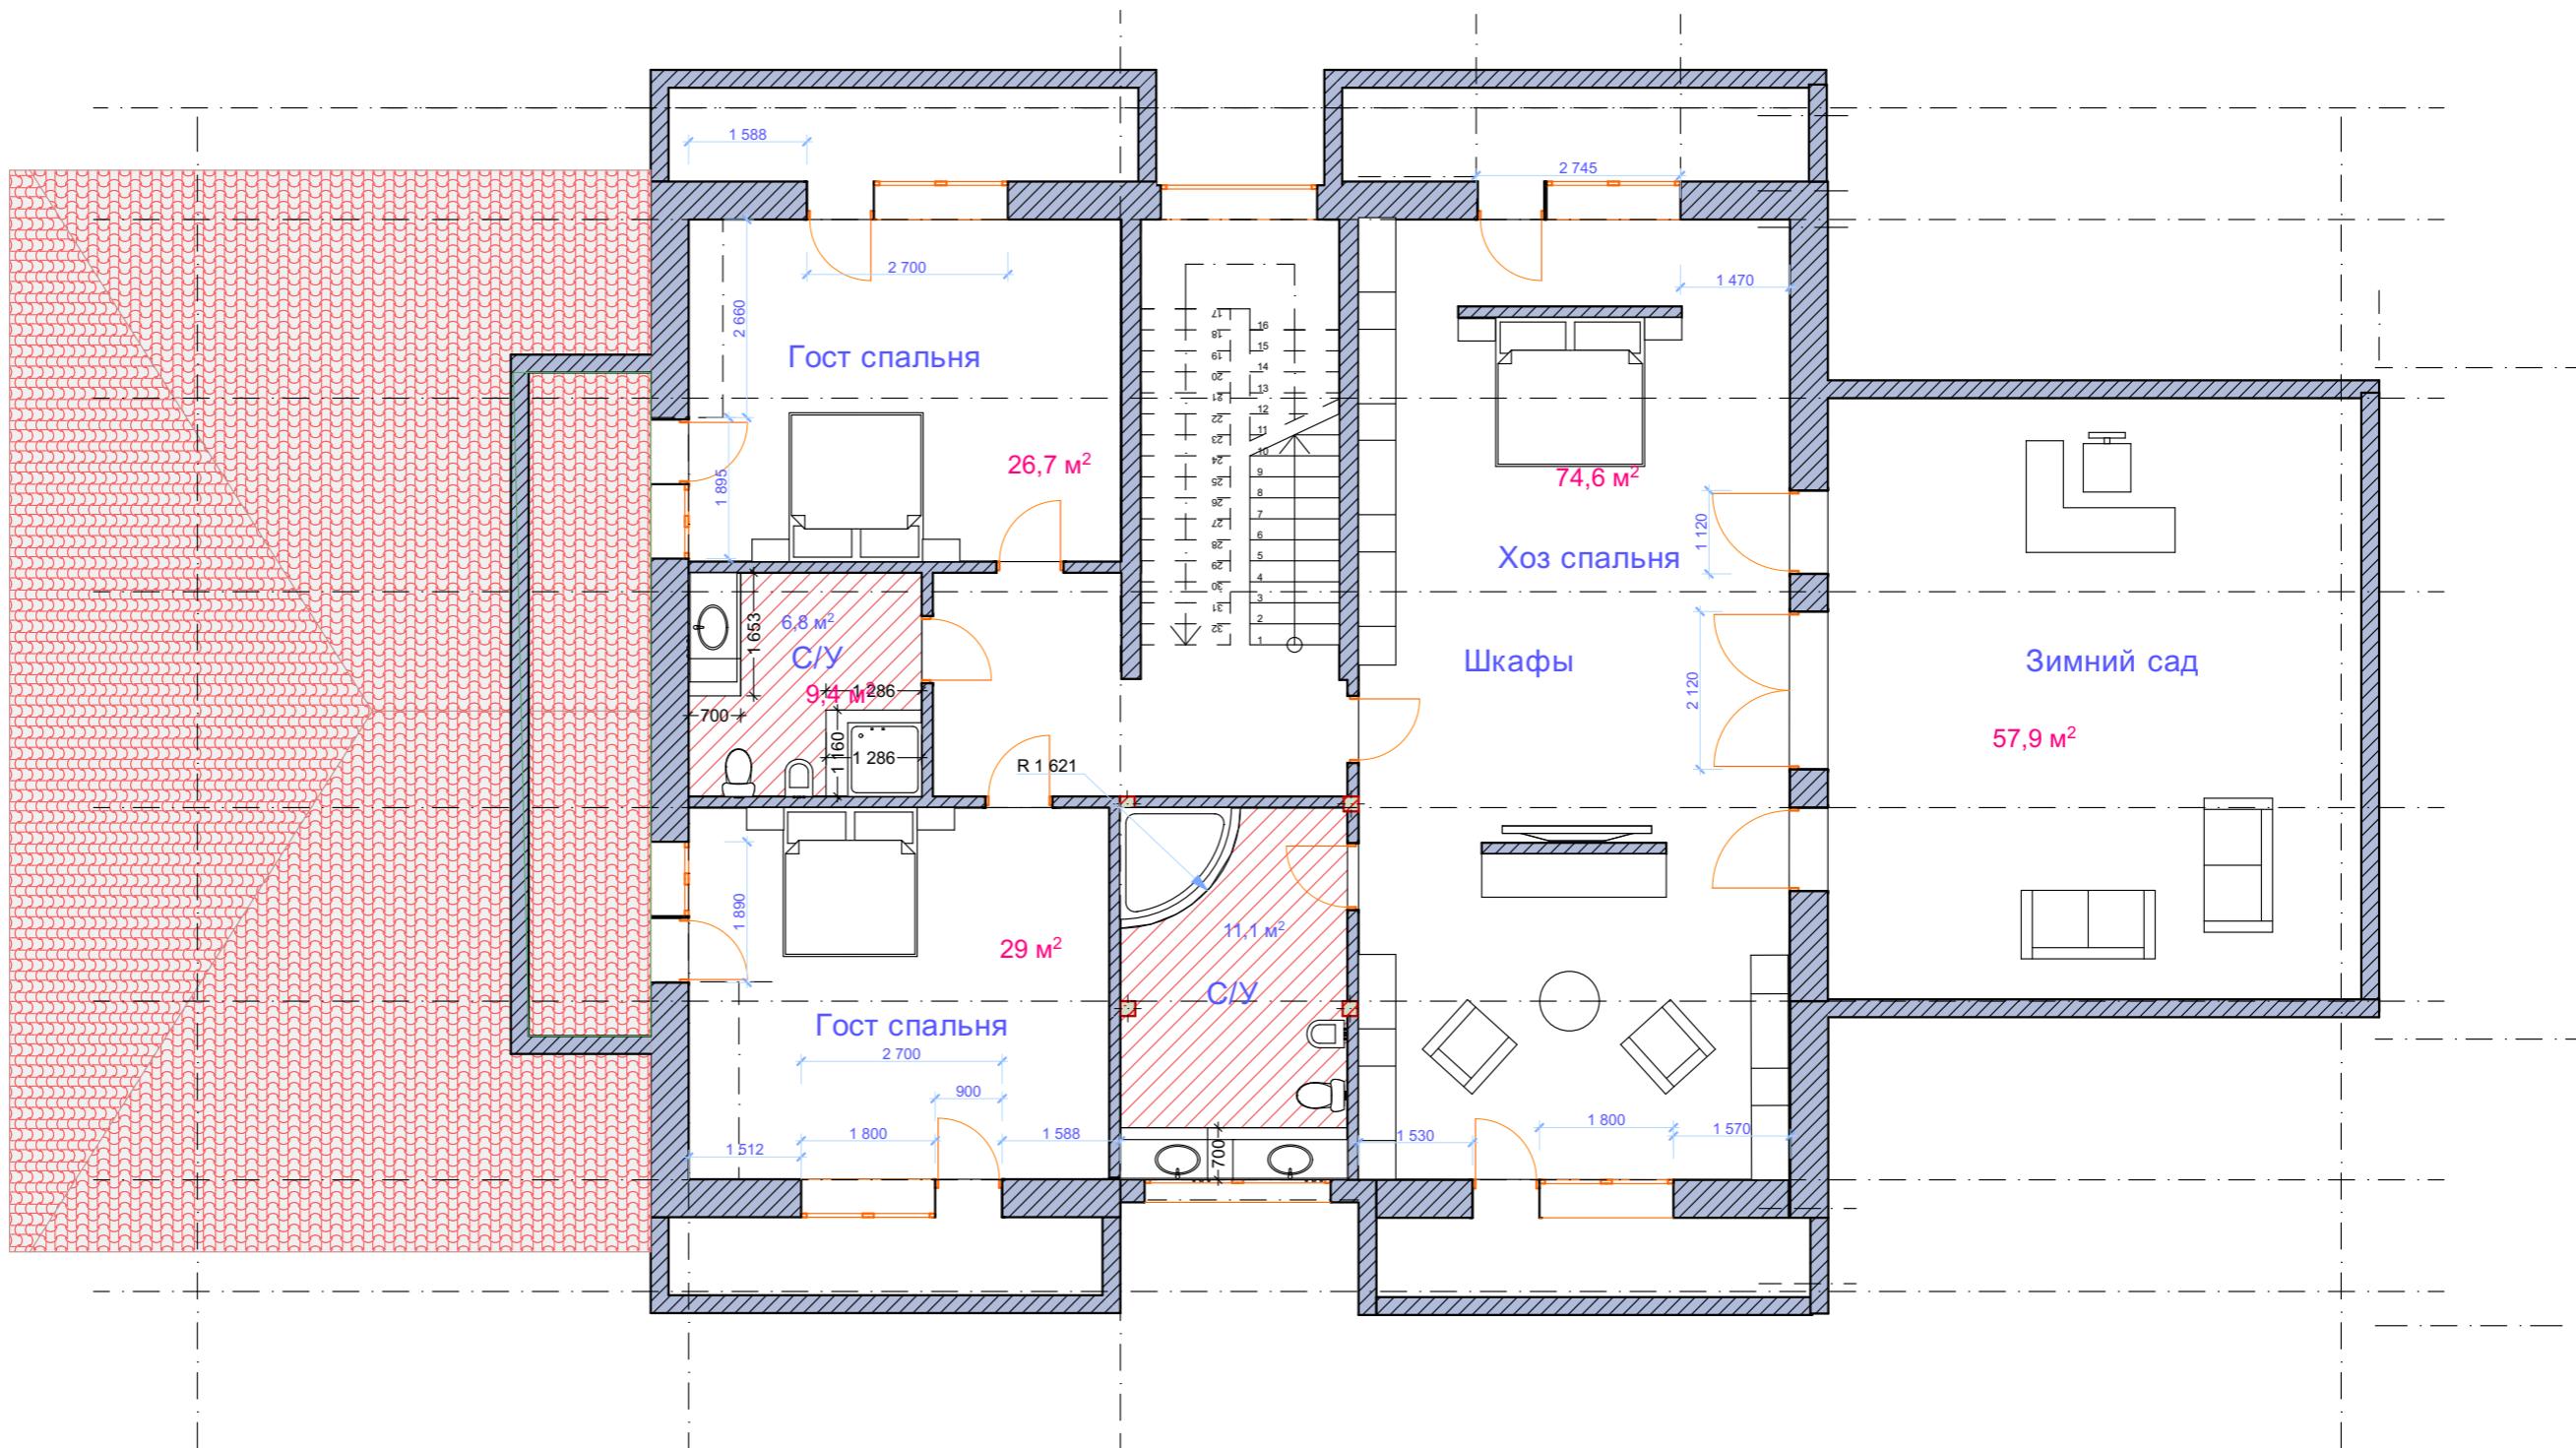


 Interior Design	Частный дом. ЖК МонакоВо!
	Дом у Озера
	Масштаб 1:100
	Дизайнер Т. Астафьев 8 915 360 0663

## *Дизайн-проект камина*


## *Фронтальный вид*

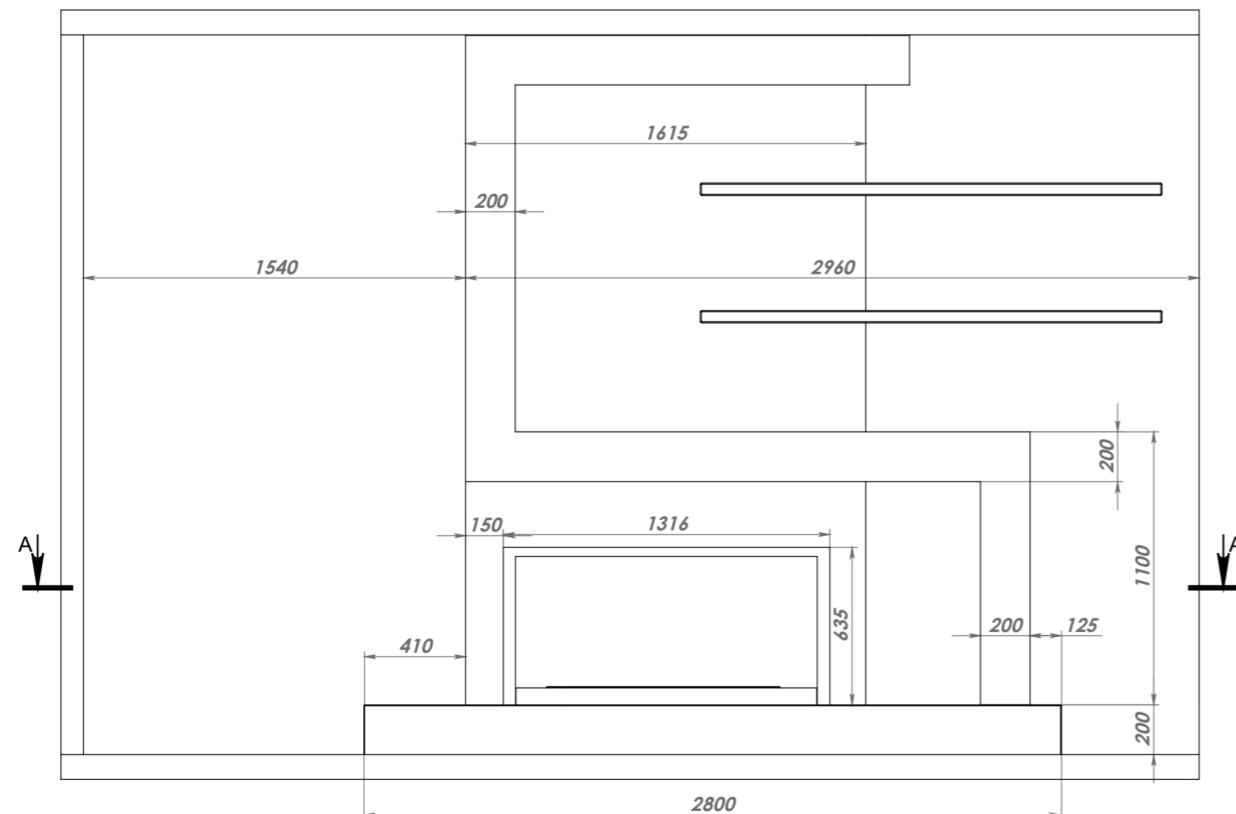

## *Вид сверху*

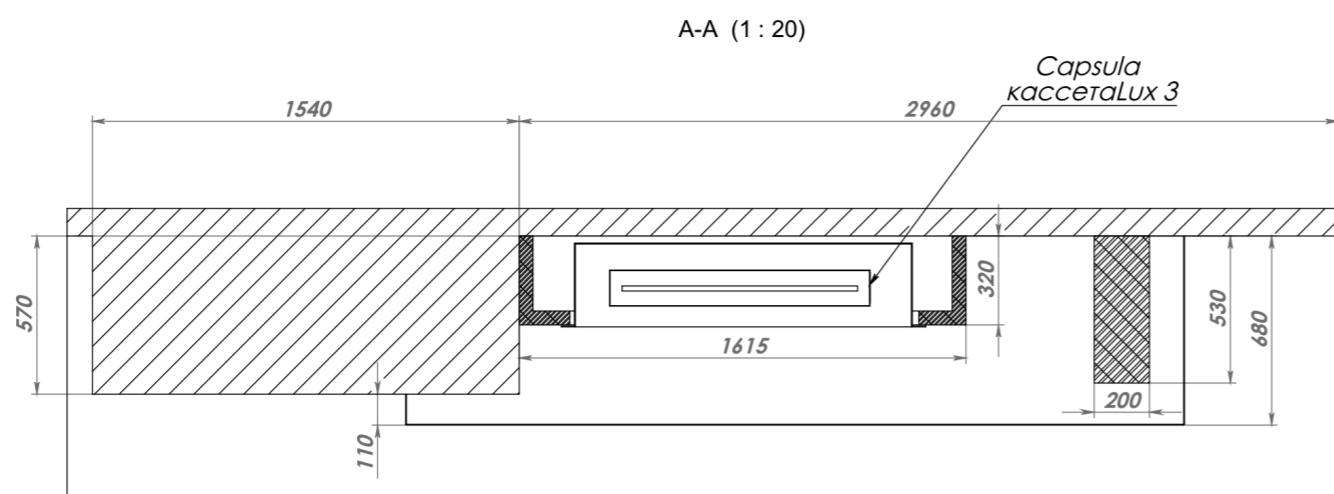

*Разрез всего дома с лестницей*

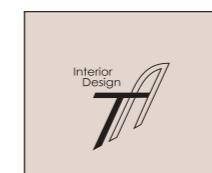

Частный дом. ЖК МонакоВо!



Дом у Озера

Масштаб 1:100

Дизайнер Т. Астафьев 8 915 360 0663

Лист 53 из 11

# Конструктивный узел

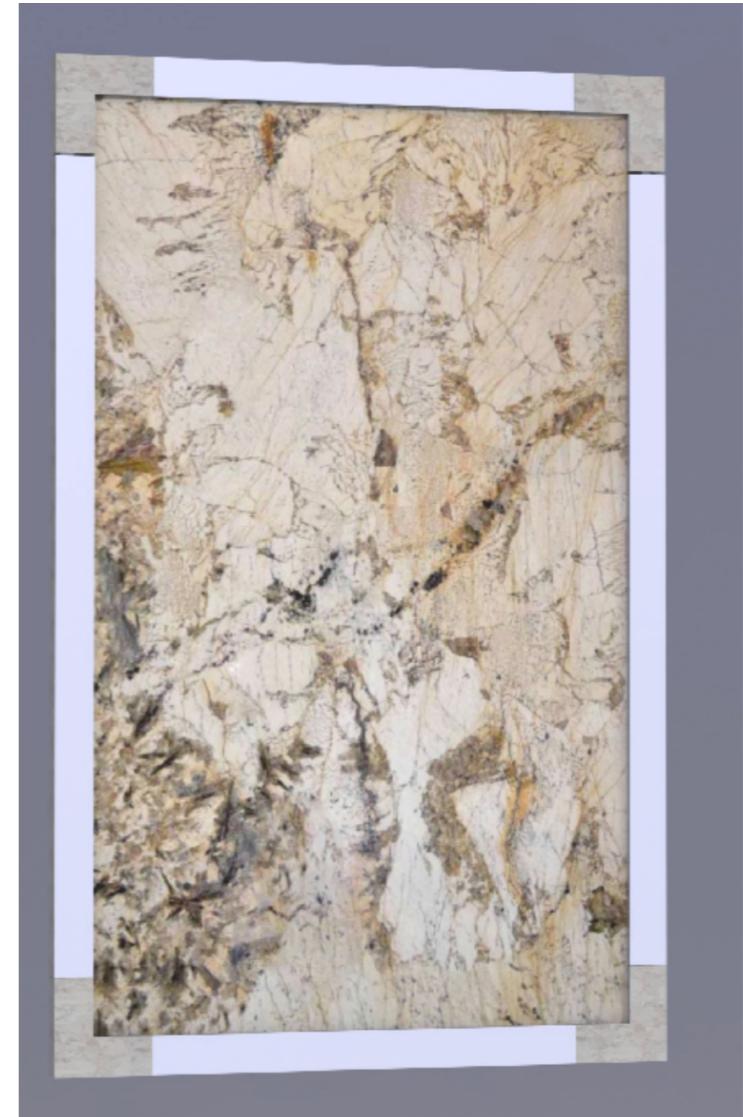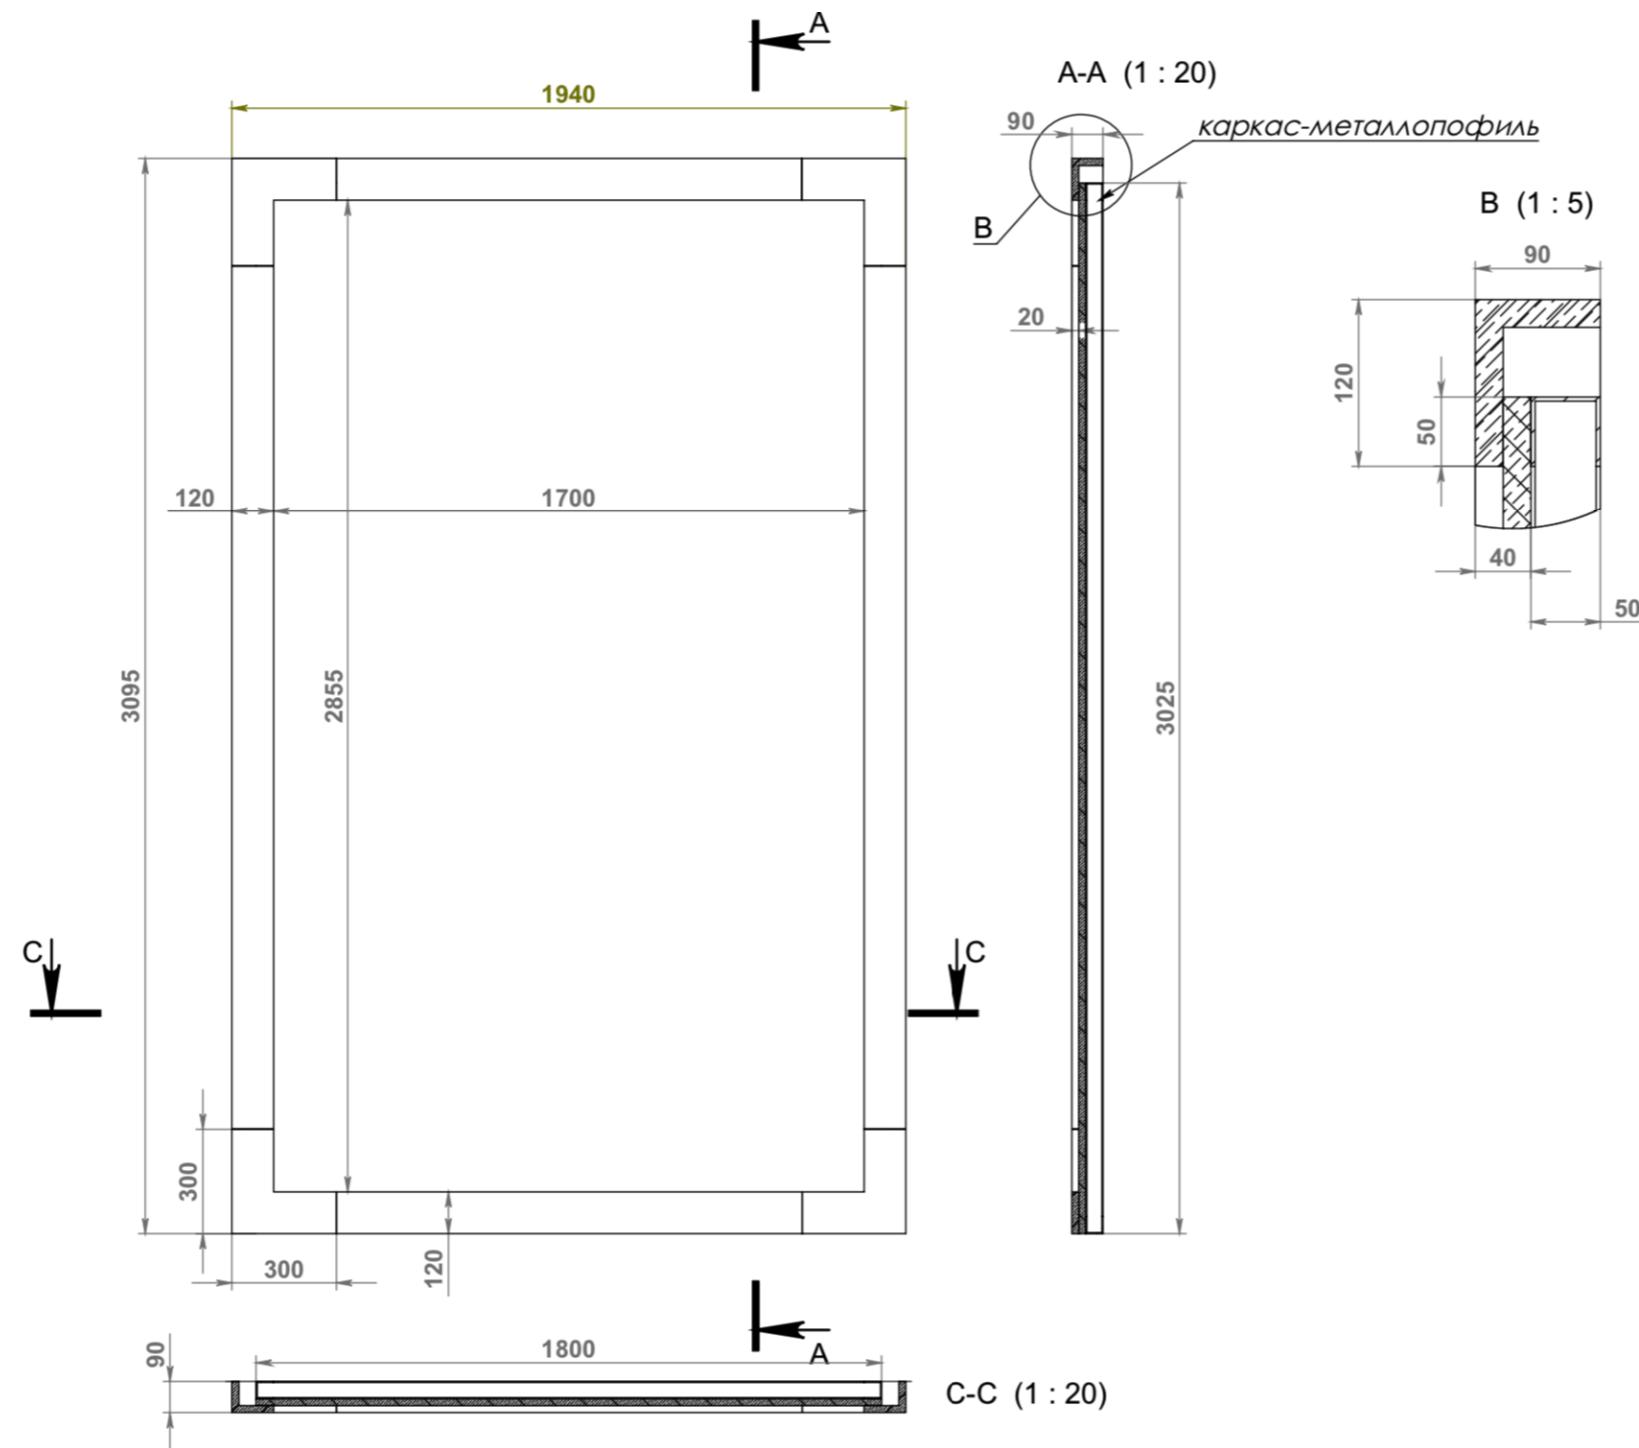

	Частный дом. ЖК МонакоВо!	
	Дом у Озера	Масштаб
	Дизайнер Т. Астафьев 8 915 360 0663	
	Лист 54 из 11	

## Визуализация



## Визуализация



## Визуализация



*Визуализация*



## Визуализация



## Визуализация



*Визуализация*



## Визуализация



# Визуализация



# Визуализация



## Визуализация



*Визуализация*



## Визуализация



*Визуализация*



## Визуализация



*Визуализация*



# Визуализация



*Визуализация*



## Визуализация

